


مصنع وتد الأخشاب · ملف التصميم

مجلس وحوش وغرفة نوم 9.00 × 13.00 م – الحوية


المساحة 117 م² • غرفة نوم 4.82 × 5.82 م • مستودع 4.82 × 1.88 م • حوش 3.82 × 7.82 م • مجلس 6.82 × 4.82 م • مغاسل وحمام • سقف متداخل • جدران 4.00 م

المسقط الأفقي مع الفرش

الأبعاد بالسنتيمتر - الجدران: قوائم 7×5 + تلبيس 2.5 من الجهتين (12 سم)

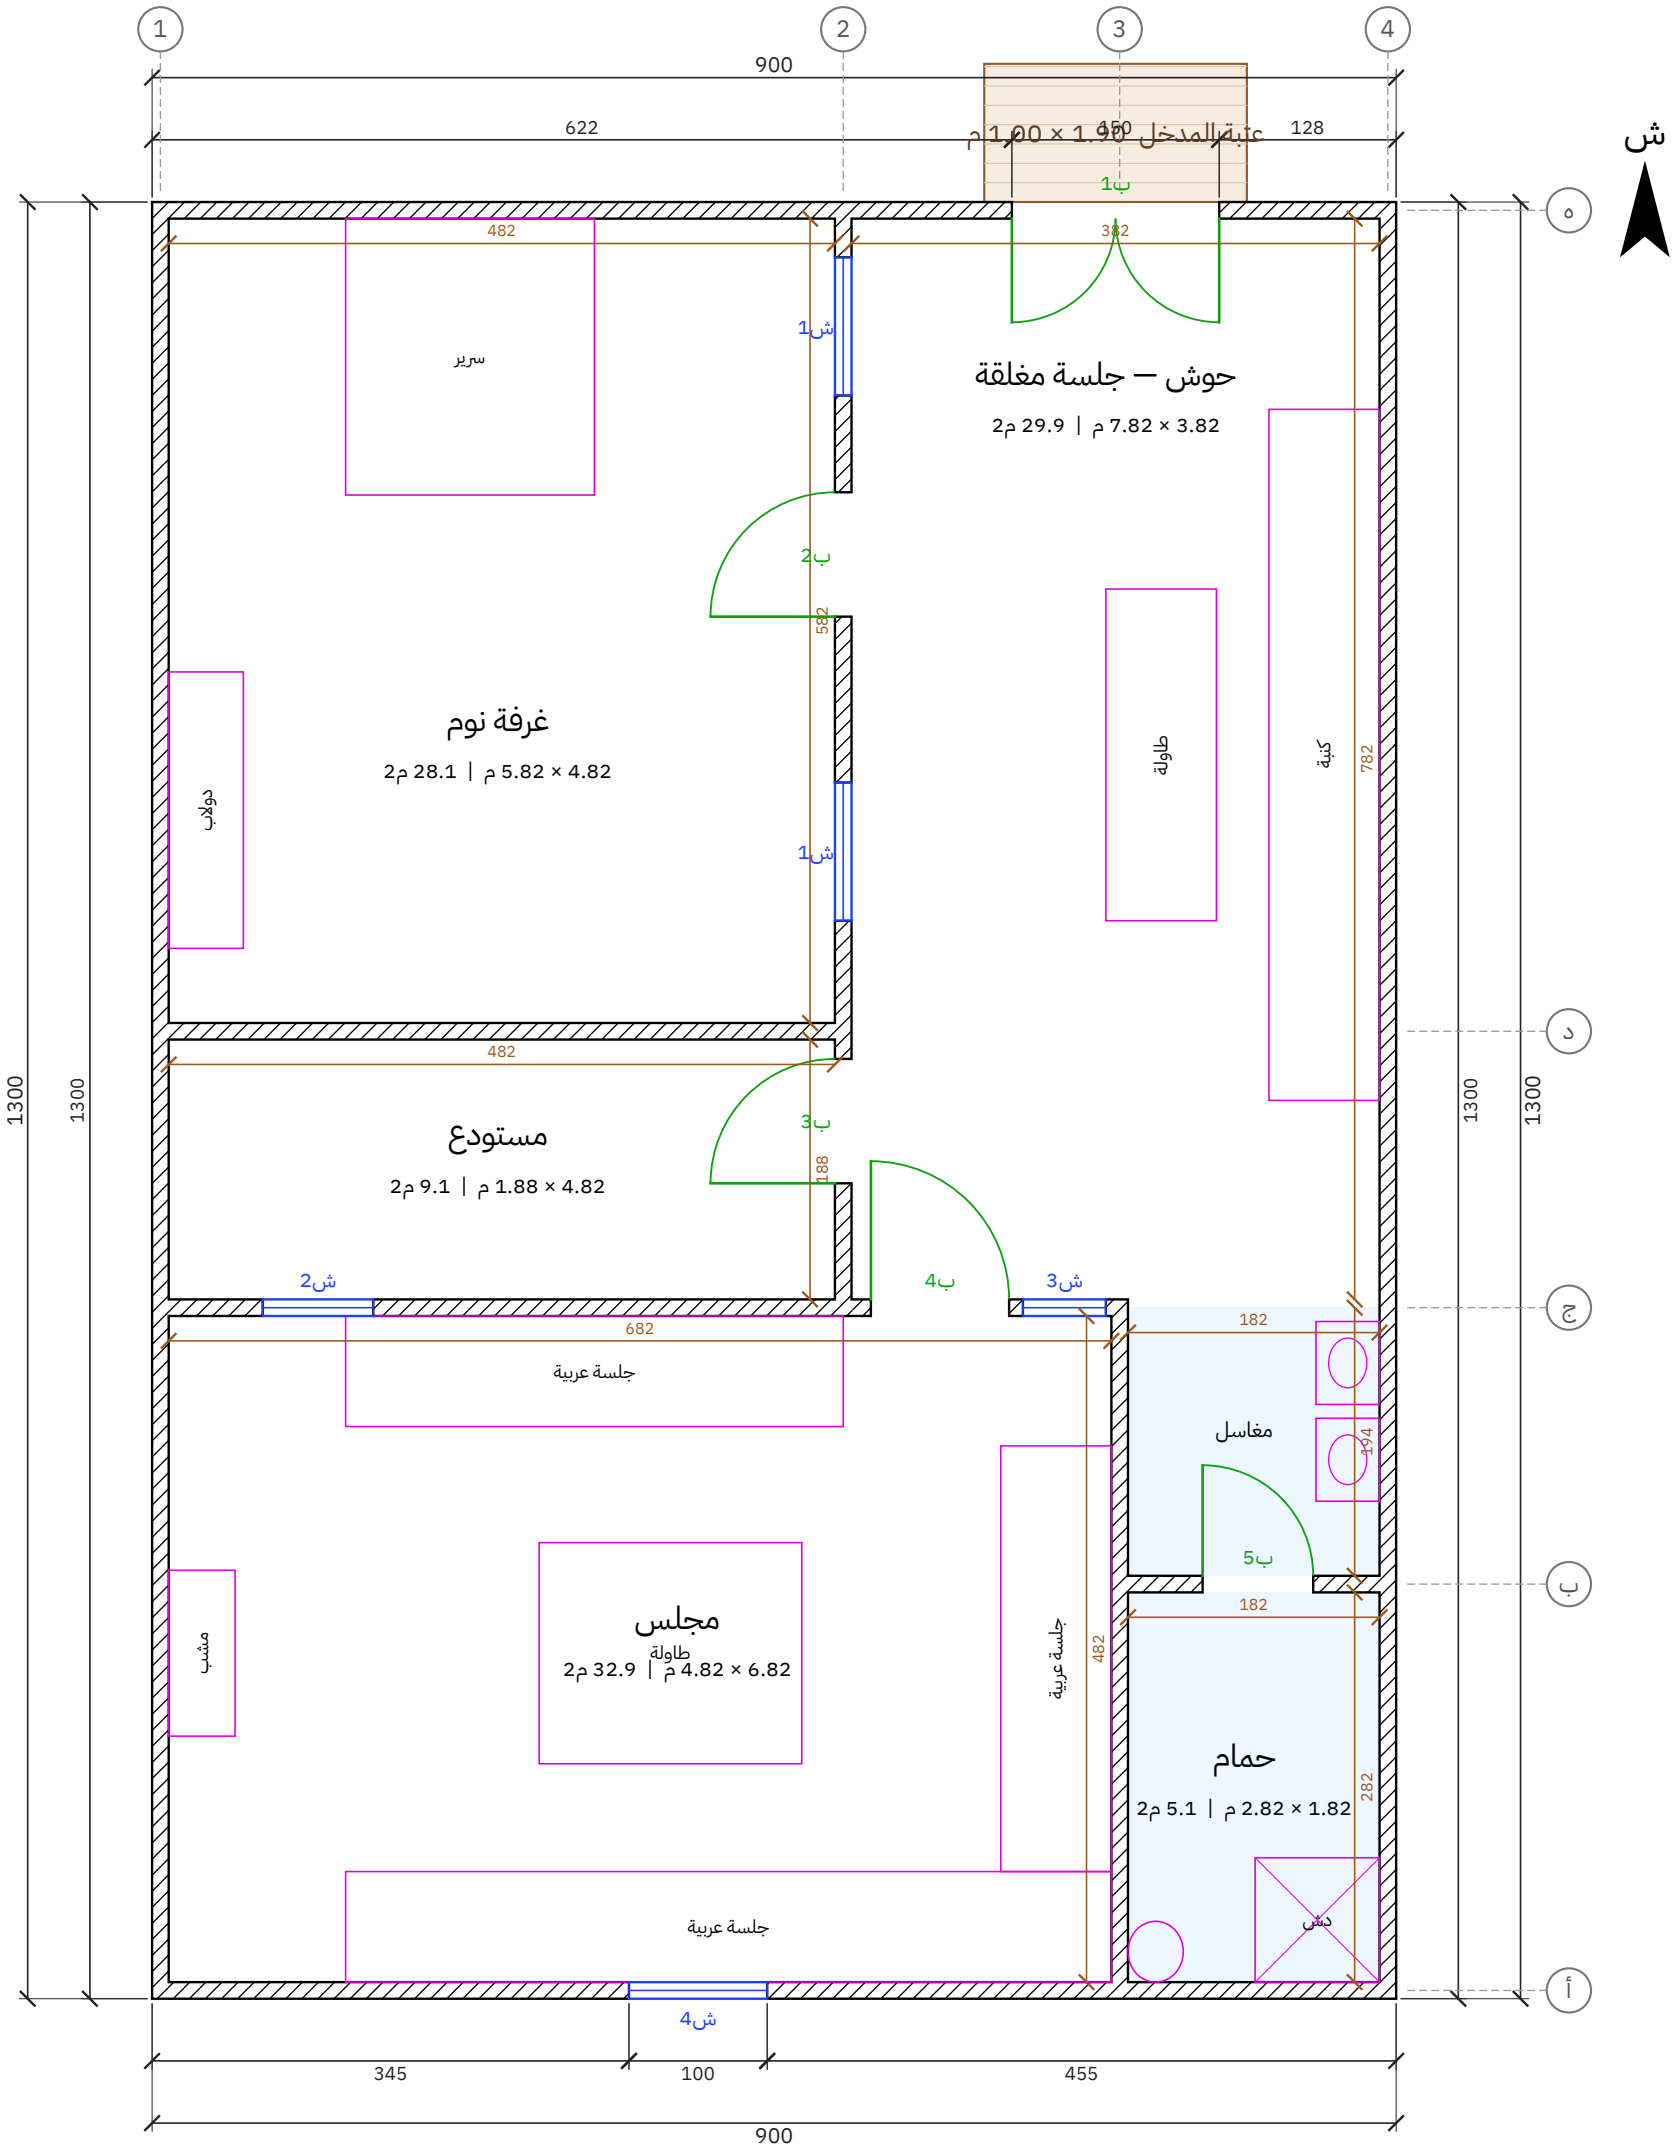


مصنع وتد الأخشاب Watad Wood Factory	المشروع / العميل مجلس وجلسة خارجية مغلقة وغرفة نوم 9.00 × 13.00 م — الحوية عميل — الحوية	عنوان اللوحة المسقط الأفقي	المقياس 1:50	التاريخ 2026-11-05	رقم اللوحة A-02 (2/10)

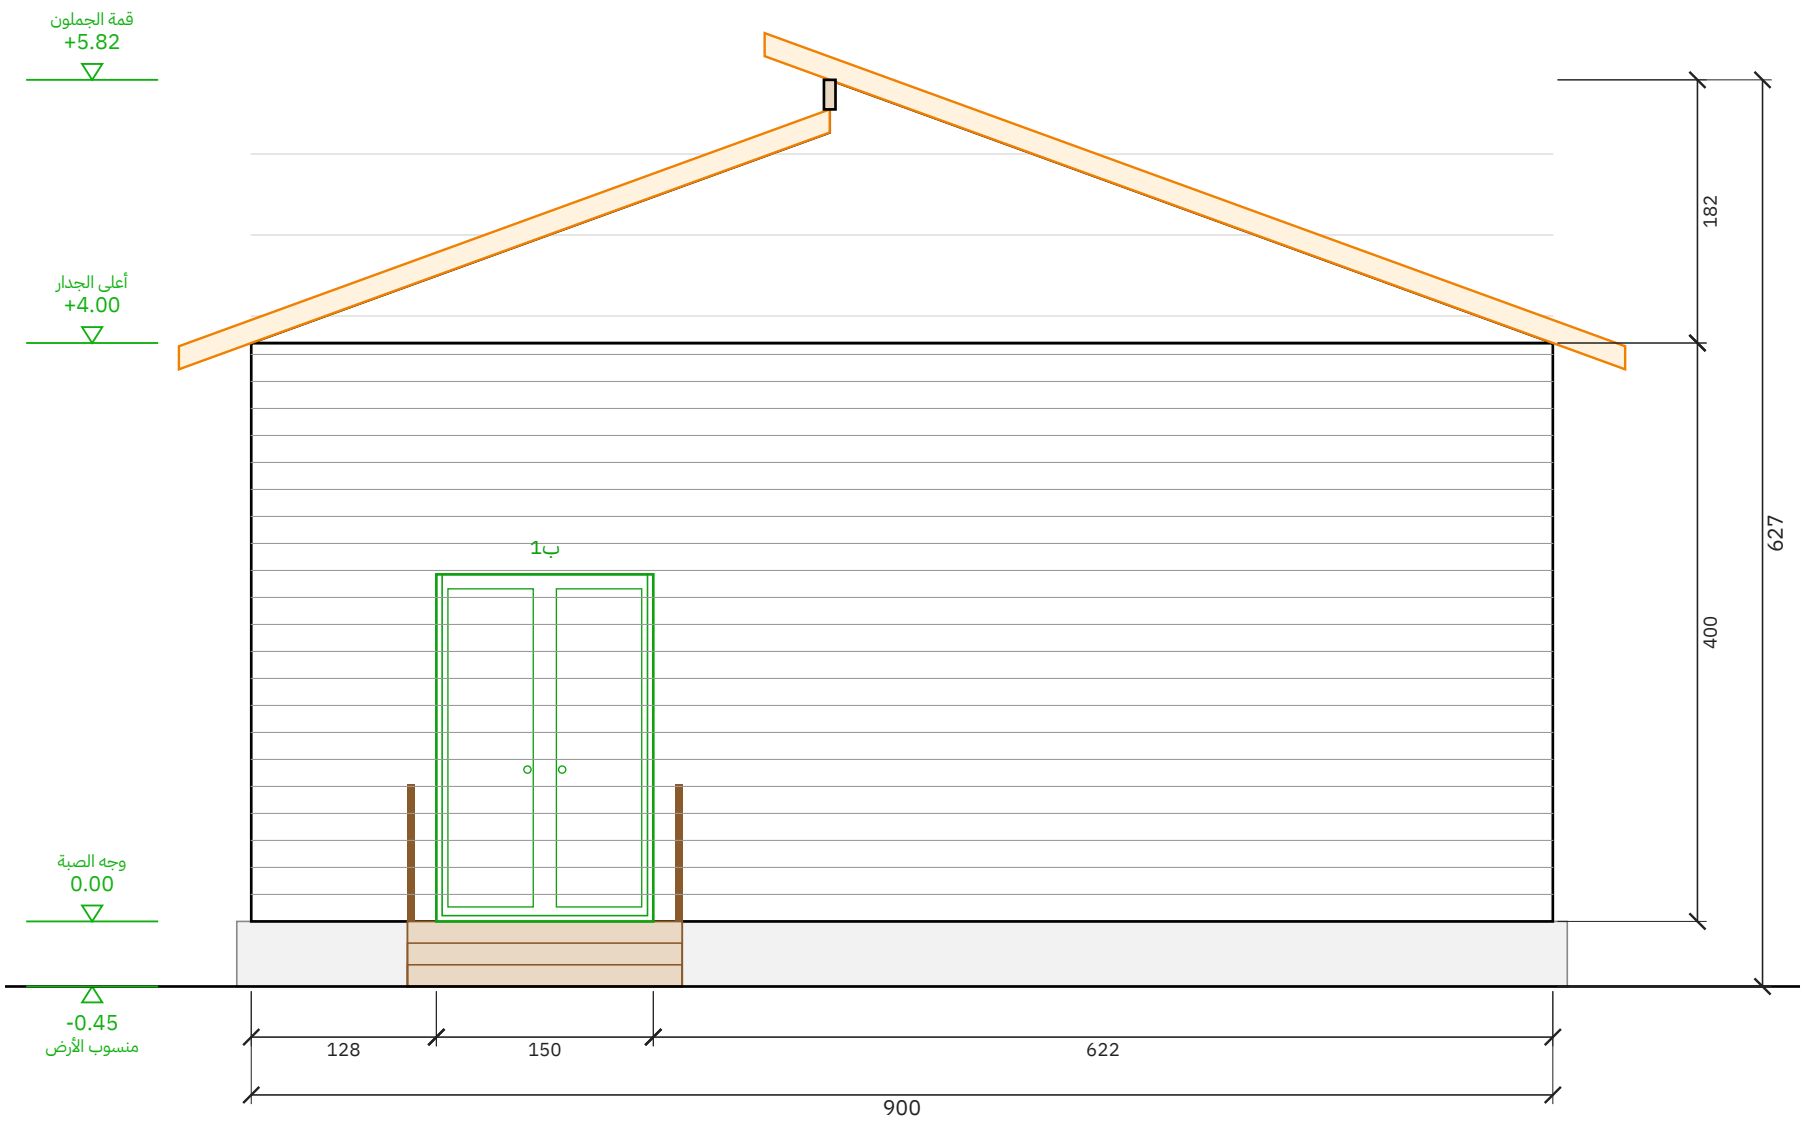

واجهة المدخل (أعلى المخطط)

مقياس 1:50 | الوحدة: سم

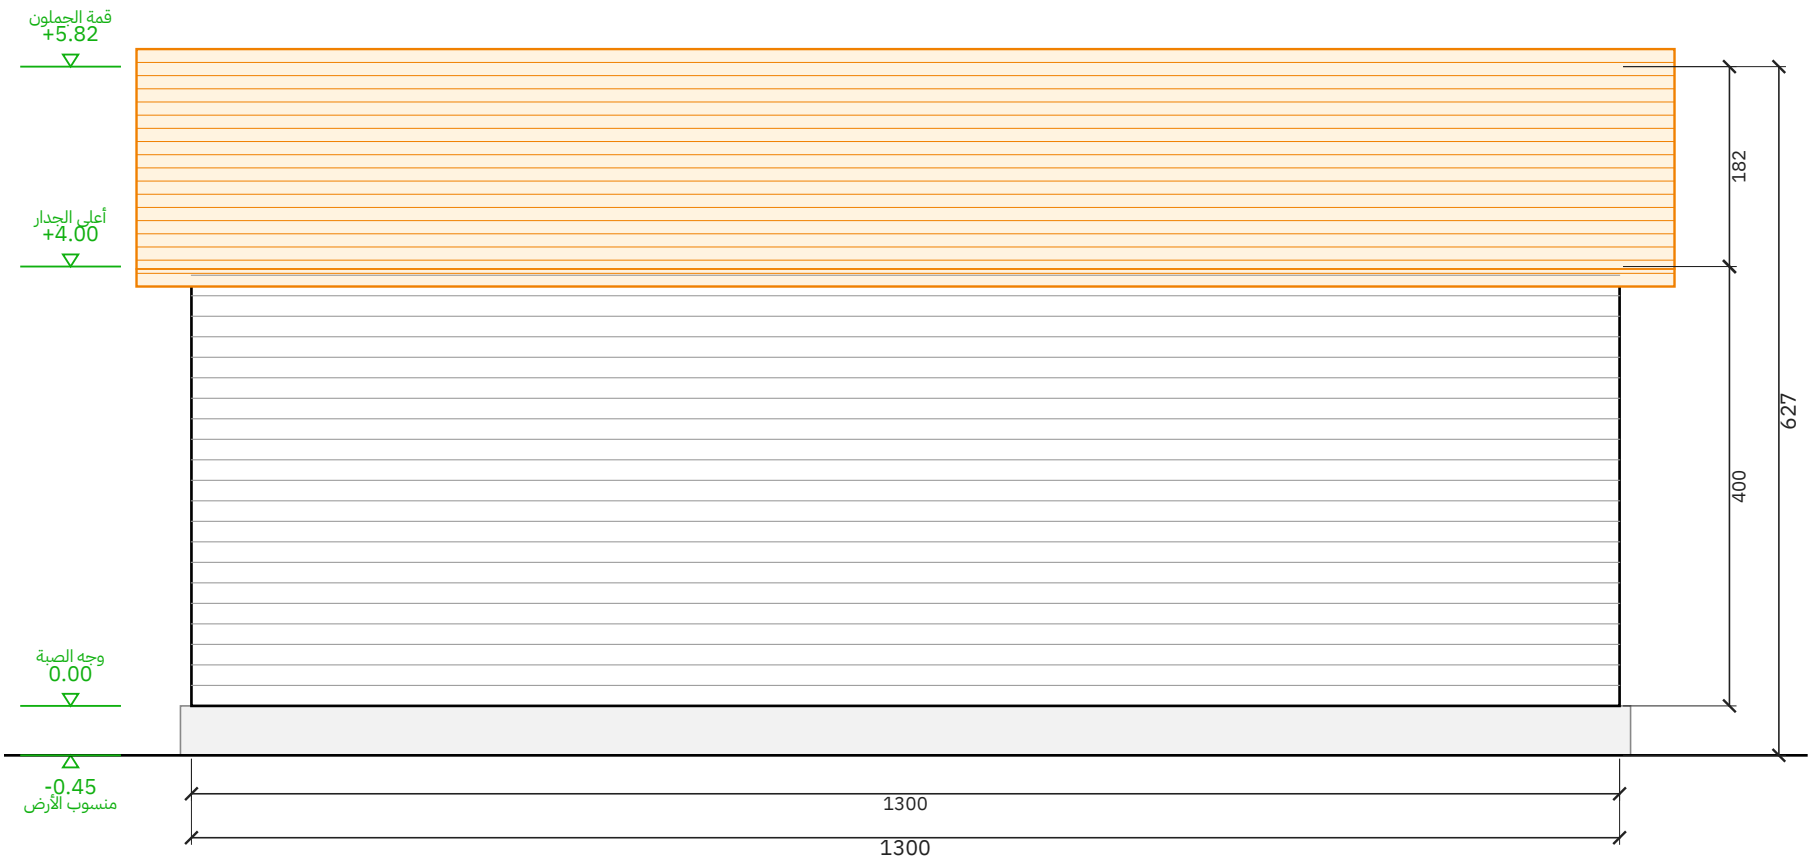


الواجهة اليمنى

مقياس 1:50 | الوحدة: سم


المشروع / العميل	عنوان اللوحة	المقياس	التاريخ	رقم اللوحة
مجلس وجلسة خارجية مغلقة وغرفة نوم 9.00 × 13.00 م – الحوية عميل – الحوية	واجهة المدخل (أعلى المخطط) والواجهة اليمنى	1:50	2026-11-05	A-03 (3/10)

مصنع وتد الأخشاب
Watad Wood Factory

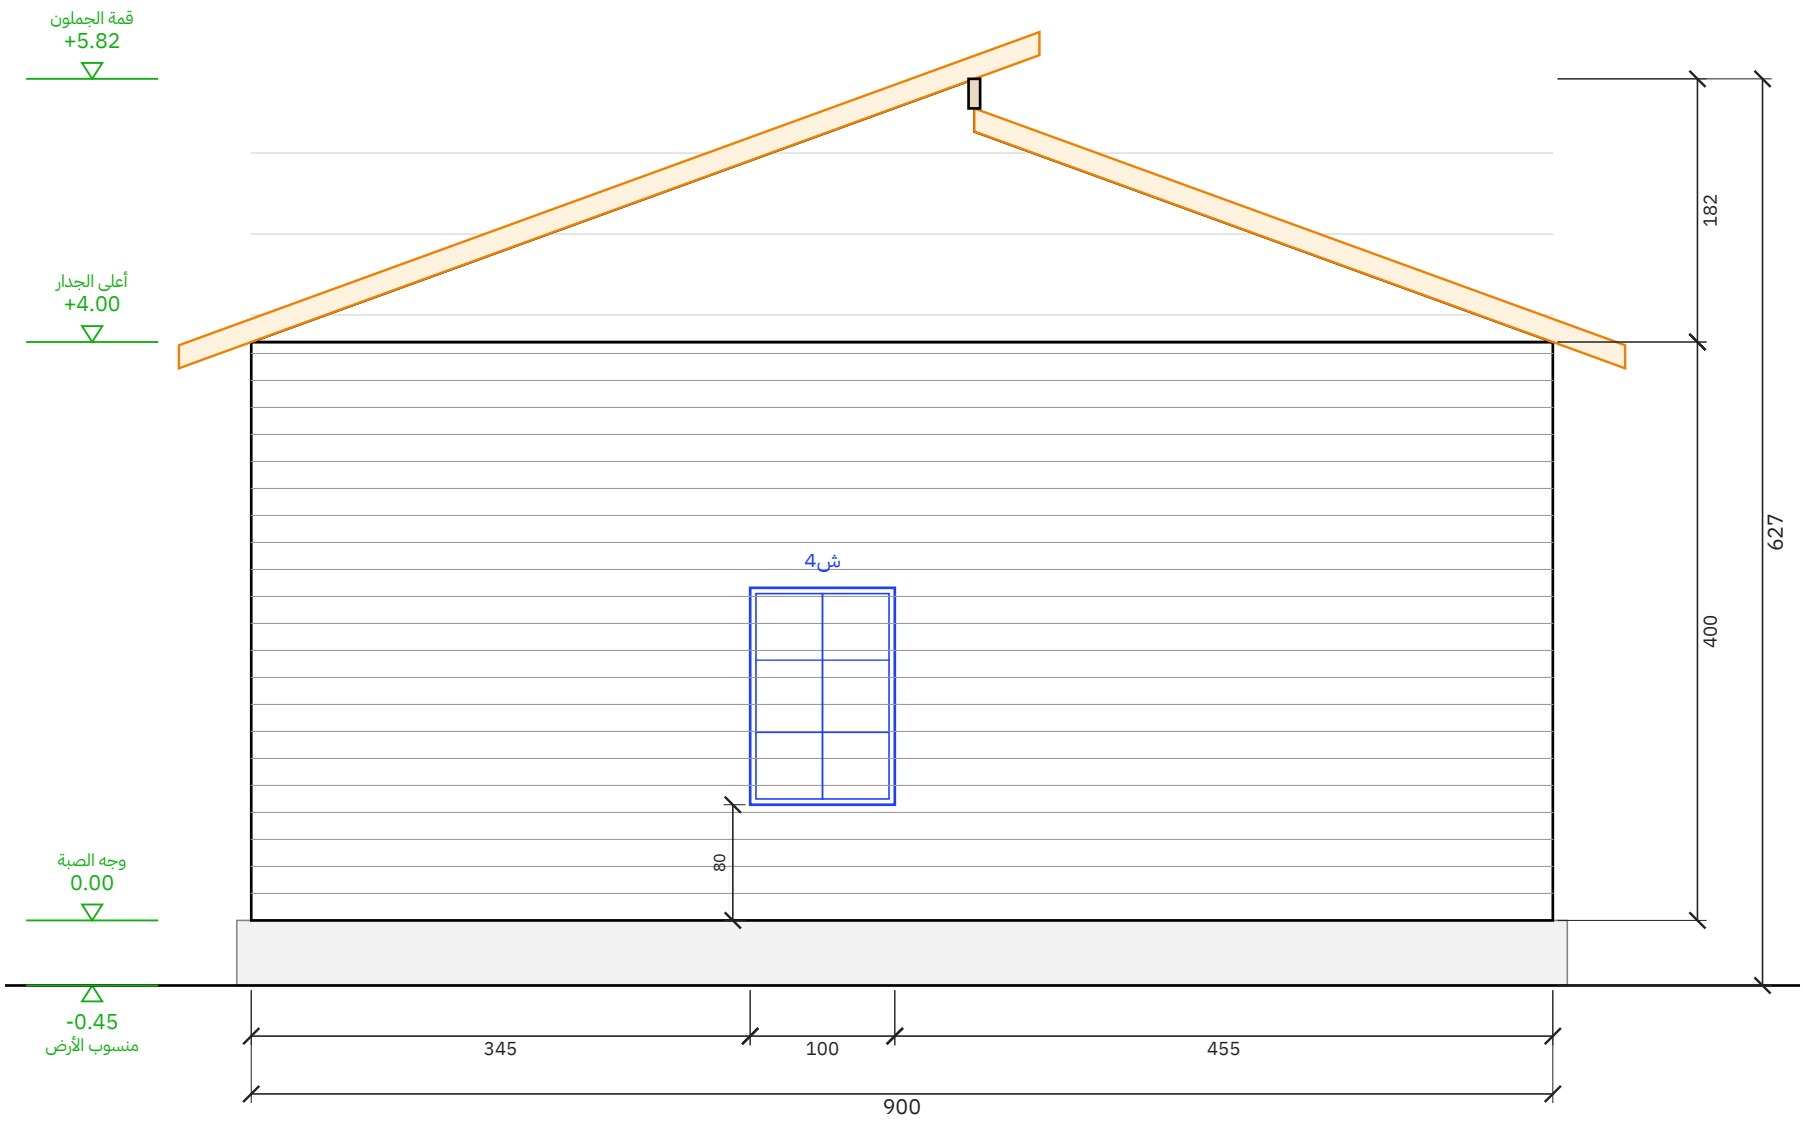

الواجهة السفلية (المجلس)

مقياس 1:50 | الوحدة: سم

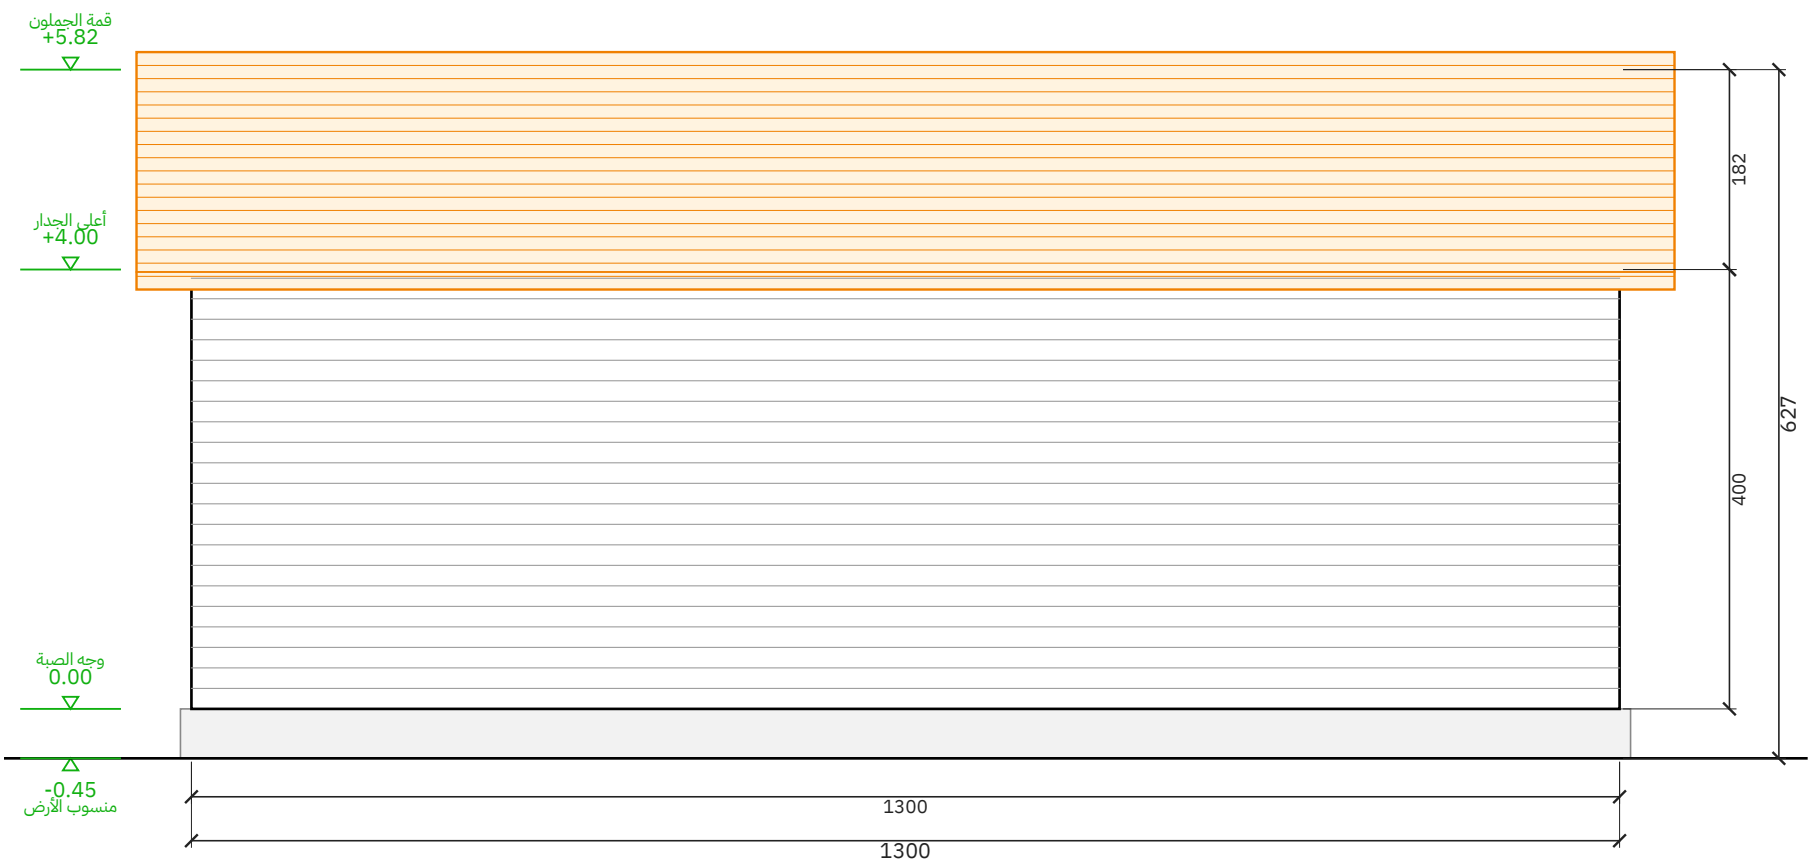

الواجهة اليسرى


مقياس 1:50 | الوحدة: سم

المشروع / العميل	عنوان اللوحة	المقياس	التاريخ	رقم اللوحة
مجلس وجلسة خارجية مغلقة وغرفة نوم 9.00 × 13.00 م – الحوية عميل – الحوية	الواجهة السفلية (المجلس) والواجهة اليسرى	1:50	2026-11-05	A-04 (4/10)

مصنع وتد الأخشاب
Watad Wood Factory


مسقط السقف (جملون متداخل)

رفرف 50 سم من كل جهة | مقياس 1:50

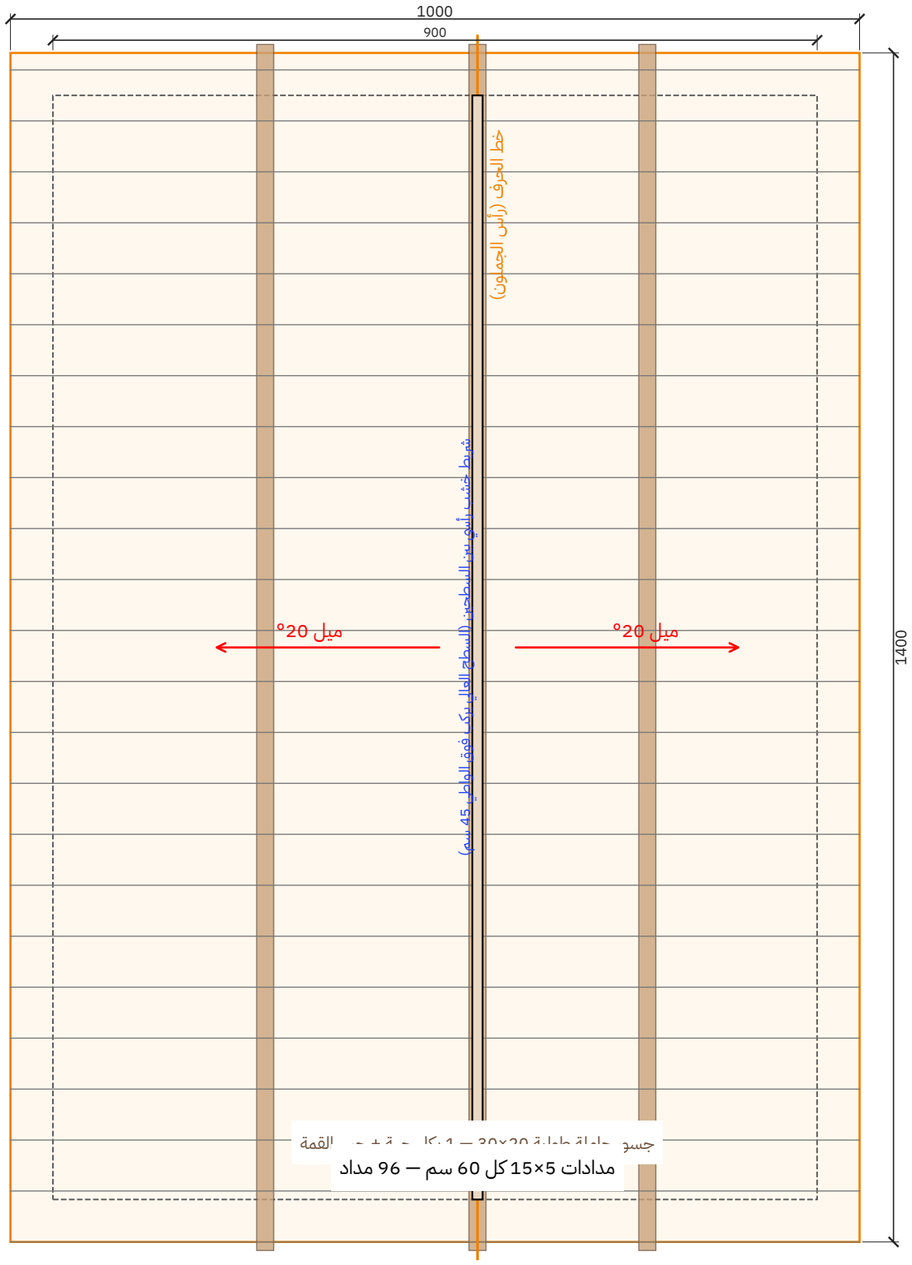


قطاع عرضي أ-أ

مقياس 1:50 | الوحدة: سم

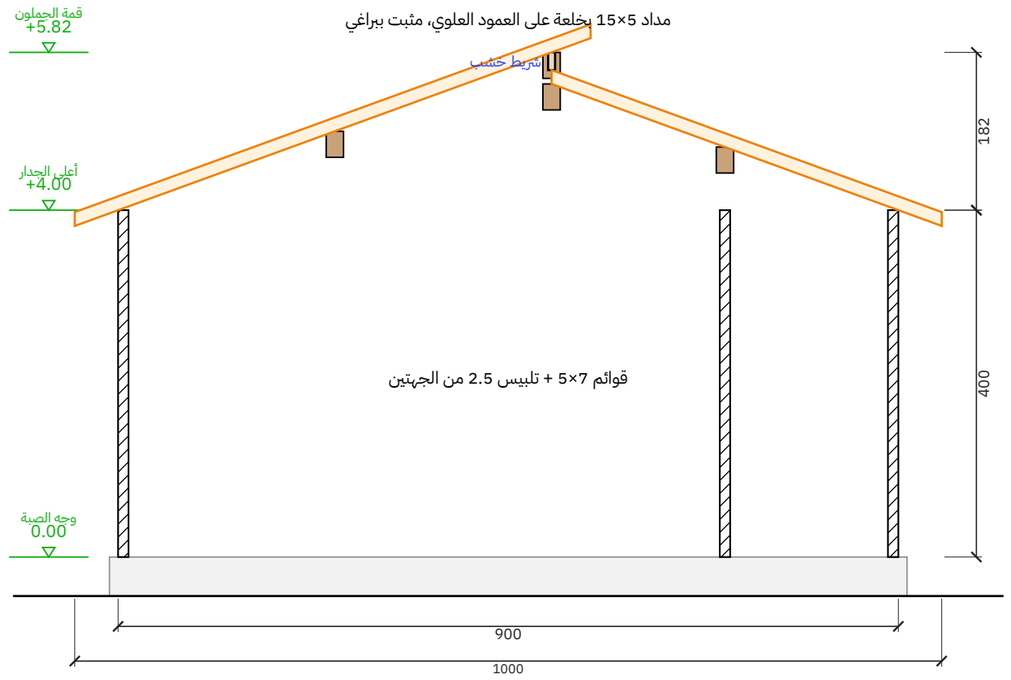

تفصيلة جلوس المداد على العلوي (1:5)

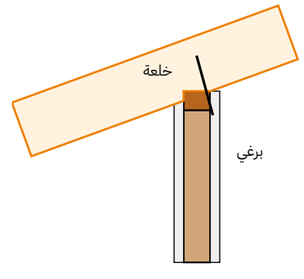

علوي 7×5 على قائم 7×5


المشروع / العميل **مجلس وجلسة خارجية مغلقة وغرفة نوم 9.00 × 13.00 م — الحوية** **عميل — الحوية**	عنوان اللوحة **مسقط السقف والقطاع**	المقياس **1:50**	التاريخ **2026-11-05**	رقم اللوحة **A-05 (5/10)**	**مصنع وتد الأخشاب** Watad Wood Factory

لقطات المنظور الخارجي


المنظور الأمامي




منظور أمامي من اليسار

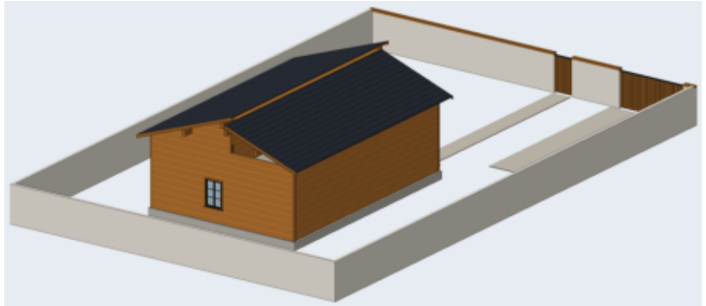


منظور أمامي من اليمين

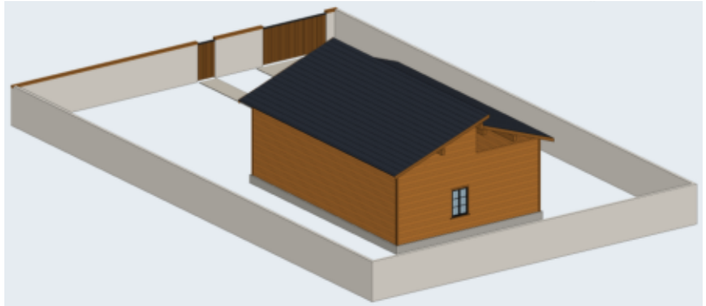


المنظور الخلفي

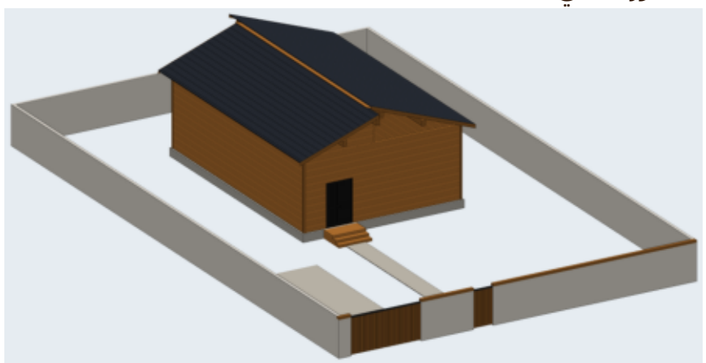

منظور خلفي من اليمين

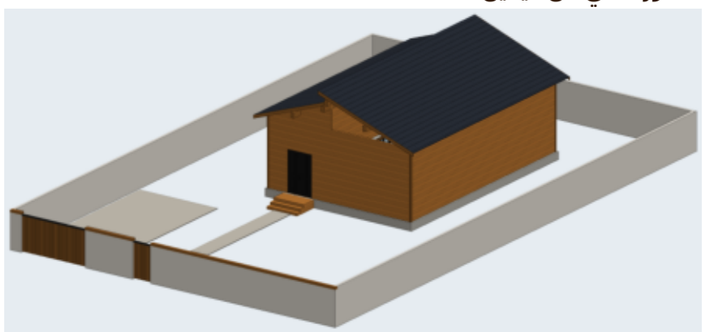

منظر علوي

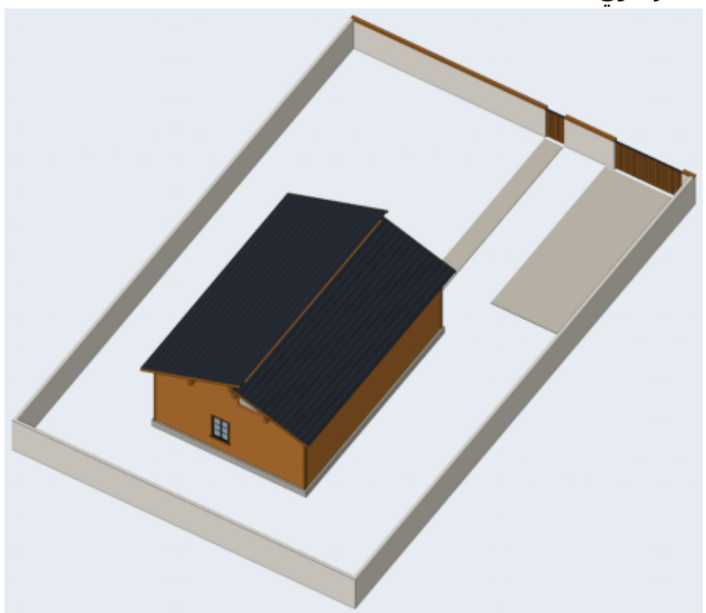


المشروع / العميل	عنوان اللوحة	المقياس	التاريخ	رقم اللوحة
مجلس وجلسة خارجية مغلقة وغرفة نوم 9.00 × 13.00 م – الحوية **عميل – الحوية**	**لقطات المنظور**	–	**2026-11-05**	**A-08 (8/10)**

مصنع وتد الأخشاب
Watad Wood Factory

المقطع العلوي بالفرش

مقطع أفقي على ارتفاع 1.90 م — توزيع الفرش ومسار الحركة

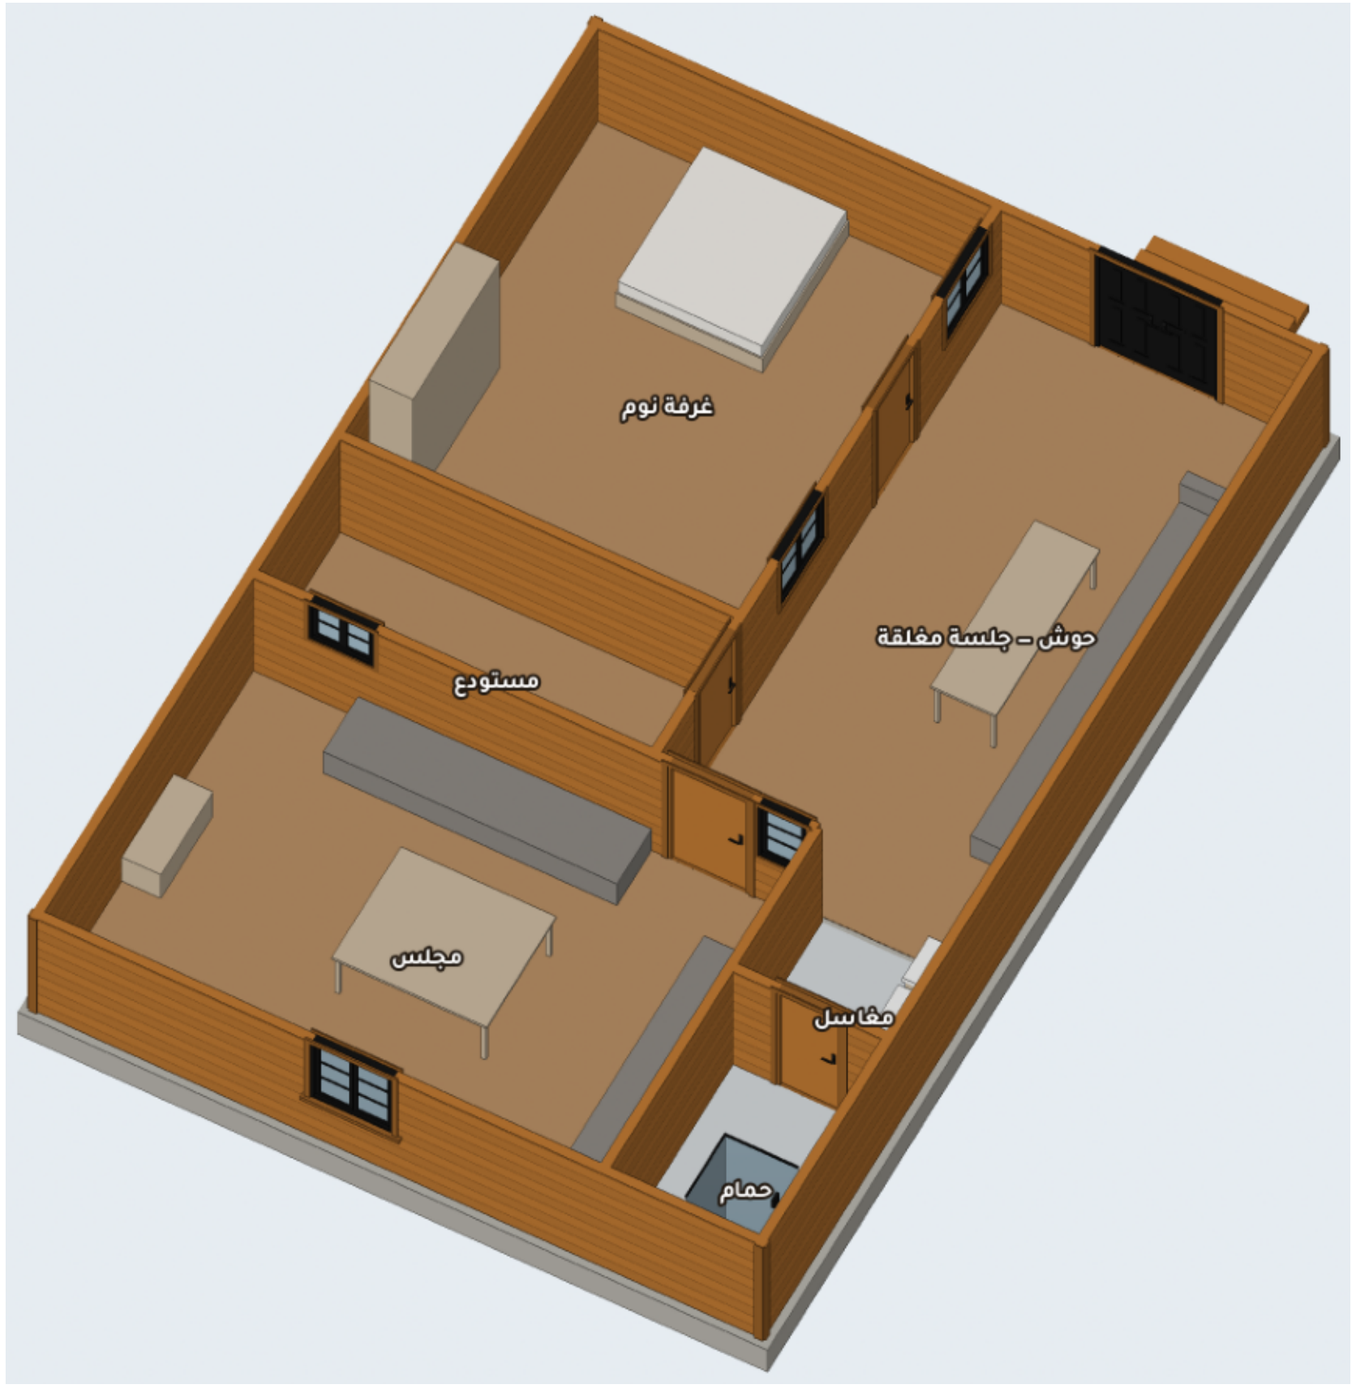

المشروع / العميل	عنوان اللوحة	المقياس	التاريخ	رقم اللوحة
مجلس وجلسة خارجية مغلقة وغرفة نوم 9.00 × 13.00 م — الحوية عميل — الحوية	المقطع العلوي بالفرش	—	2026-11-05	A-09 (9/10)

مصنع وتد الأخشاب
Watad Wood Factory

الواجهة من الحديقة · الخارج – نهاراً



مصنع وتد الأخشاب

الواجهة من الموقف · الخارج – نهاراً



مصنع وتد الأخشاب



مصنع وتد الأخشاب

منظر علوي – الأرض والسور · الخارج – نهاراً




مصنع وتد الأخشاب

جدول مساحات الموقع

البند	المقاس	المساحة (م²)
مساحة الأرض	20.00 × 32.00 م	640.0
مسطح الكوخ (البصمة)	9.00 × 13.00 م	117.0
تراس الكوخ	1.90 × 1.00 م	1.9
موقف سيارة	4.90 × 10.90 م	53.4
ممر	1.10 × 12.90 م	14.2
المسطحات الخضراء (حديقة)	الباقي	453.5

الموقع العام وتنسيق الحديقة (لاندسكيب)

الأرض 20 × 32 م = 640 م² | الأبعاد بالسنتيمتر

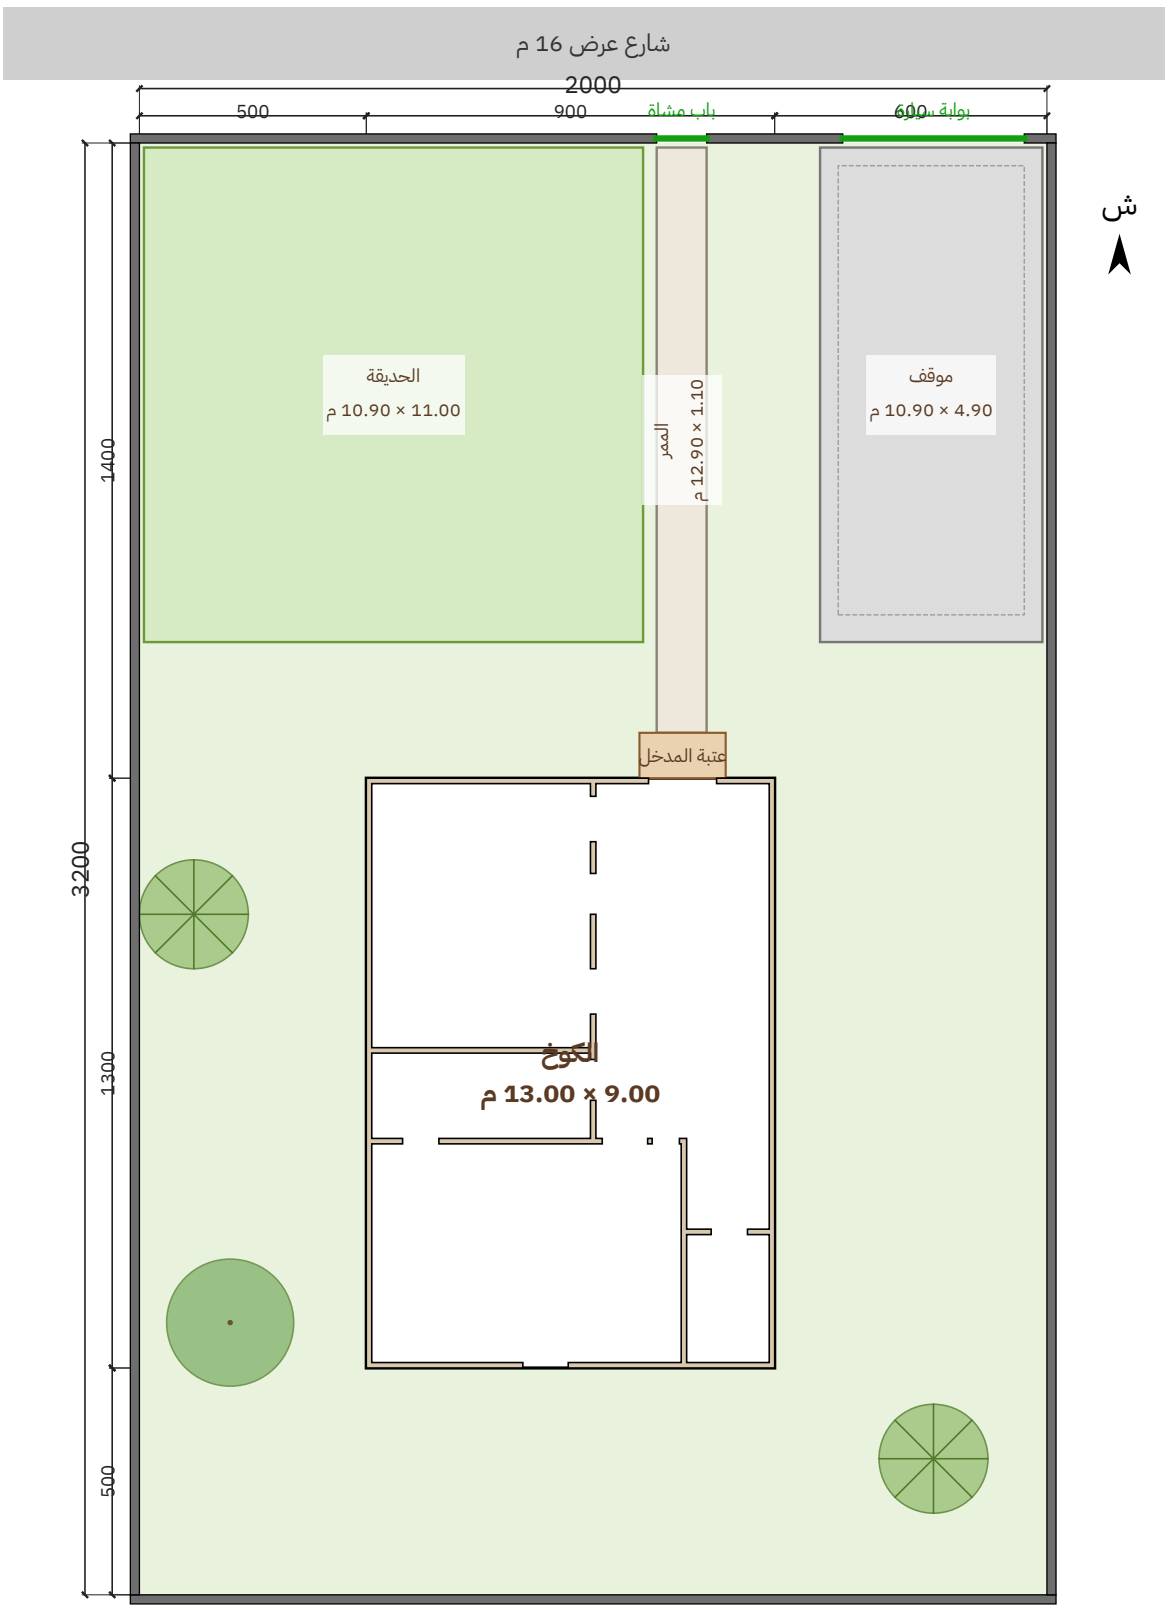

المشروع / العميل	عنوان اللوحة	المقياس	التاريخ	رقم اللوحة
مجلس وجلسة خارجية مغلقة وغرفة نوم 9.00 × 13.00 م – الحوية عميل – الحوية	الموقع العام واللاندسكيب	1:200	2026-11-05	A-01 (1/10)

مصنع وتد الأخشاب
Watad Wood Factory

جدول مقاسات الأبواب والشبابيك


مقاس الفتحة الصافي في الجدار - الوحدة: سم

الرمز	النوع	العرض (سم)	الارتفاع (سم)	ارتفاع الجلسة (سم)	العدد	الموقع
ب1	باب مزدوج	150	240	-	1	واجهة المدخل (أعلى المخطط)
ب2	باب	90	220	-	1	غرفة النوم
ب3	باب	90	220	-	1	المستودع
ب4	باب	100	230	-	1	المجلس
ب5	باب	80	210	-	1	الحمام
ش1	شباك	100	120	100	2	الغرفة على الجلسة 2
ش2	شباك	80	100	120	1	المجلس على المستودع
ش3	شباك	60	150	90	1	المجلس على الحوش
ش4	شباك	100	150	80	1	السفلية (المجلس)

الإجمالي: أبواب 5 - شبابيك 5

المنظور ثلاثي الأبعاد والمواد

النمط: برتقالي محمر + قرميد فحمي + دربزين X — رندر واقعي بخامات حقيقية

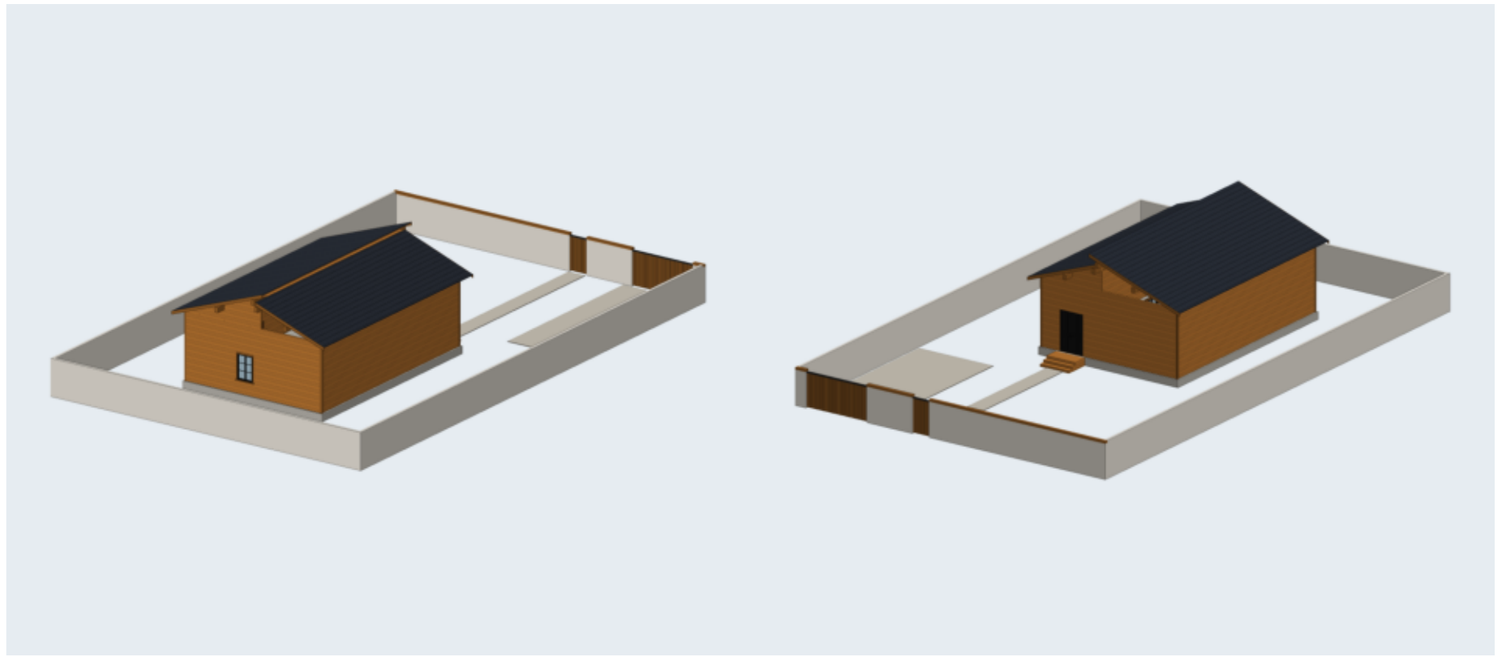

جدول المواد والألوان

الخشب / الصبغة

صبغة عسلي / سيدر

القرميد

قرميد فحمي / أسود مزرق

الزجاج

زجاج شفاف

إطارات الشبابيك والأبواب

إطار ألمنيوم أسود

الكنار والزوايا

نفس الصبغة أغمق درجة


الصبة

خرسانة 45 سم


الدربزين: تقاطع X (صورة 5)

تقسيم الشبابيك: شبكة | الباب الرئيسي: خشب مصمت

أنواع الدربزين المعتمدة (من مشاريع المصنع)

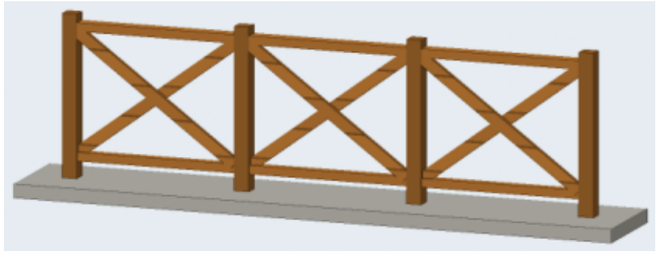

تقاطع X (صورة 5)

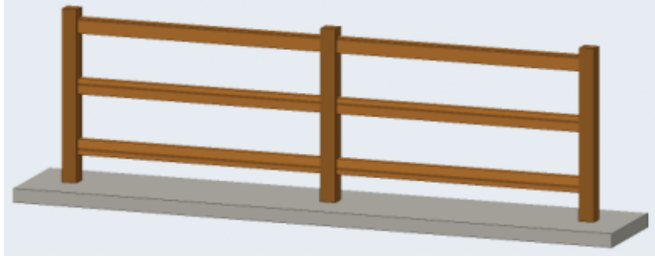

3 مرابيع أفقية (صورة 2)



قوائم رأسية متقاربة (صورة 1)

المشروع / العميل	عنوان اللوحة	المقياس	التاريخ	رقم اللوحة
مجلس وجلسة خارجية مغلقة وغرفة نوم 9.00 × 13.00 م — الحوية **عميل — الحوية**	**المنظور والمواد**	**—**	**2026-11-05**	**A-10 (10/10)**

مصنع وتد الأخشاب
Watad Wood Factory

جدول المساحات وبيانات المشروع

بيانات المشروع

البند	البيان
المشروع	مجلس وجلسة خارجية مغلقة وغرفة نوم 9.00 × 13.00 م — الحوية
العميل	عميل — الحوية
الموقع	الحوية
الاستخدام	مجلس ضيافة + جلسة مغلقة + غرفة نوم
التاريخ	2026-11-05
نظام البناء	هيكل خشب 7×5 + تلبيس 2.5 سم من الجهتين
السقف	جملون 20° — قرميد معدني

جدول المساحات

م	الفراغ	الأبعاد (م)	المساحة (م2)
1	غرفة نوم	4.82 × 5.82	28.05
2	مستودع	4.82 × 1.88	9.06
3	حوش — جلسة مغلقة	3.82 × 7.82	29.87
4	مجلس	6.82 × 4.82	32.87
5	مغاسل	1.82 × 1.94	3.53
6	حمام	1.82 × 2.82	5.13
	المساحة الصافية الداخلية		**108.52**
	المساحة الإجمالية المبنية	**9.00 × 13.00**	**117.00**