
المنظور ثلاثي الأبعاد والمواد

النمط: برتقالي محمر + قرميد فحمي + دربزين X — رندر واقعي بخامات حقيقية

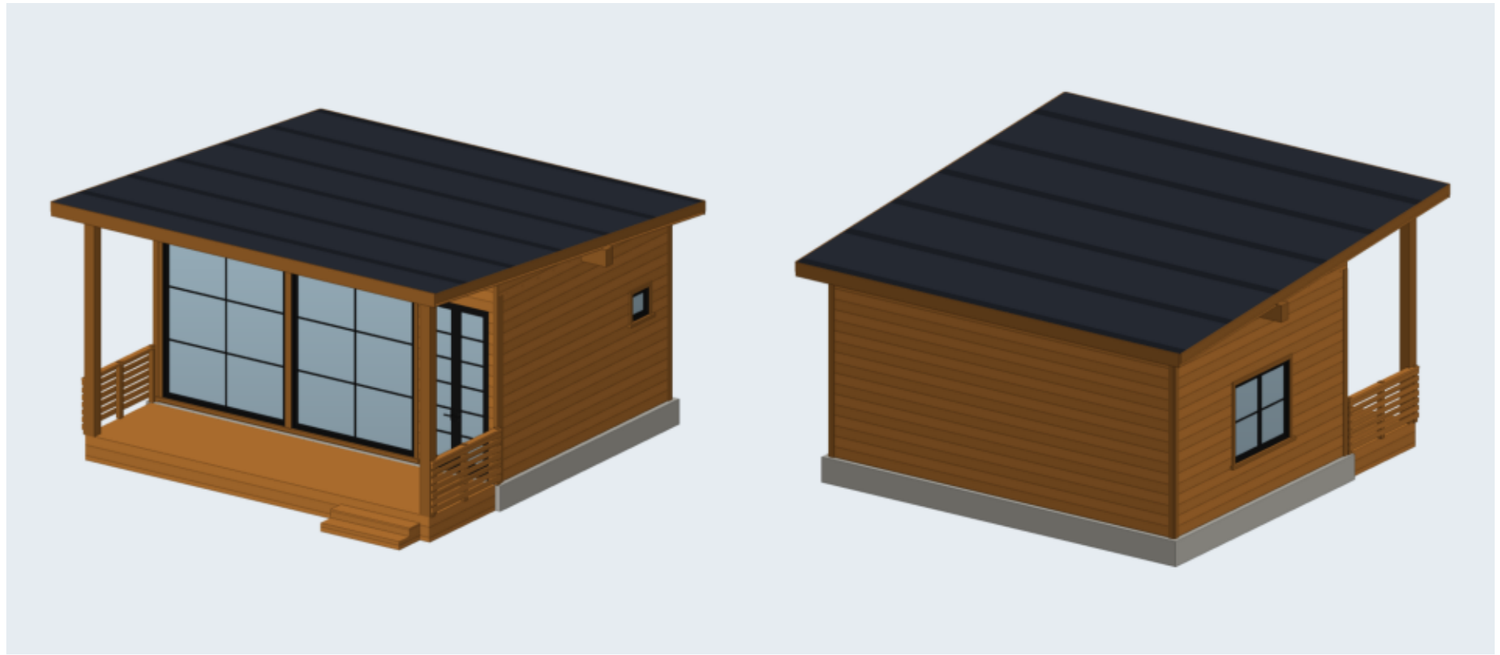

جدول المواد والألوان

الخشب / الصبغة

صبغة عسلي / سيدر

السقف (صاج معدني)

صاج فحمي / أسود مزرق

الزجاج

زجاج شفاف

إطارات الشبابيك والأبواب

إطار ألمنيوم أسود

الكنار والزوايا

نفس الصبغة أغمق درجة


الصبة

خرسانة 45 سم


الدربزين: ألواح أفقية متقاربة (عصري)

تقسيم الشبابيك: شبكة | الباب الرئيسي: زجاج بتقسيمات (فرنسي)

أنواع الدربزين المعتمدة (من مشاريع المصنع)

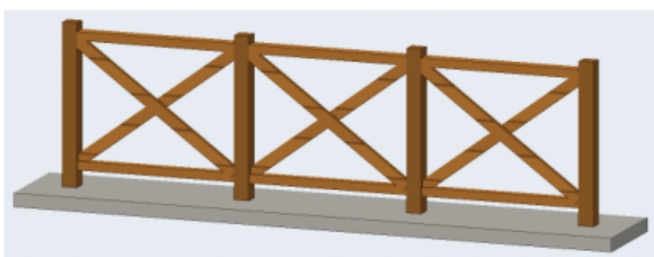

تقاطع X (صورة 5)

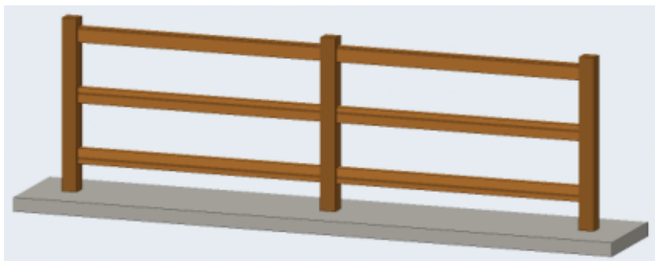

3 مرابيع أفقية (صورة 2)




قوائم رأسية متقاربة (صورة 1)


المشروع / العميل	عنوان اللوحة	المقياس	التاريخ	رقم اللوحة
مصنع وتد الأخشاب Watad Wood Factory **مجلس خشب 7.00 × 5.00 م — سقف مائل ممتد على جلسة خارجية** **عميل — مجلس 7×5**	**المنظور والمواد**	**1:50**	**2026-10-29**	**W-01 (1/12)**

المسقط الأفقي مع الفرش

الأبعاد بالسنتيمتر - الجدران: قوائم 7×5 + تلبيس 2.5 من الجهتين (12 سم)

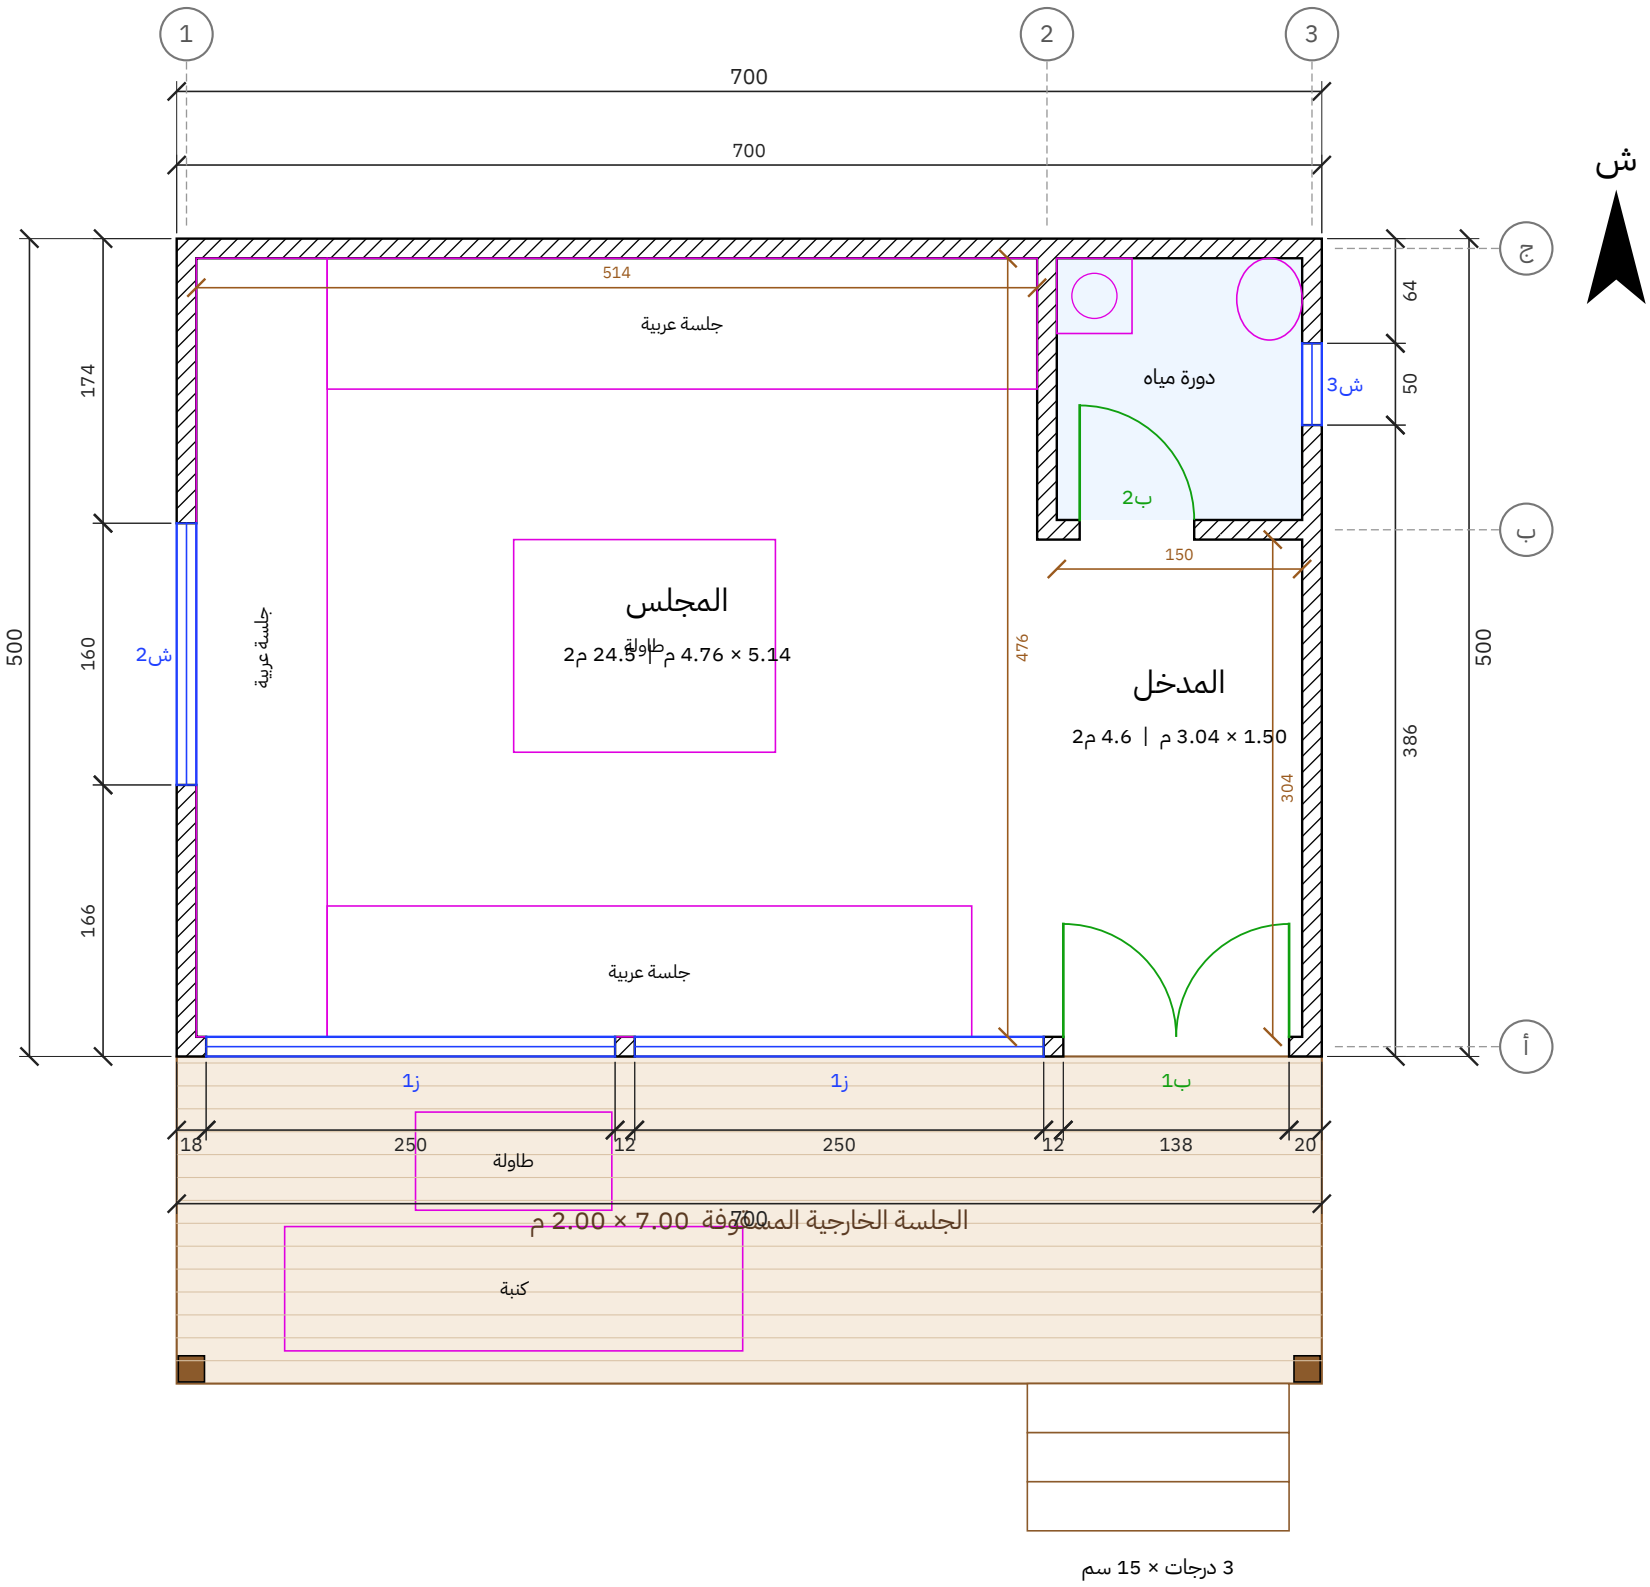


مصنع وتد الأخشاب Watad Wood Factory	المشروع / العميل مجلس خشب 7.00 × 5.00 م – سقف مائل ممتد على جلسة خارجية عميل – مجلس 7×5	عنوان اللوحة المسقط الأفقي	المقياس 1:50	التاريخ 2026-10-29	رقم اللوحة W-02 (2/12)

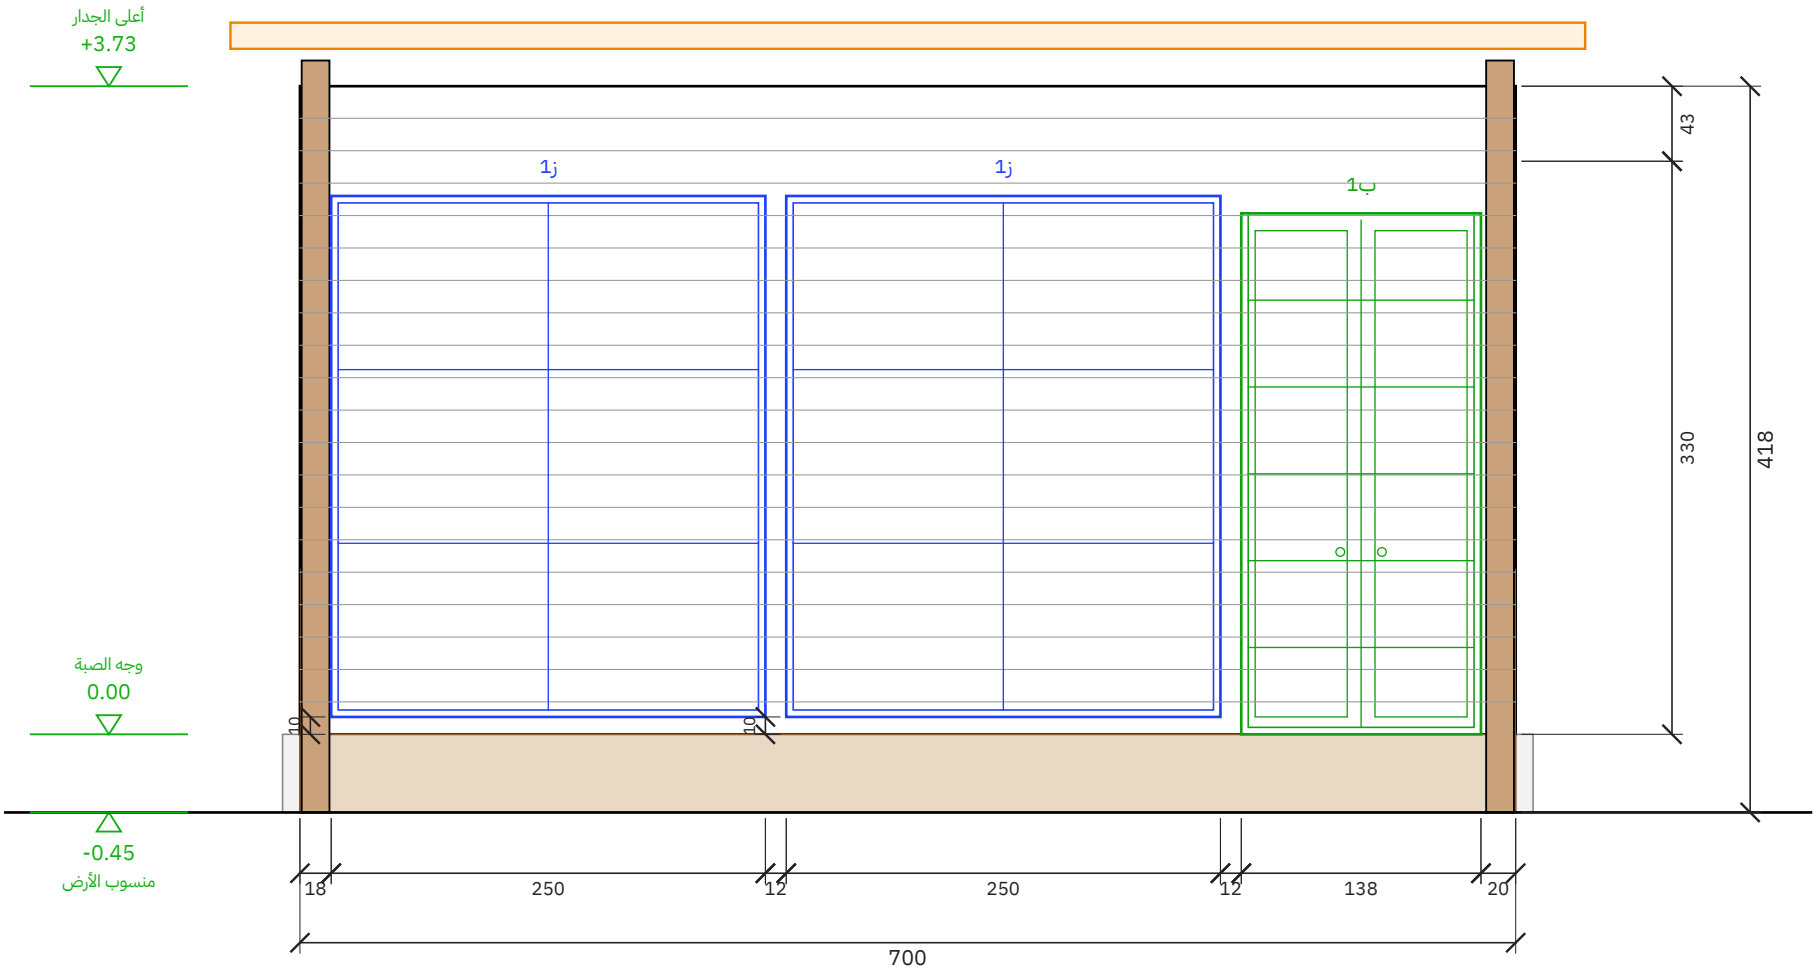

الواجهة الأمامية (زجاج كامل على الحوش)

مقياس 1:50 | الوحدة: سم

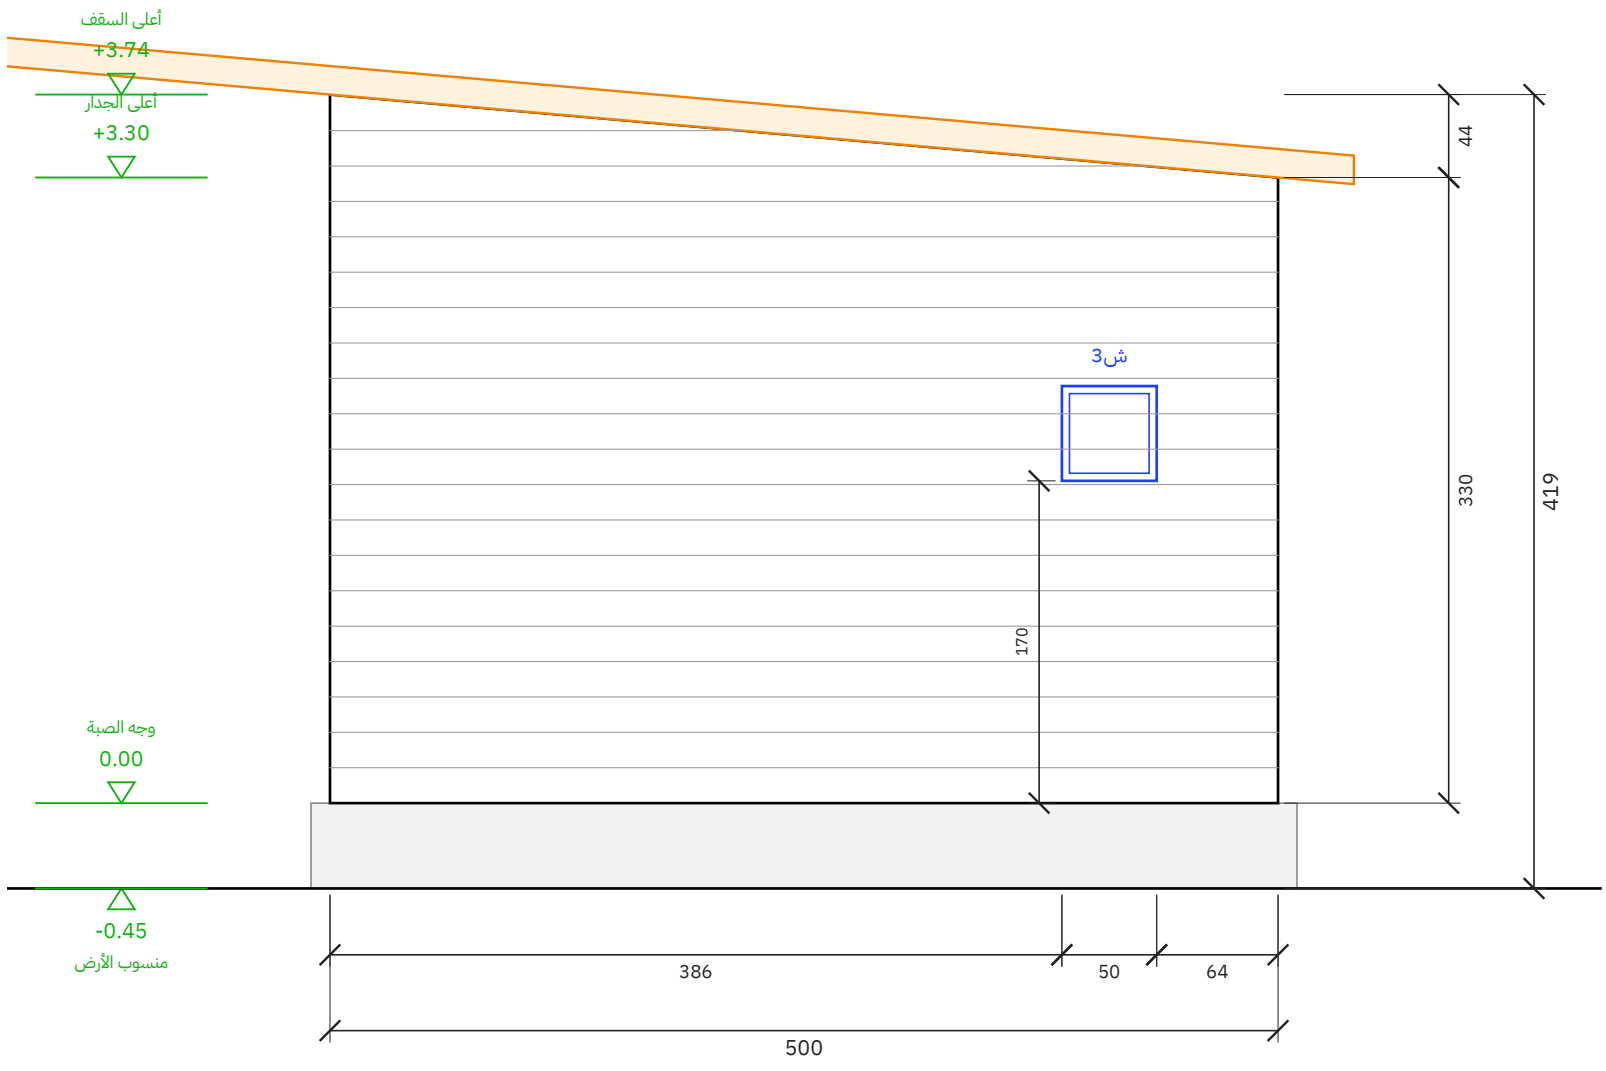


الواجهة الشرقية

مقياس 1:50 | الوحدة: سم


المشروع / العميل	عنوان اللوحة	المقياس	التاريخ	رقم اللوحة
مجلس خشب 7.00 × 5.00 م — سقف مائل ممتد على جلسة خارجية عميل — مجلس 7×5	الواجهة الأمامية (زجاج كامل على الحوش) والواجهة الشرقية	1:50	2026-10-29	W-03 (3/12)

مصنع وتد الأخشاب
Watad Wood Factory

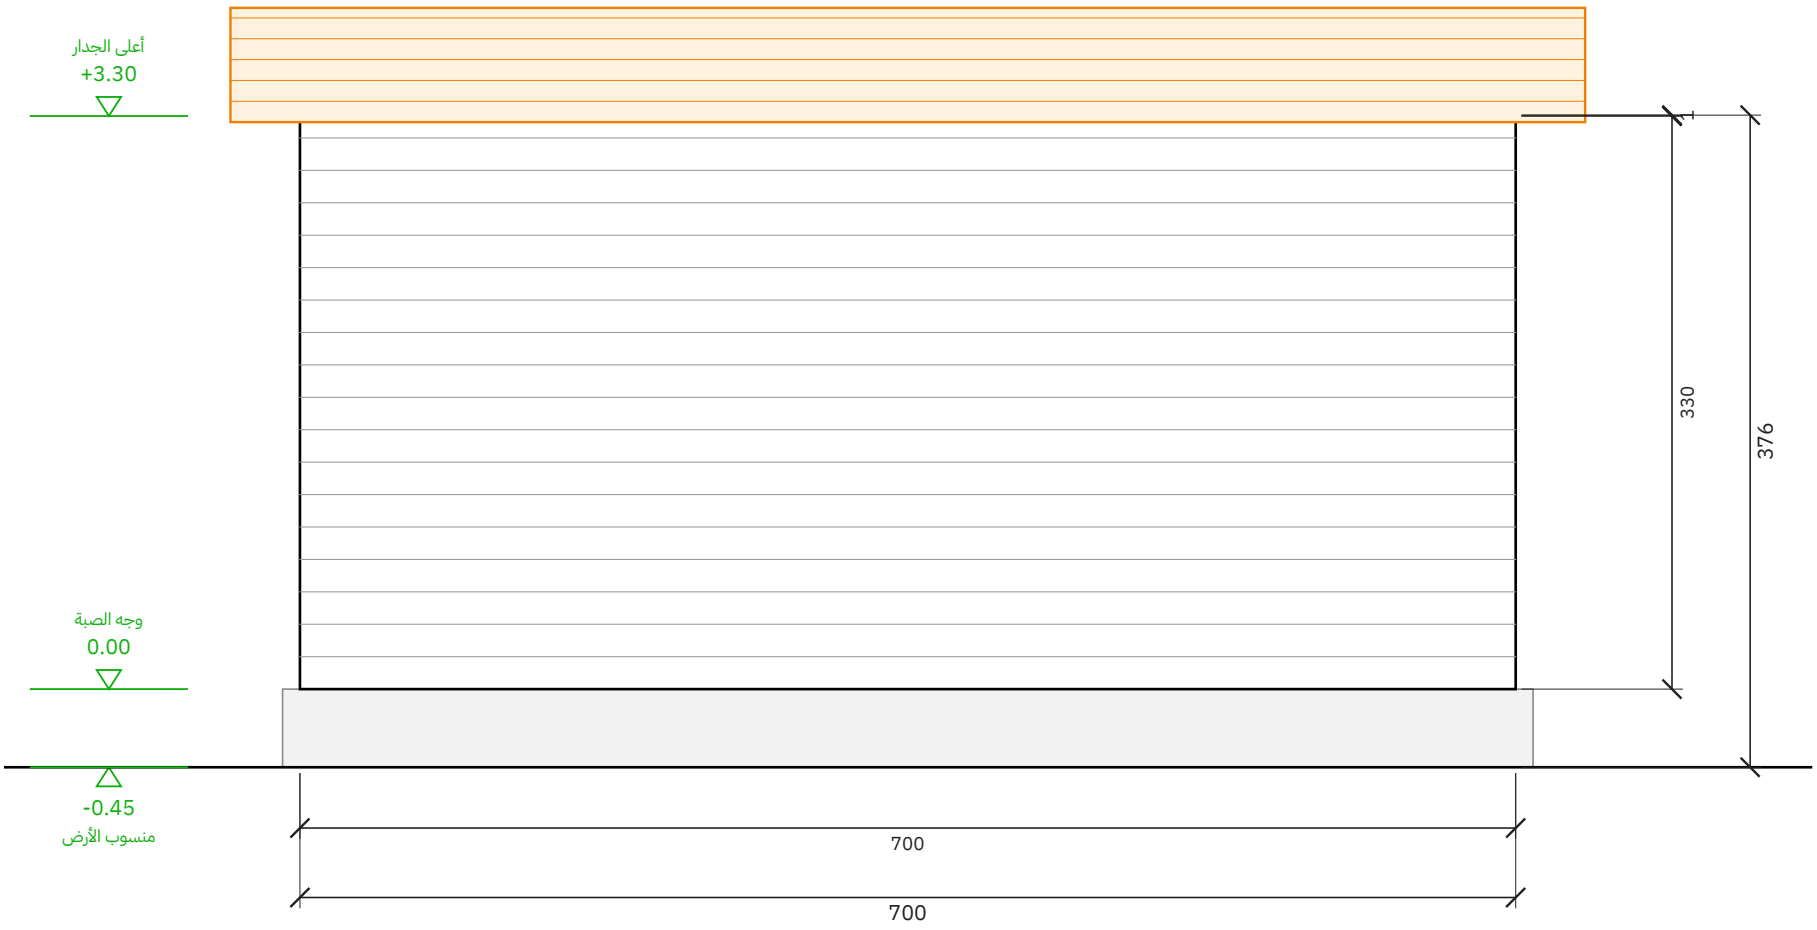

الواجهة الخلفية

مقياس 1:50 | الوحدة: سم

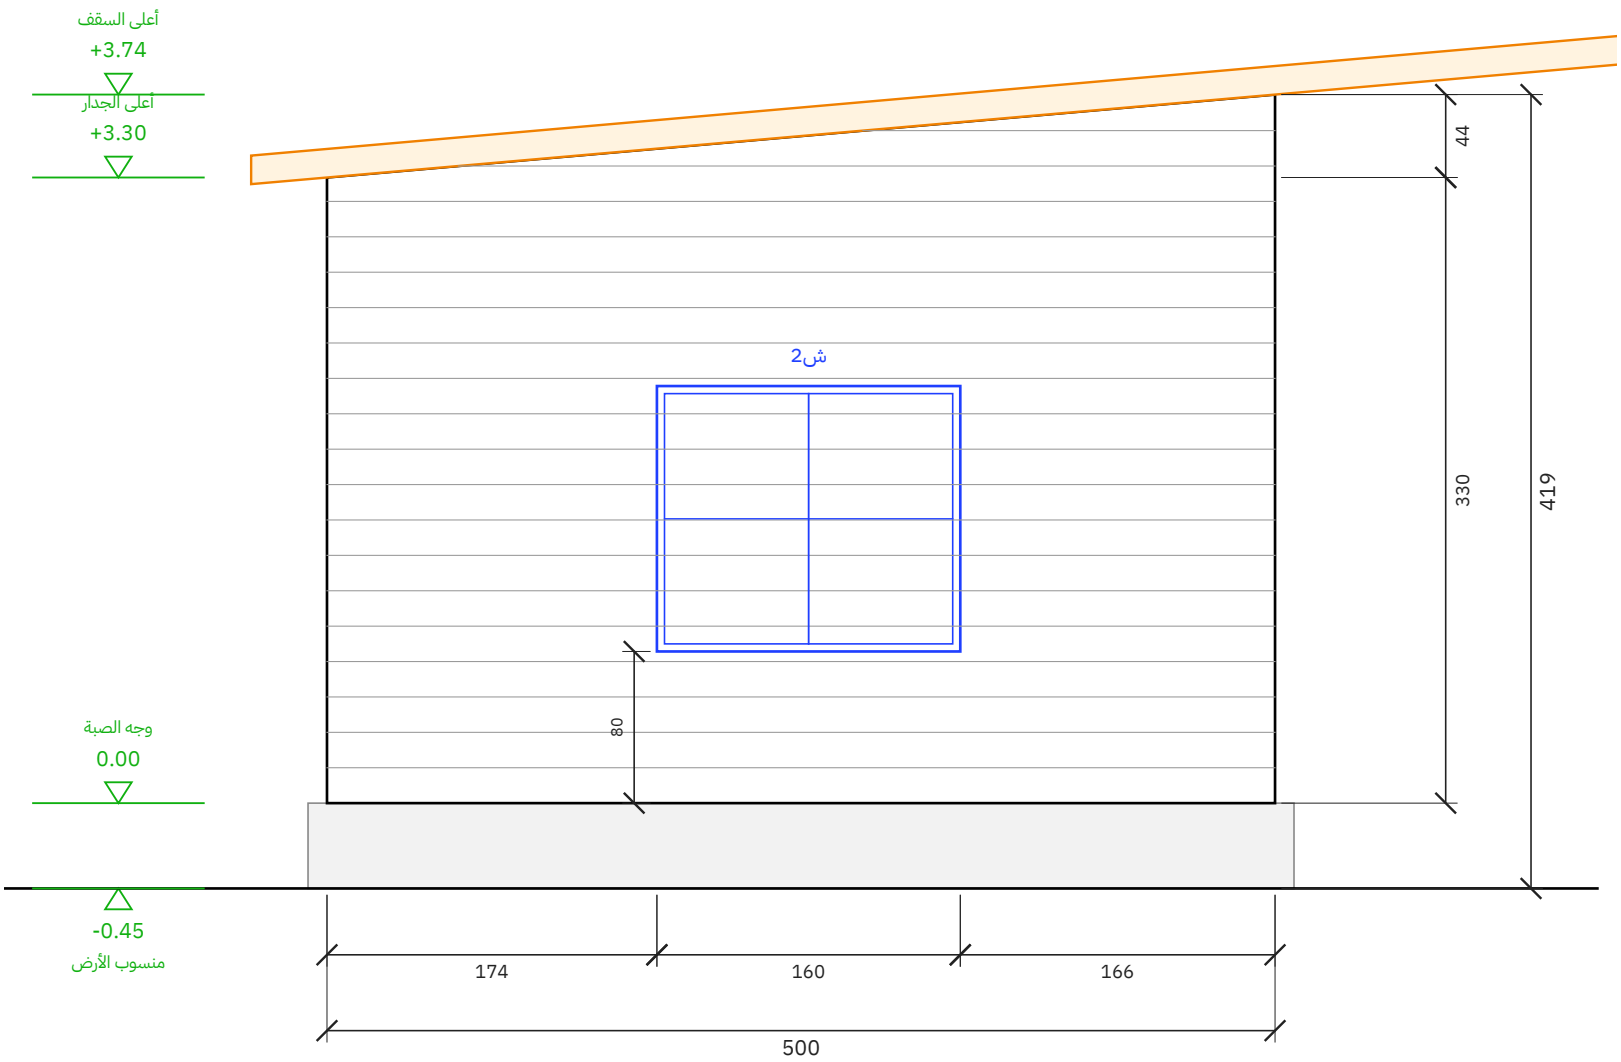

الواجهة الغربية


مقياس 1:50 | الوحدة: سم

المشروع / العميل	عنوان اللوحة	المقياس	التاريخ	رقم اللوحة
مجلس خشب 7.00 × 5.00 م — سقف مائل ممتد على جلسة خارجية عميل — مجلس 7×5	الواجهة الخلفية والواجهة الغربية	1:50	2026-10-29	W-04 (4/12)

مصنع وتد الأخشاب
Watad Wood Factory


مسقط السقف (مائل باتجاه واحد)

رفرف 40 سم من كل جهة | مقياس 1:50

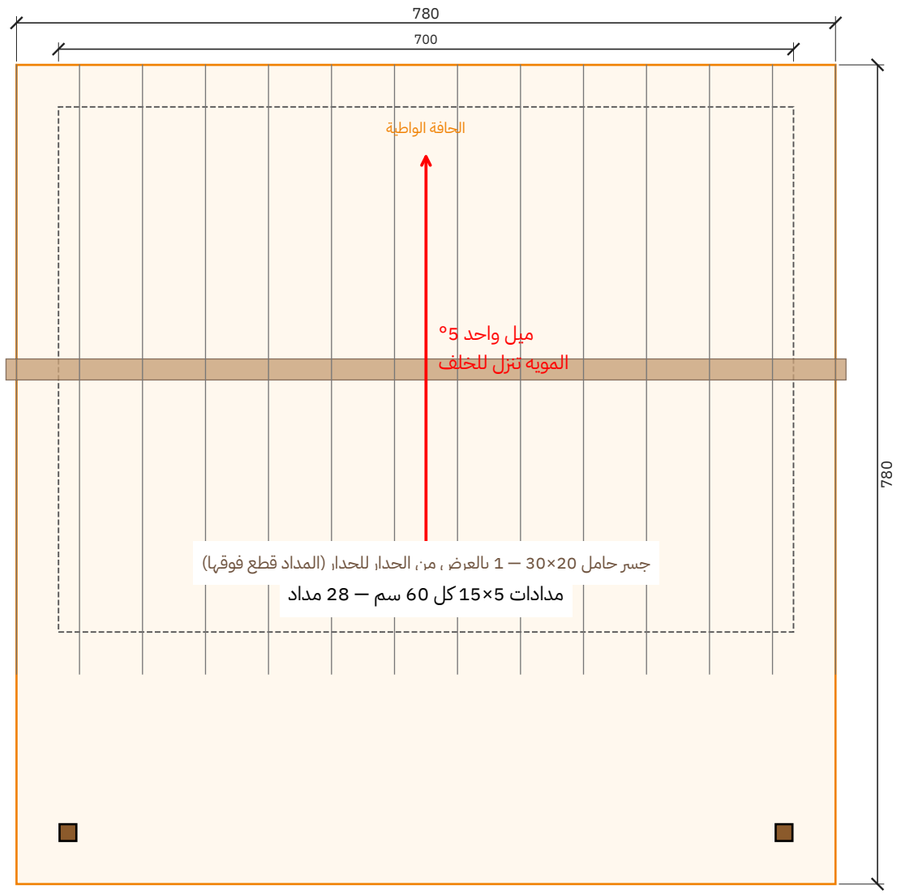


قطاع عرضي أ-أ

مقياس 1:50 | الوحدة: سم

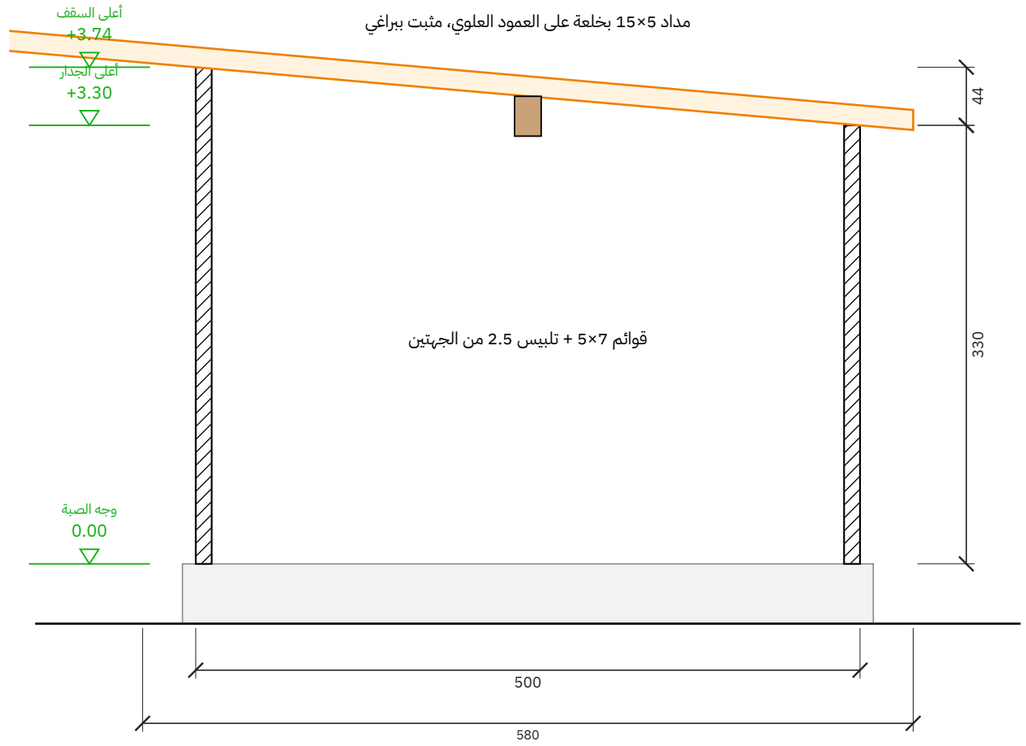

تفصيلة جلوس المداد على العلوي (1:5)

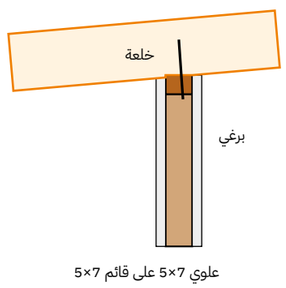

المشروع / العميل **مجلس خشب 7.00 × 5.00 م — سقف مائل ممتد على جلسة خارجية** **عميل — مجلس 7×5**	عنوان اللوحة **مسقط السقف والقطاع**	المقياس **1:50**	التاريخ **2026-10-29**	رقم اللوحة **W-05 (5/12)**

مصنع وتد الأخشاب
Watad Wood Factory

جدول مقاسات الأبواب والشبابيك

مقاس الفتحة الصافي في الجدار - الوحدة: سم

الرمز	النوع	العرض (سم)	الارتفاع (سم)	ارتفاع الجلسة (سم)	العدد	الموقع
ب1	باب مزدوج	138	300	-	1	الأمامية (زجاج كامل على الحوش)
ب2	باب	70	210	-	1	دورة المياه
ز1	شباك	250	300	10	2	الأمامية (زجاج كامل على الحوش) 2
ش2	شباك	160	140	80	1	الغربية
ش3	شباك	50	50	170	1	الشرقية

الإجمالي: أبواب 2 - شبابيك 4

جدول المساحات وبيانات المشروع


بيانات المشروع

البند	البيان
المشروع	مجلس خشب 7.00 × 5.00 م — سقف مائل ممتد على جلسة خارجية
العميل	عميل — مجلس 7×5
الموقع	—
الاستخدام	مجلس ضيافة
التاريخ	2026-10-29
نظام البناء	هيكل خشب 7×5 + تلبيس 2.5 سم من الجهتين
السقف	مائل باتجاه واحد 5° — صاج معدني + عزل مائي


جدول المساحات

م	الفراغ	الأبعاد (م)	المساحة (م2)
1	المجلس	5.14 × 4.76	24.47
2	المدخل	1.50 × 3.04	4.56
3	دورة مياه	1.50 × 1.60	2.40
	المساحة الصافية الداخلية		**31.43**
	الجلسة الخارجية المسقوفة	**7.00 × 2.00**	**14.00**
	المساحة الإجمالية المبنية	**7.00 × 5.00**	**35.00**
	المساحة الكلية (المبنية + التراس)		**49.00**

تأطير جدار جنوب — الطول 688 سم، الارتفاع 374 سم

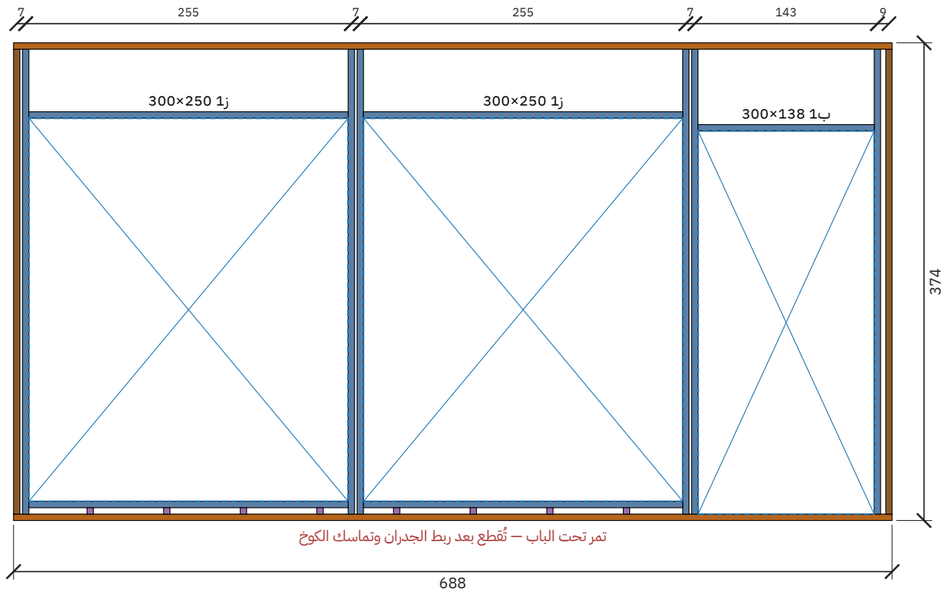

تأطير جدار شرق — الطول 488 سم، الارتفاع 330 سم

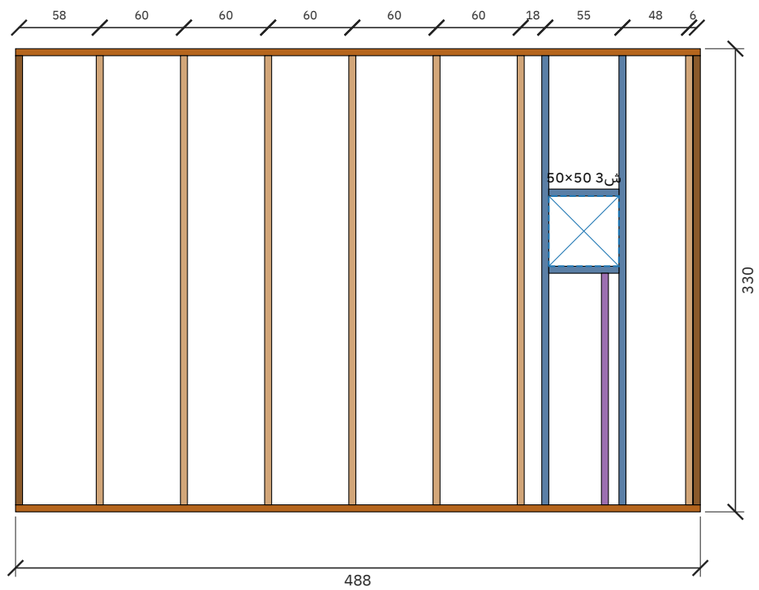


قاعدة سفلية · علوي · عمود · عمود زاوية · جنب فتحة · رأس فتحة · جلسة شباك · عمود قصير


المشروع / العميل	عنوان اللوحة	المقياس	التاريخ	رقم اللوحة
مجلس خشب 7.00 × 5.00 م – سقف مائل ممتد على جلسة خارجية عميل – مجلس 7×5	لوحات التأطير (للورشة)	–	2026-10-29	W-08 (8/12)

مصنع وتد الأخشاب
Watad Wood Factory

تأطير جدار شمال — الطول 688 سم، الارتفاع 330 سم

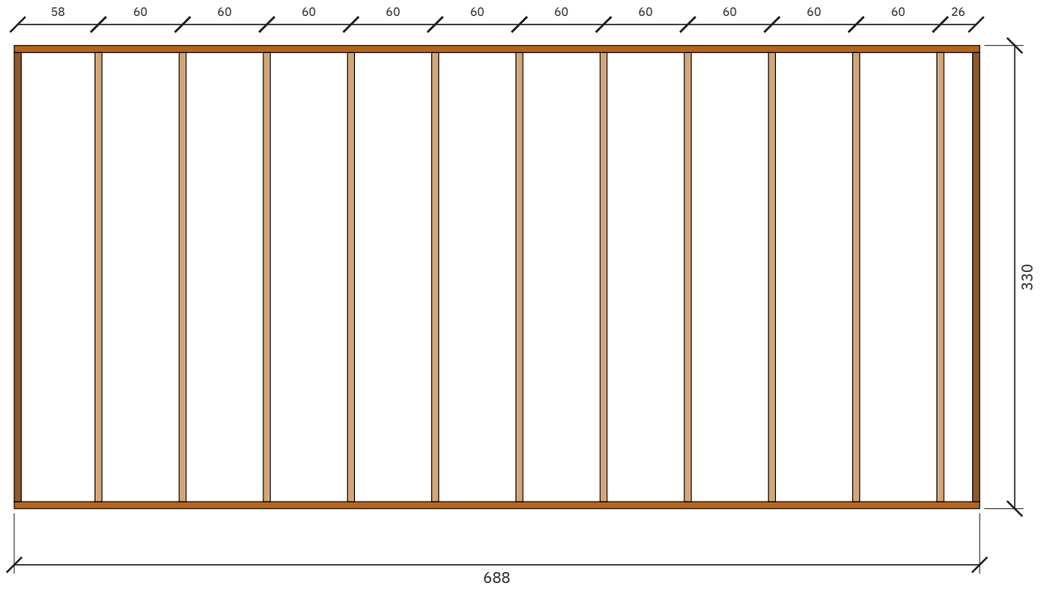

تأطير جدار غرب — الطول 488 سم، الارتفاع 330 سم

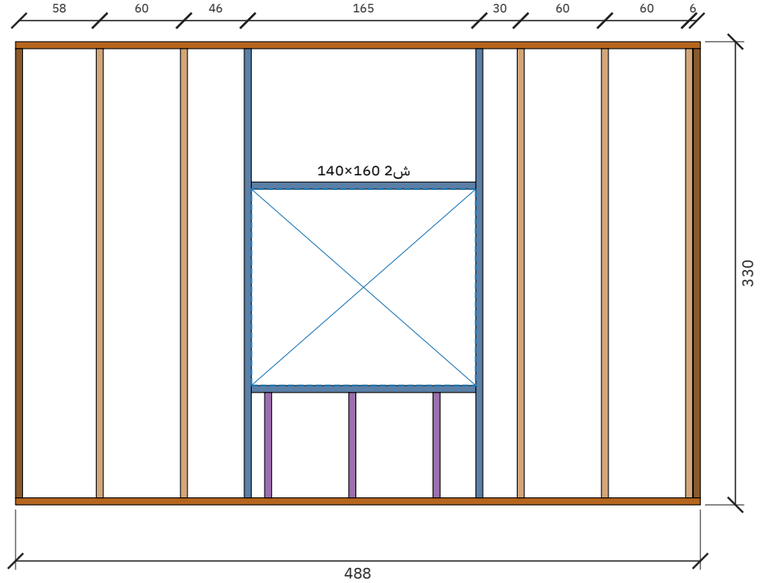


قاعدة سفلية | علوي | عمود | عمود زاوية | جنب فتحة | رأس فتحة | جلسة شباك | عمود قصير


المشروع / العميل	عنوان اللوحة	المقياس	التاريخ	رقم اللوحة
مجلس خشب 7.00 × 5.00 م — سقف مائل ممتد على جلسة خارجية عميل — مجلس 7×5	لوحات التأطير (للورشة)	—	2026-10-29	W-09 (9/12)

مصنع وتد الأخشاب
Watad Wood Factory

تأطير جدار جدار دورة المياه — الطول 162 سم، الارتفاع 330 سم (داخلي)

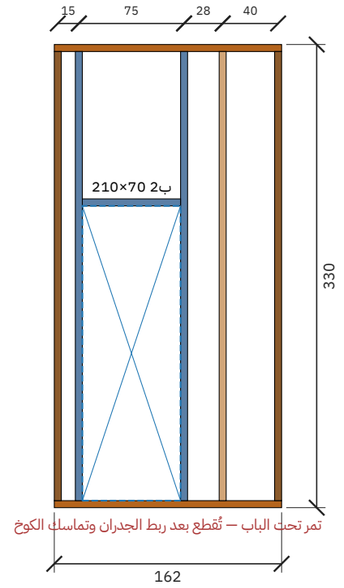

تأطير جدار جدار دورة المياه الغربي — الطول 172 سم، الارتفاع 330 سم (داخلي)

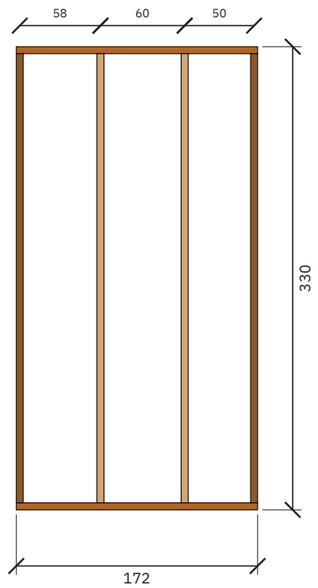

قاعدة سفلية | علوي | عمود | عمود زاوية | جنب فتحة | رأس فتحة | جلسة شباك | عمود قصير

المشروع / العميل	عنوان اللوحة	المقياس	التاريخ	رقم اللوحة
مجلس خشب 7.00 × 5.00 م — سقف مائل ممتد على جلسة خارجية عميل — مجلس 7×5	لوحات التأطير (للورشة)	—	2026-10-29	W-10 (10/12)

مصنع وتد الأخشاب
Watad Wood Factory

جدول الكميات وخطة تقطيع الطبليات

البند	القيمة
الارتفاع المطلوب / المعتمد	330 / 330 سم
السقف	مائل باتجاه واحد 5° — أعلى نقطة 374 سم من وجه الصبة
المدادات 5×15	28 مداد (14 خط × قطعتين موصولة فوق الجسر الحامل بتراكب 60 سم) × حتى 321 سم — من طبلية 480
طبليات الطريقة الأولى (مداد + عمود)	28 طبلية × 480 سم
طبليات الطريقة الثانية (3 أعمدة)	17 طبلية × 320 سم
إجمالي الطبليات 5×22.5	45
إجمالي قطع 5×7	84
قائمة تقطيع 5×7	688سم×4 | 488سم×4 | 364سم×8 | 320سم×42 | 250سم×4 | 172سم×2 | 165سم×1 | 162سم×2 | 160سم×2
	138سم×1 | 75سم×3 | 70سم×1 | 50سم×2 | 5سم×8
ألواح تلبيس 2.5 سم	204 لوح × 400 سم (مجموع الصفوف 640.5 م، 12 وجه)
أسمنت بورد 12 مم (122×244)	16 لوح (داخل دورات المياه)
العزل	96 لوح فوم صخري 80
الصبة	يجهزها العميل — 20 سم، مفرغة تحت دورات المياه

مراجعة التصميم مقابل قواعد المصنع

النوع	البند	التفاصيل	المقترح
ملاحظة	بحر المدادات	أطول بحر بدون جدار داخلي يحمل المداد: جهة أ: 500 سم. يحتاج رقم المصنع لأقصى بحر مسموح لتحديد المدادات اللي تُقوّى 20×5.	
ملاحظة	الصبة والدرج	ارتفاع الصبة 45 سم ← 3 درجة بقائمة 15.0 سم.	
ملاحظة	مناسيب رؤوس الفتحات	رؤوس الأبواب والشبابيك على مناسيب مختلفة: 210، 220، 310 سم.	
تنبيه	ميل سقف خفيف (بموافقة المصنع)	ميل 5° أقل من 20° — يصرّف باتجاه واحد بس يحتاج تغطية صاج معدني (مو قرميد) وعزل مائي تحت الصاج ووصلات مختومة.	صاج معدني بطول واحد من الحافة العالية للواطية بدون وصلات عرضية.
سؤال	يحتاج تأكيد	أقصى بحر للمداد بدون جدار داخلي قبل إضافة تقوية 7×5 (مداد 20×5)؟	
سؤال	يحتاج تأكيد	التغطية الصافية للوح التلبيس بعد التعشيق (مستنتجة مؤقتاً 18.67 سم من 280/15)؟	
سؤال	يحتاج تأكيد	هل يوضع أعمدة قصيرة فوق رأس الشباك/الباب إلى العلوي؟	
سؤال	يحتاج تأكيد	مكان الوصلة في القاعدة والعلوي إذا الجدار أطول من الطبلية؟	