

المنظور ثلاثي الأبعاد والمواد

النمط: جوزي غامق + إطارات سوداء — رندر واقعي بخامات حقيقية

جدول المواد والألوان

الخشب / الصبغة

خشب طبيعي فاتح (بدون صبغة)

القرميد

قرميد رمادي غامق

الزجاج

زجاج عاكس غامق

إطارات الشبابيك والأبواب

إطار ألومنيوم أسود

الكنار والزوايا


نفس الصبغة أعمق درجة

الصبة

خرسانة 45 سم

الدريزين: ألواح أفقية متقاربة (عصري)


تقسيم الشبابيك: بدون | الباب الرئيسي: زجاج بتقسيمات (فرنسي)

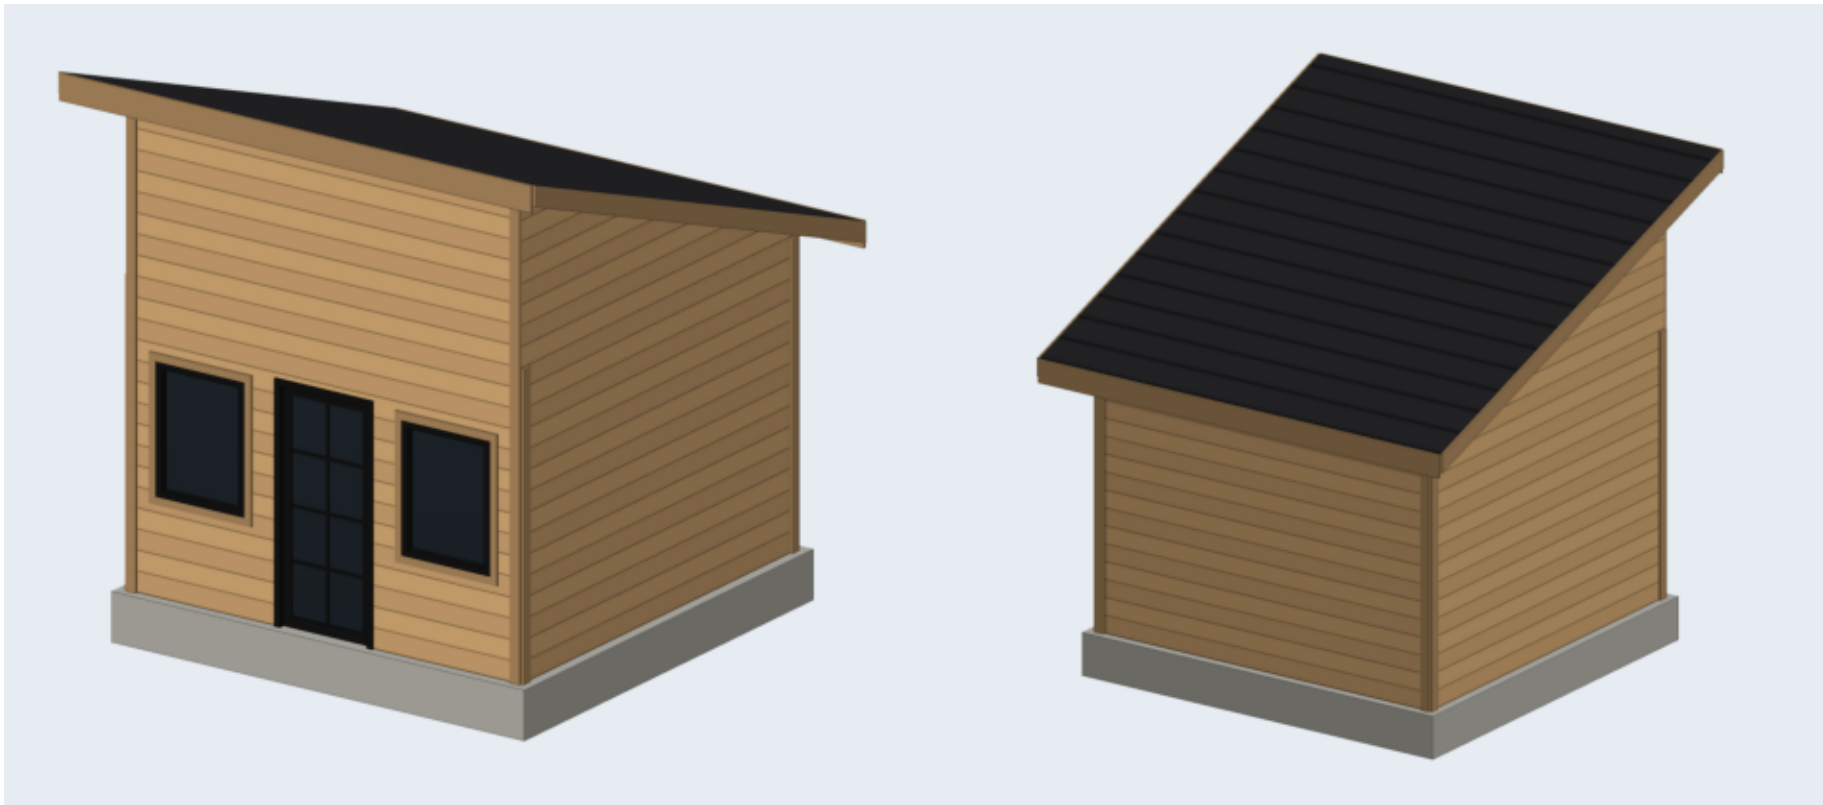


أنواع الدريزين المعتمدة (من مشاريع المصنع)



قوائم رأسية متقاربة (صورة 1)

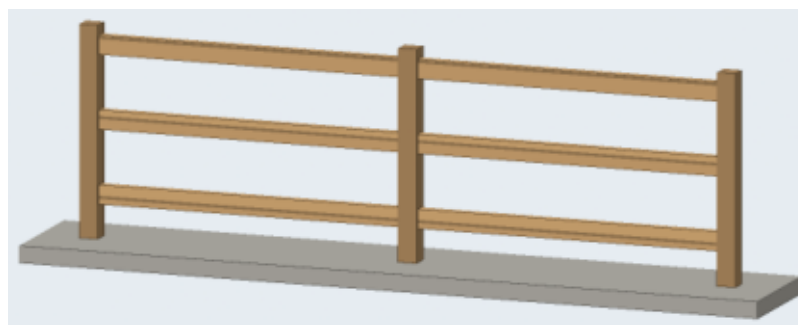

3 مربيع أفقية (صورة 2)

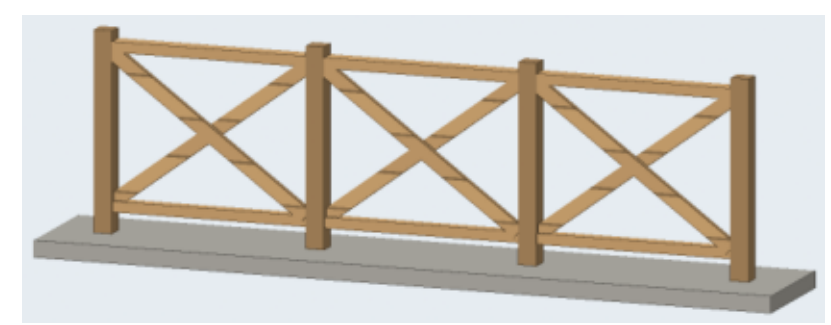

تقاطع X (صورة 5)

رقم اللوحة

W-01 (1/11)

التاريخ

2026-10-01

المقياس

1:50

عنوان اللوحة

المنظور والمواد

المشروع / العميل

غرفة 4x4 بسقف مانل
عميل — غرفة مستقلة


مصنع وتد الأخشاب

Watad Wood Factory




[illegible]

المشروع / العمل	عنوان اللوحة	المقياس	التاريخ	رقم اللوحة
مصنع وتد الأخشاب Watad Wood Factory	غرفة 4x4 بسقف مائل عميل — غرفة مستقلة	المسقط الأفقي	2026-10-01	W-02 (2/11)

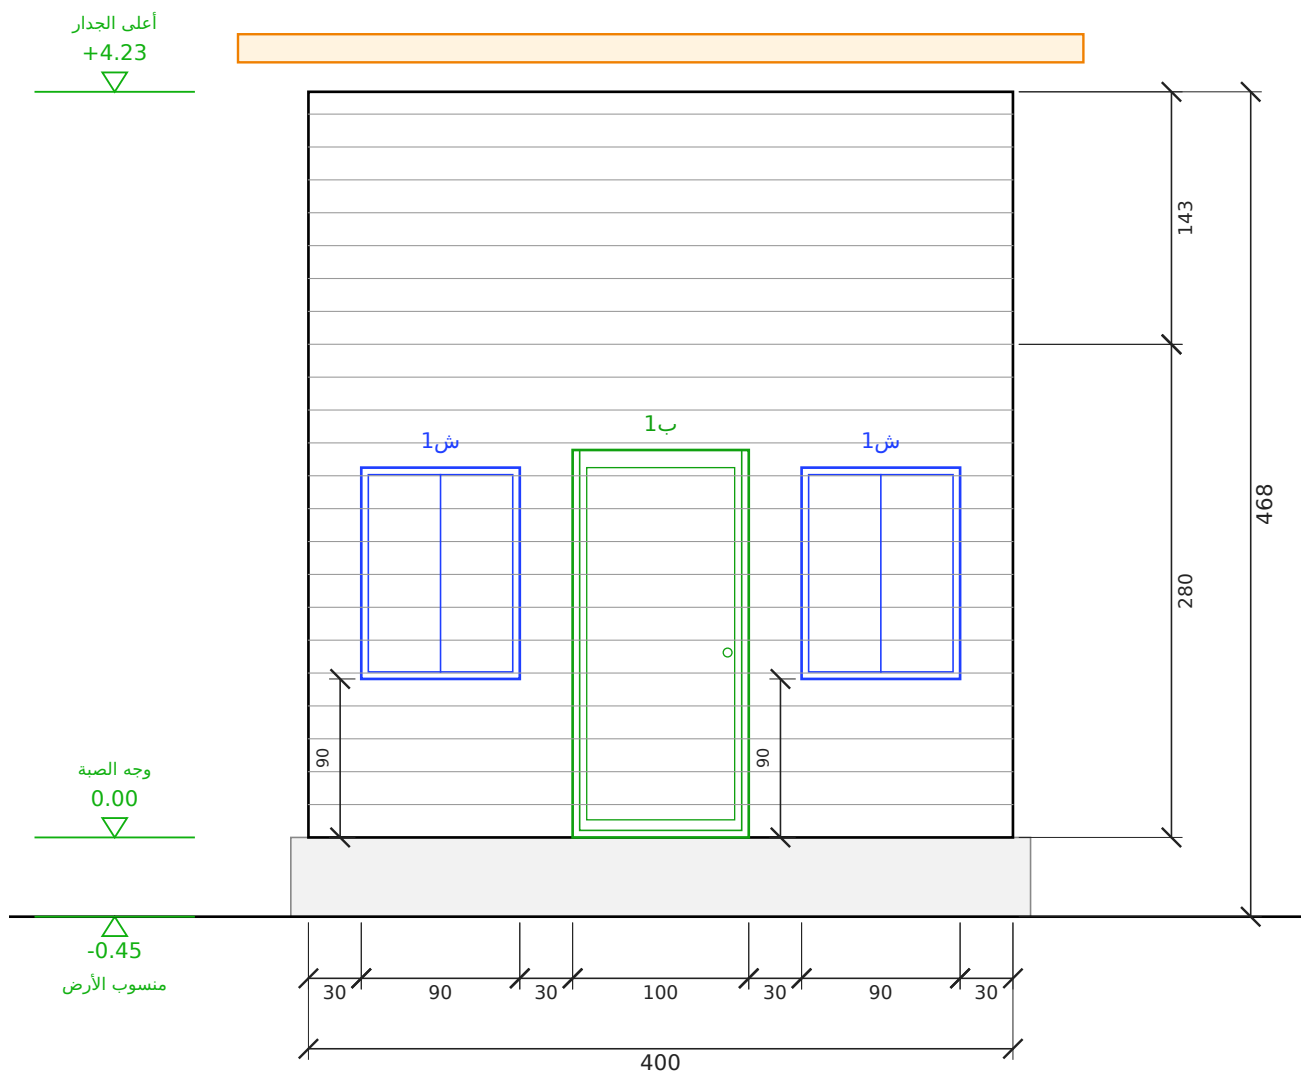

الواجهة الأمامية


مقياس 1:50 | الوحدة: سم

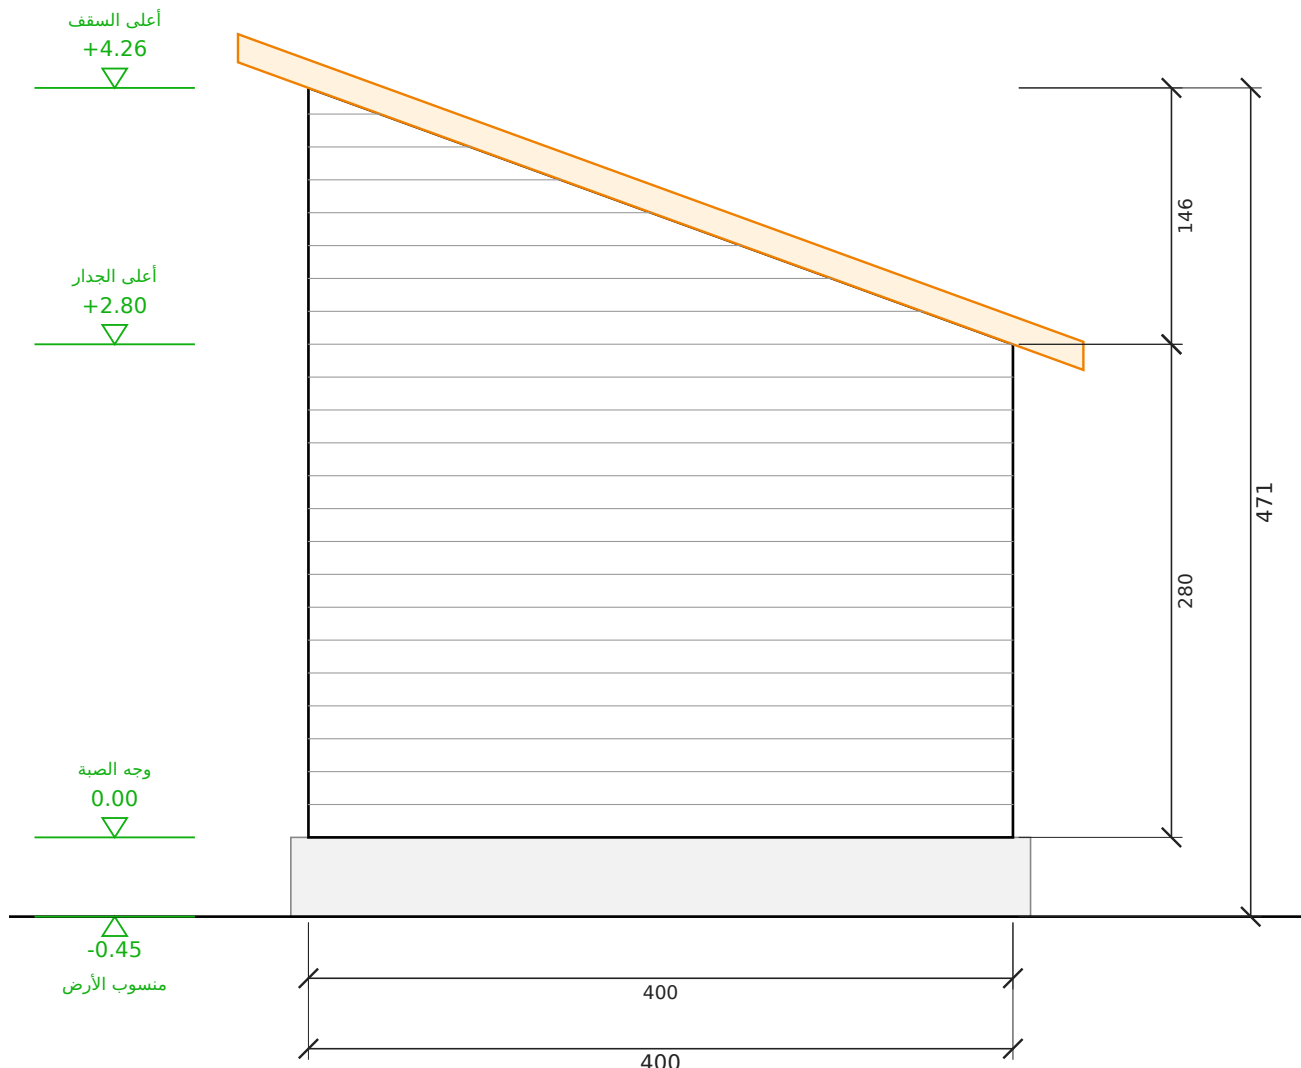

الواجهة الشرقية


مقياس 1:50 | الوحدة: سم

رقم اللوحة	التاريخ	المقياس	عنوان اللوحة	المشروع / العميل	مصنع وتد الأخشاب Watad Wood Factory
W-03 (3/11)	2026-10-01	1:50	الواجهة الأمامية والواجهة الشرقية	غرفة 4x4 بسقف مائل عميل - غرفة مستقلة	

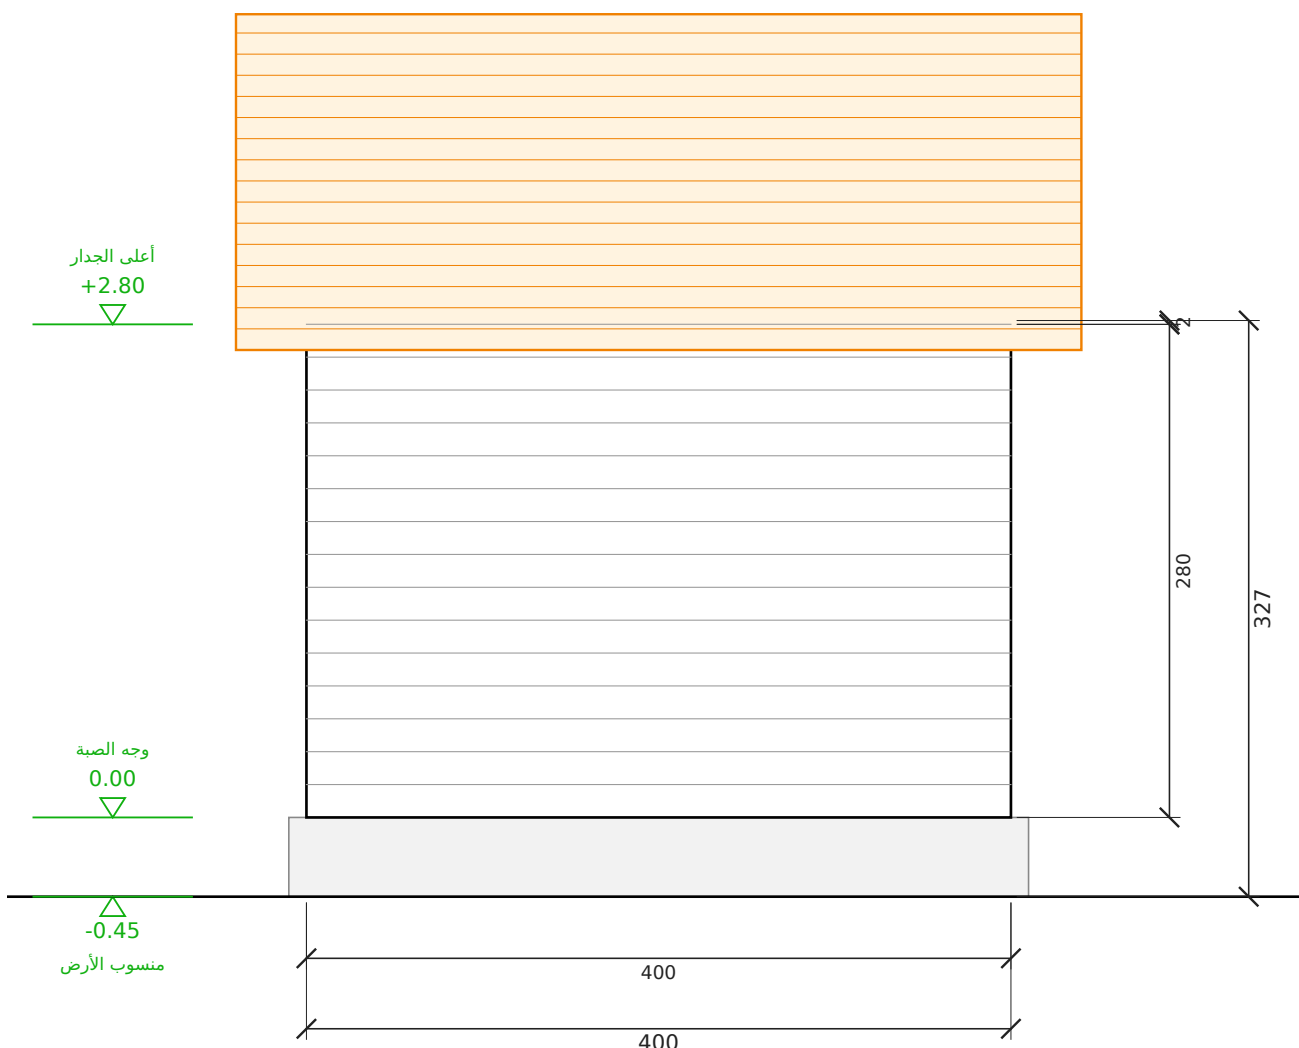

الواجهة الخلفية

مقياس 1:50 | الوحدة: سم

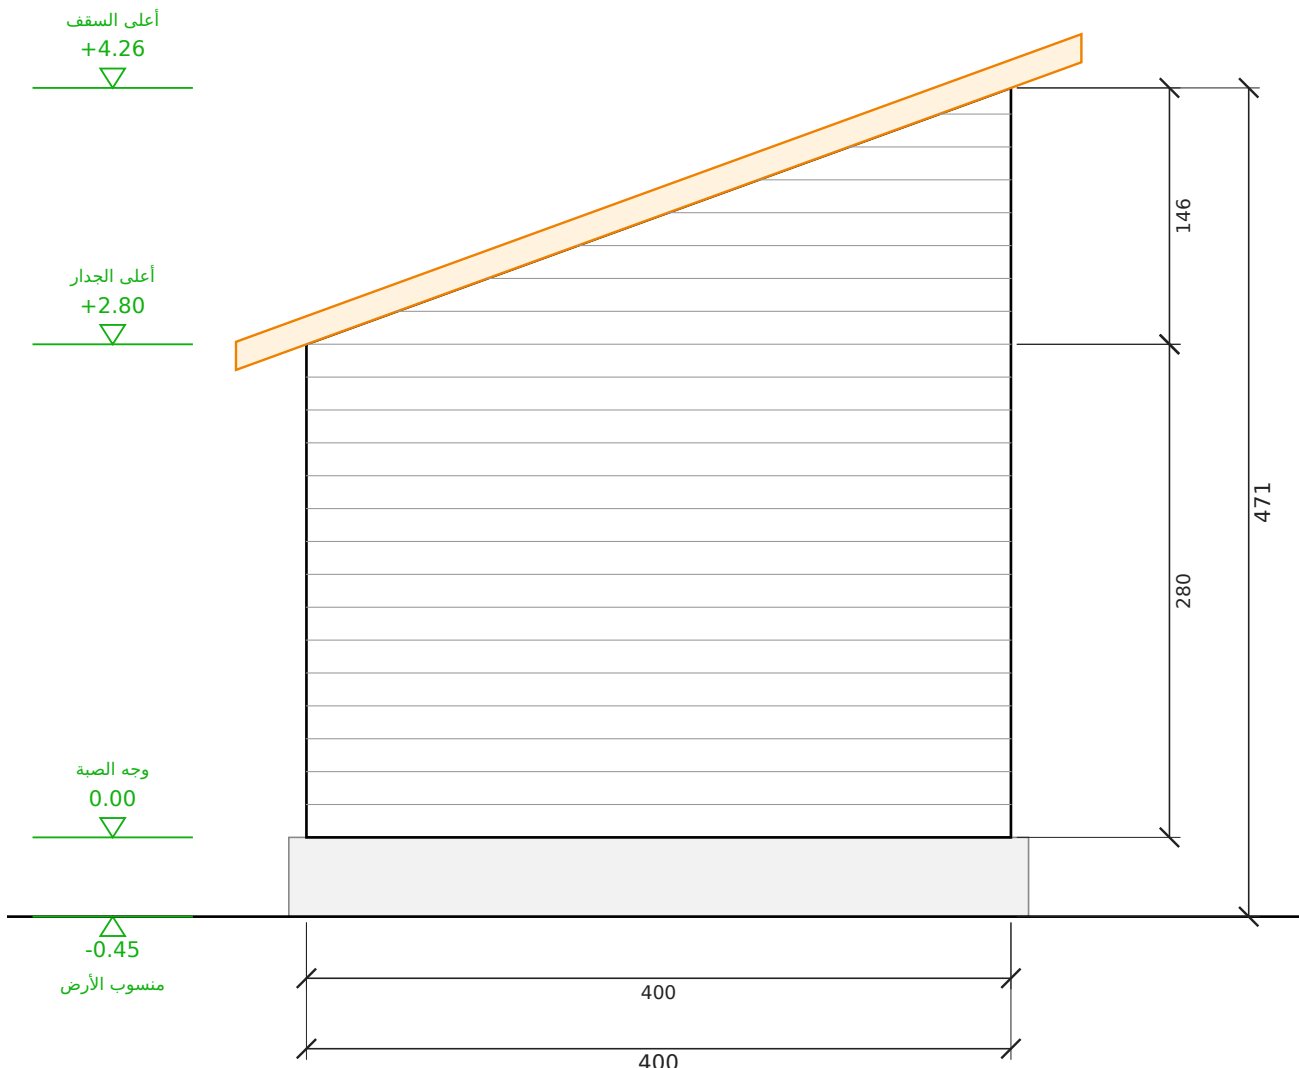


الواجهة الغربية



مقياس 1:50 | الوحدة: سم

رقم اللوحة	التاريخ	المقياس	عنوان اللوحة	المشروع / العميل	مصنع وتد الأخشاب Watad Wood Factory
W-04 (4/11)	2026-10-01	1:50	الواجهة الخلفية والواجهة الغربية	غرفة 4x4 بسقف مائل عميل - غرفة مستقلة	

مسقط السقف (مائل باتجاه واحد)
رفر 40 سم من كل جهة | مقياس 1:50

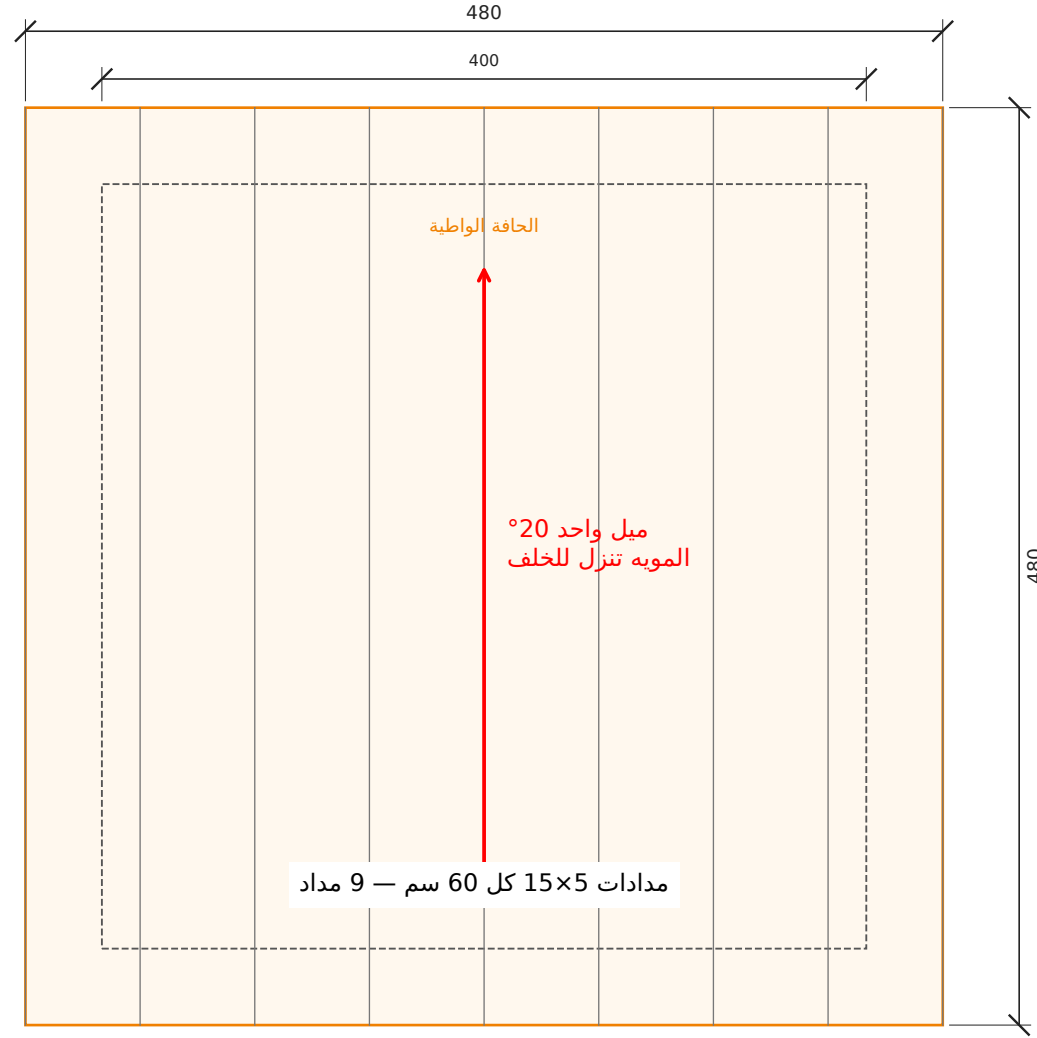

قطاع عرضي أ-أ
مقياس 1:50 | الوحدة: سم

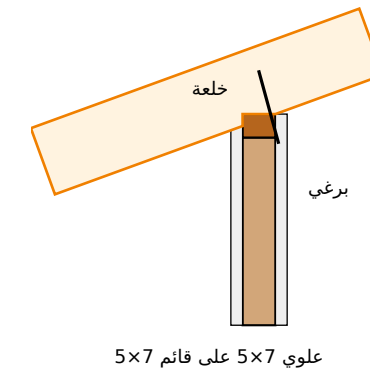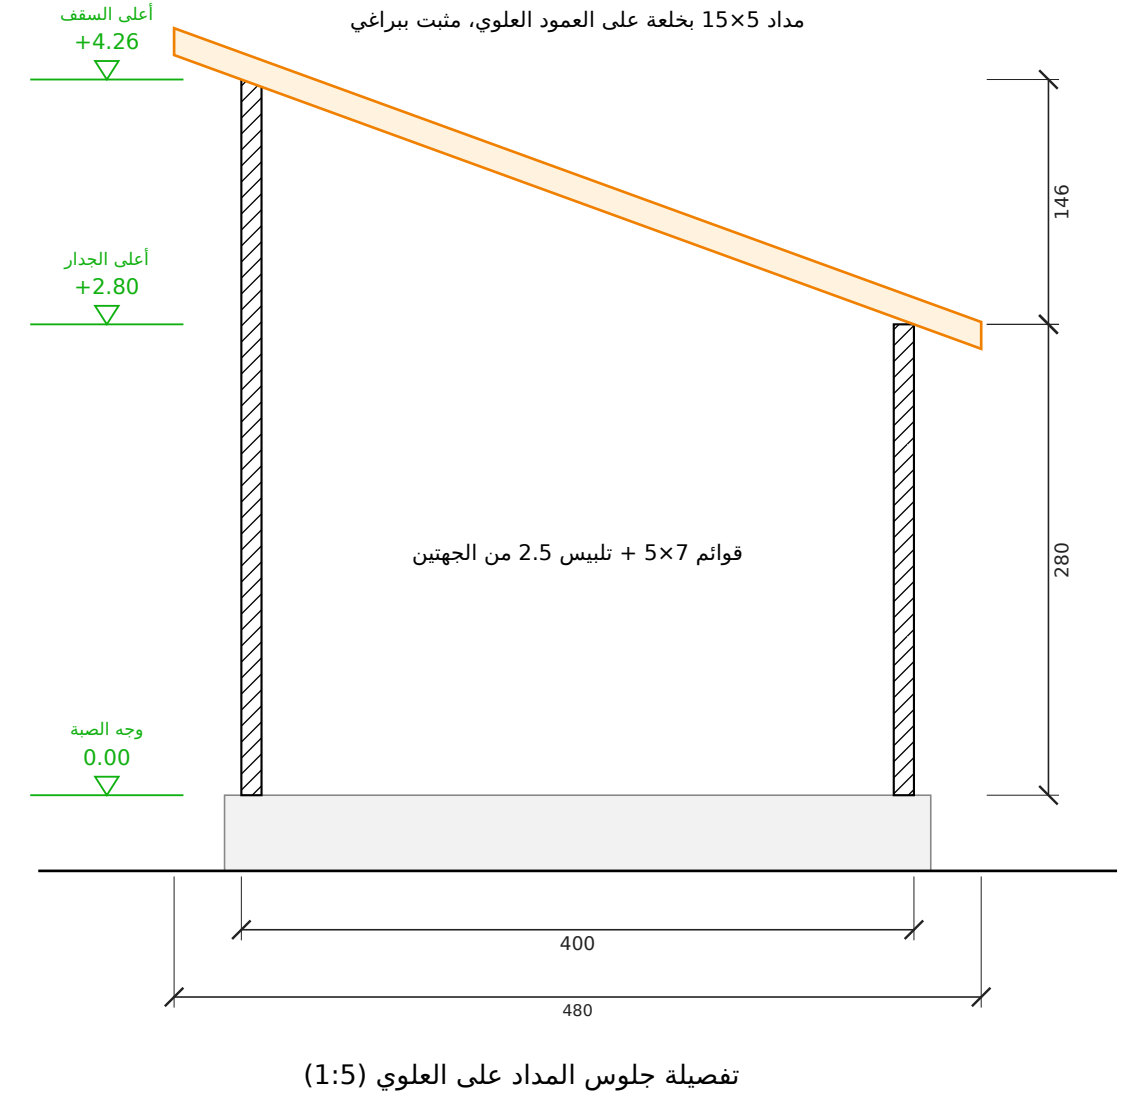

رقم اللوحة

W-05 (5/11)

التاريخ

2026-10-01

المقياس

1:50

عنوان اللوحة

مسقط السقف والقطاع

المشروع / العميل

غرفة 4x4 بسقف مائل
عميل — غرفة مستقلة

مصنع وتد الأخشاب
Watad Wood Factory



جدول مقاسات الأبواب والشبابيك
مقاس الفتحة الصافي في الجدار - الوحدة: سم

الرمز	النوع	العرض (سم)	الارتفاع (سم)	ارتفاع الجلسة (سم)	العدد	الموقع
ب1	باب	100	220	-	1	الأمامية
ش1	شباك	90	120	90	2	الأمامية 2

الإجمالي: أبواب 1 - شبابيك 2

جدول المساحات وبيانات المشروع والتسعير

جدول المساحات

م	الفراغ	الأبعاد (م)	المساحة (م2)
1	الغرفة	3.76 × 3.76	14.14
	المساحة الصافية الداخلية		14.14
	المساحة الإجمالية المبنية	4.00 × 4.00	16.00

بيانات المشروع

البند	البيان
المشروع	غرفة 4×4 بسقف مائل
العميل	عميل — غرفة مستقلة
الموقع	—
الاستخدام	غرفة / استراحة
التاريخ	2026-10-01
نظام البناء	هيكل خشب 5×7 + تليس 2.5 سم من الجهتين
السقف	مائل باتجاه واحد 20° — قرميد معدني


التسعير

البند	القيمة
المساحة المبنية (م2)	16.00
سعر المتر المربع	1,196 ريال
الإجمالي	19,136 ريال


ملاحظات:

- السعر للمساحة المبنية حسب المخطط المعتمد.
- الصبة والتوريدات الخارجية على العميل ما لم يُذكر غير ذلك.

تأطير جدار جنوب — الطول 388 سم، الارتفاع 426 سم

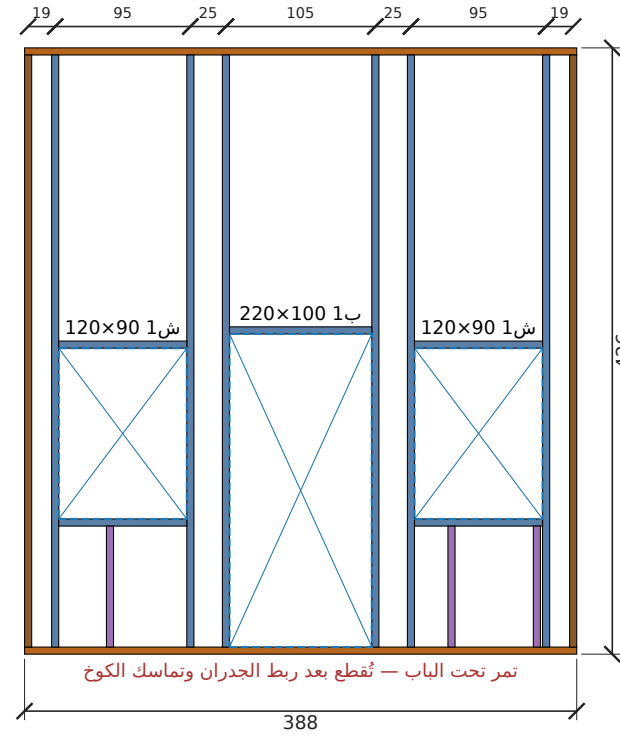

تأطير جدار شرق — الطول 388 سم، الارتفاع 280 سم

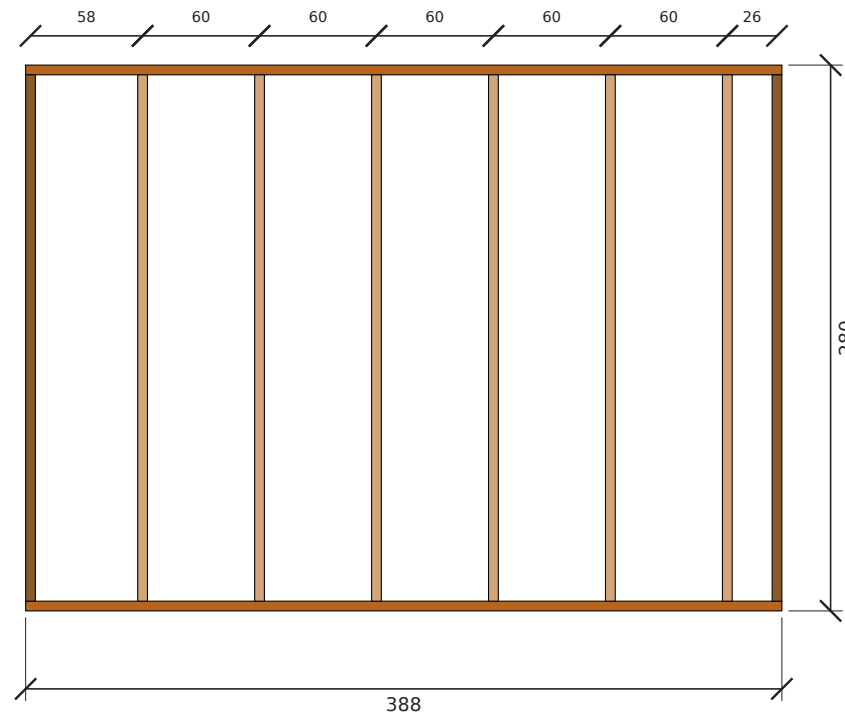

قاعدة سفلية علوي عمود عمود زاوية جنب فتحة رأس فتحة جلسة شباك عمود قصير

رقم اللوحة

W-08 (8/11)

التاريخ

2026-10-01

المقياس

—

عنوان اللوحة

لوحات التأطير (للورشة)


المشروع / العميل

غرفة 4x4 بسقف مائل
عميل — غرفة مستقلة


مصنع وتد الأخشاب
Watad Wood Factory



تأطير جدار شمال — الطول 388 سم، الارتفاع 280 سم

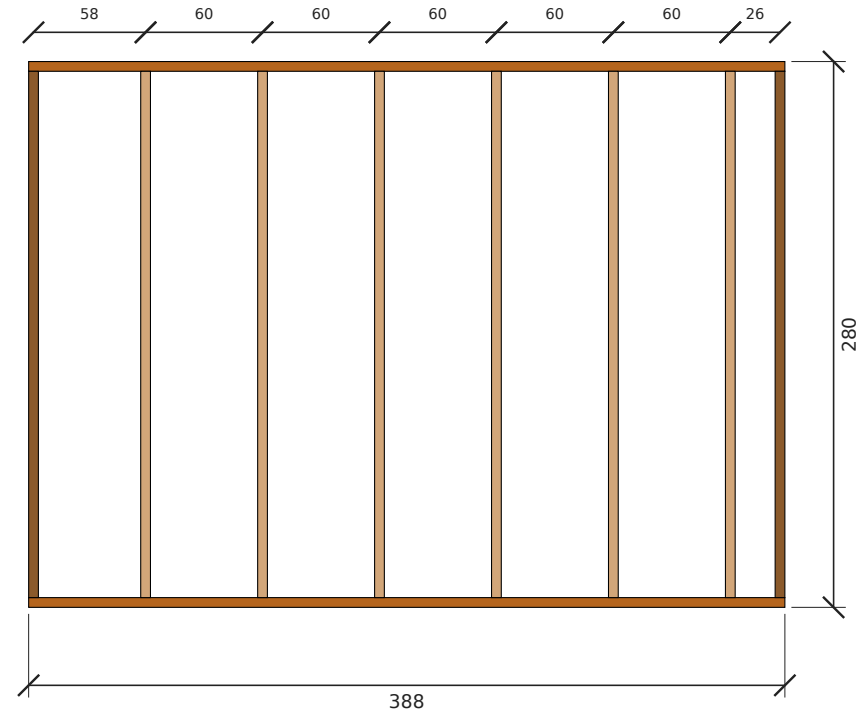

تأطير جدار غرب — الطول 388 سم، الارتفاع 280 سم

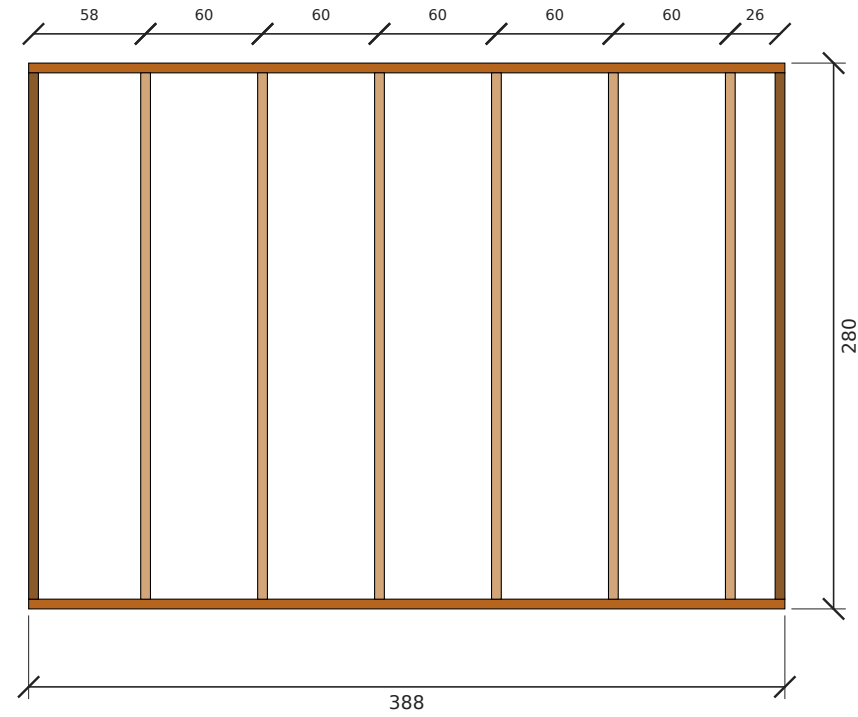

قاعدة سفلية علوي عمود عمود زاوية جنب فتحة رأس فتحة جلسة شباك عمود قصير

رقم اللوحة

W-09 (9/11)

التاريخ

2026-10-01

المقياس

—

عنوان اللوحة

لوحات التأطير (للورشة)

المشروع / العميل

غرفة 4×4 بسقف مائل
عميل — غرفة مستقلة

مصنع وتد الأخشاب
Watad Wood Factory



جدول الكميات وخطة تقطيع الطبلیات

البند	القيمة
الارتفاع المطلوب / المعتمد	280 / 280 سم
السقف	جملون 20° — قمة 426 سم من وجه الصبة
المدادات 15×5	9 مداد (9 لكل جهة) × 511 سم — من طبلية 520
طبلیات الطريقة الأولى (مداد + عمود)	9 طبلية × 520 سم
طبلیات الطريقة الثانية (3 أعمدة)	8 طبلية × 320 سم
طبلیات الطريقة الثانية (طويلة)	3 طبلية × 520 سم
إجمالي الطبلیات 22.5×5	20
إجمالي قطع 5×7	48
قائمة تقطيع 5×7	416سم×8 388سم×8 270سم×24 100سم×1 90سم×4 85سم×3
ألواح تلبیس 2.5 سم	124 لوح × 400 سم (مجموع الصفوف 476.5 م، 8 وجه)
أسمنت بورد 12 مم (244×122)	0 لوح (داخل دورات المياه)
العزل	بدون (غير مطلوب)
الصبة	يجهزها العميل — 20 سم، مفرغة تحت دورات المياه

مراجعة التصميم مقابل قواعد المصنع

النوع	البند	التفاصيل	المقترح
ملاحظة	بحر المدادات	أطول بحر بدون جدار داخلي يحمل المداد: جهة أ: 400 سم. يحتاج رقم المصنع لأقصى بحر مسموح لتحديد المدادات اللي تُقوّى 5×20.	
ملاحظة	الصبة والدرج	ارتفاع الصبة 45 سم ← 3 درجة بقائمة 15.0 سم.	
ملاحظة	مناسيب رؤوس الفتحات	رؤوس الأبواب والشبابيك على مناسيب مختلفة: 210، 220 سم.	
سؤال	يحتاج تأكيد	أقصى بحر للمداد بدون جدار داخلي قبل إضافة تقوية 5×7 (مداد 5×20)؟	
سؤال	يحتاج تأكيد	التغطية الصافية للوح التليس بعد التعشيق (مستنتجة مؤقتاً 18.67 سم من 280/15)؟	
سؤال	يحتاج تأكيد	هل يوضع أعمدة قصيرة فوق رأس الشباك/الباب إلى العلوي؟	
سؤال	يحتاج تأكيد	مكان الوصلة في القاعدة والعلوي إذا الجدار أطول من الطيلية؟	