
## جدول مساحات الموقع

| البند | المقاس | المساحة (م²) |
|---|---|---|
| مساحة الأرض (شبه منحرف) | 25.00 × 24.27/16.23 م | 499.6 |
| مسطح الأكواخ (2) | 2 × 7.00 × 9.00 م | 126.0 |
| تراس الكوخ | 2 × 7.00 × 2.40 م | 33.6 |
| مسبح | 2 × 2.30 × 4.80 م | 22.1 |
| جلسة خارجية | 2 × 3.40 × 4.40 م | 29.9 |
| بلاط | | 19.4 |
| موقف سيارة | 2 × 3.00 × 5.50 م | 33.0 |
| ممر | 2 × 1.00 × 11.17 م | 22.3 |
| أحواض زراعة | 2 × 0.90 × 6.60 م | 11.9 |
| المسطحات الخضراء (حديقة) | الباقي | 201.4 |

الموقع العام وتنسيق الحديقة (لاندسكيب)
الأرض 500 م² | الأبعاد بالسنتيمتر

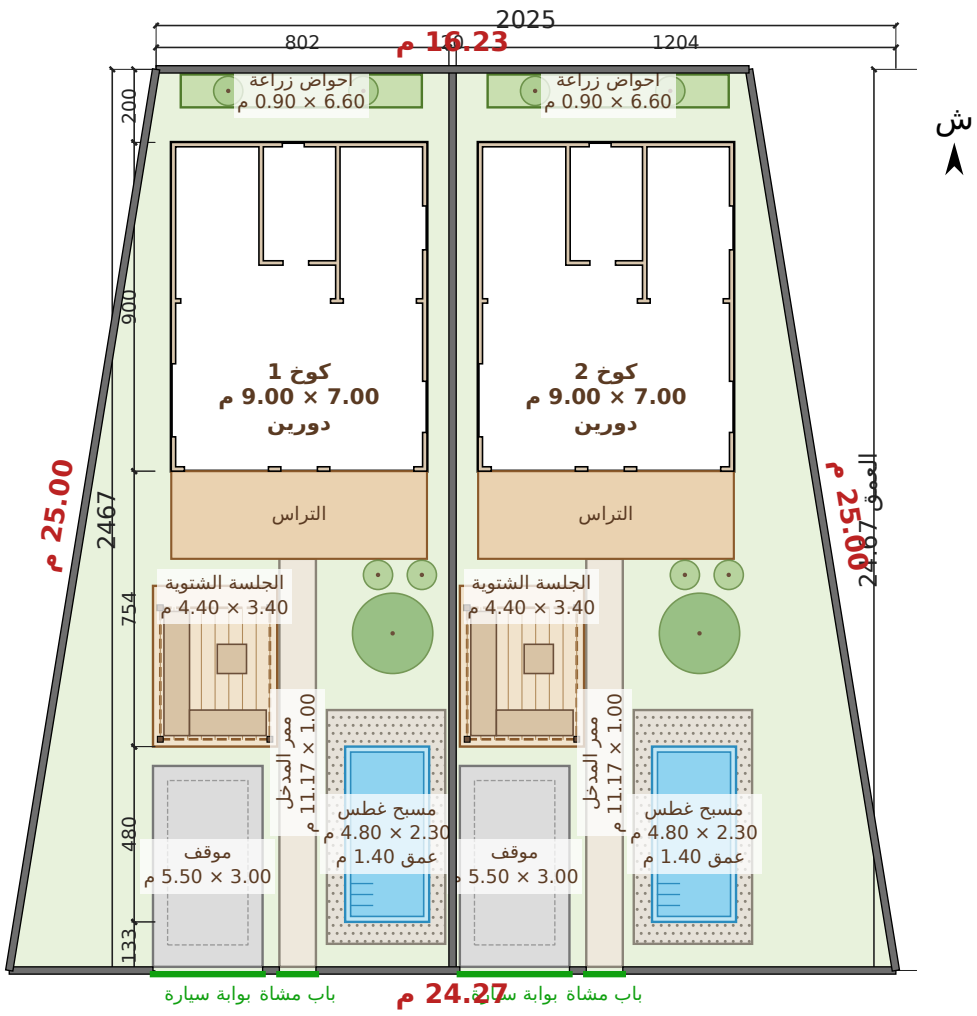



شارع عرض 15 م

- الأرض مقسومة بسور بالنص لوحدتين مستقلتين (≈ 250 م² لكل وحدة) — تأجير مستقل وخصوصية كاملة.
- الشاليه دورين ببصمة 7.00 × 9.00 م — الحوش الأمامي لكل وحدة صار 11.3 م للاندسكيب.
- كل وحدة: بوابة سيارة 3.00 م لموقف + باب مشاة بممر مستقيم لدرج التراس، ومسبح غطس 2.30 × 4.80 م ببلاط حوله.
- جلسة شتوية 3.40 × 4.40 م تحت برجولة خشب (يمكن تسقيفها وتقفيلها زجاج) بجلسة L ومشب نار بالنص.
- سور بلك 2.20 م بغطاء خشب على أضلاع الأرض (شبه منحرف) + السور الفاصل بين الوحدتين، وأحواض زراعة على السور الخلفي.

| المشروع / العميل | عنوان اللوحة | المقياس | التاريخ | رقم اللوحة |
|---|---|---|---|---|
| **مصنع وتد الأخشاب** Watad Wood Factory<br>**شاليهين الهدا الاستثماري — دورين — غرفتين وصالة لكل شاليه — 2 دور × 7.00 × 9.00 م**<br>**عميل — الهدا (استثماري)** | **الموقع العام واللاندسكيب** | **1:200** | **2026-10-23** | **A-01 (1/12)** |

# المسقط الأفقي مع الفرش — الدور الأرضي

الأبعاد بالسنتيمتر - الجدران: قوائم 7×5 + تلبيس 2.5 من الجهتين (12 سم) | منسوب الأرضية +0.00

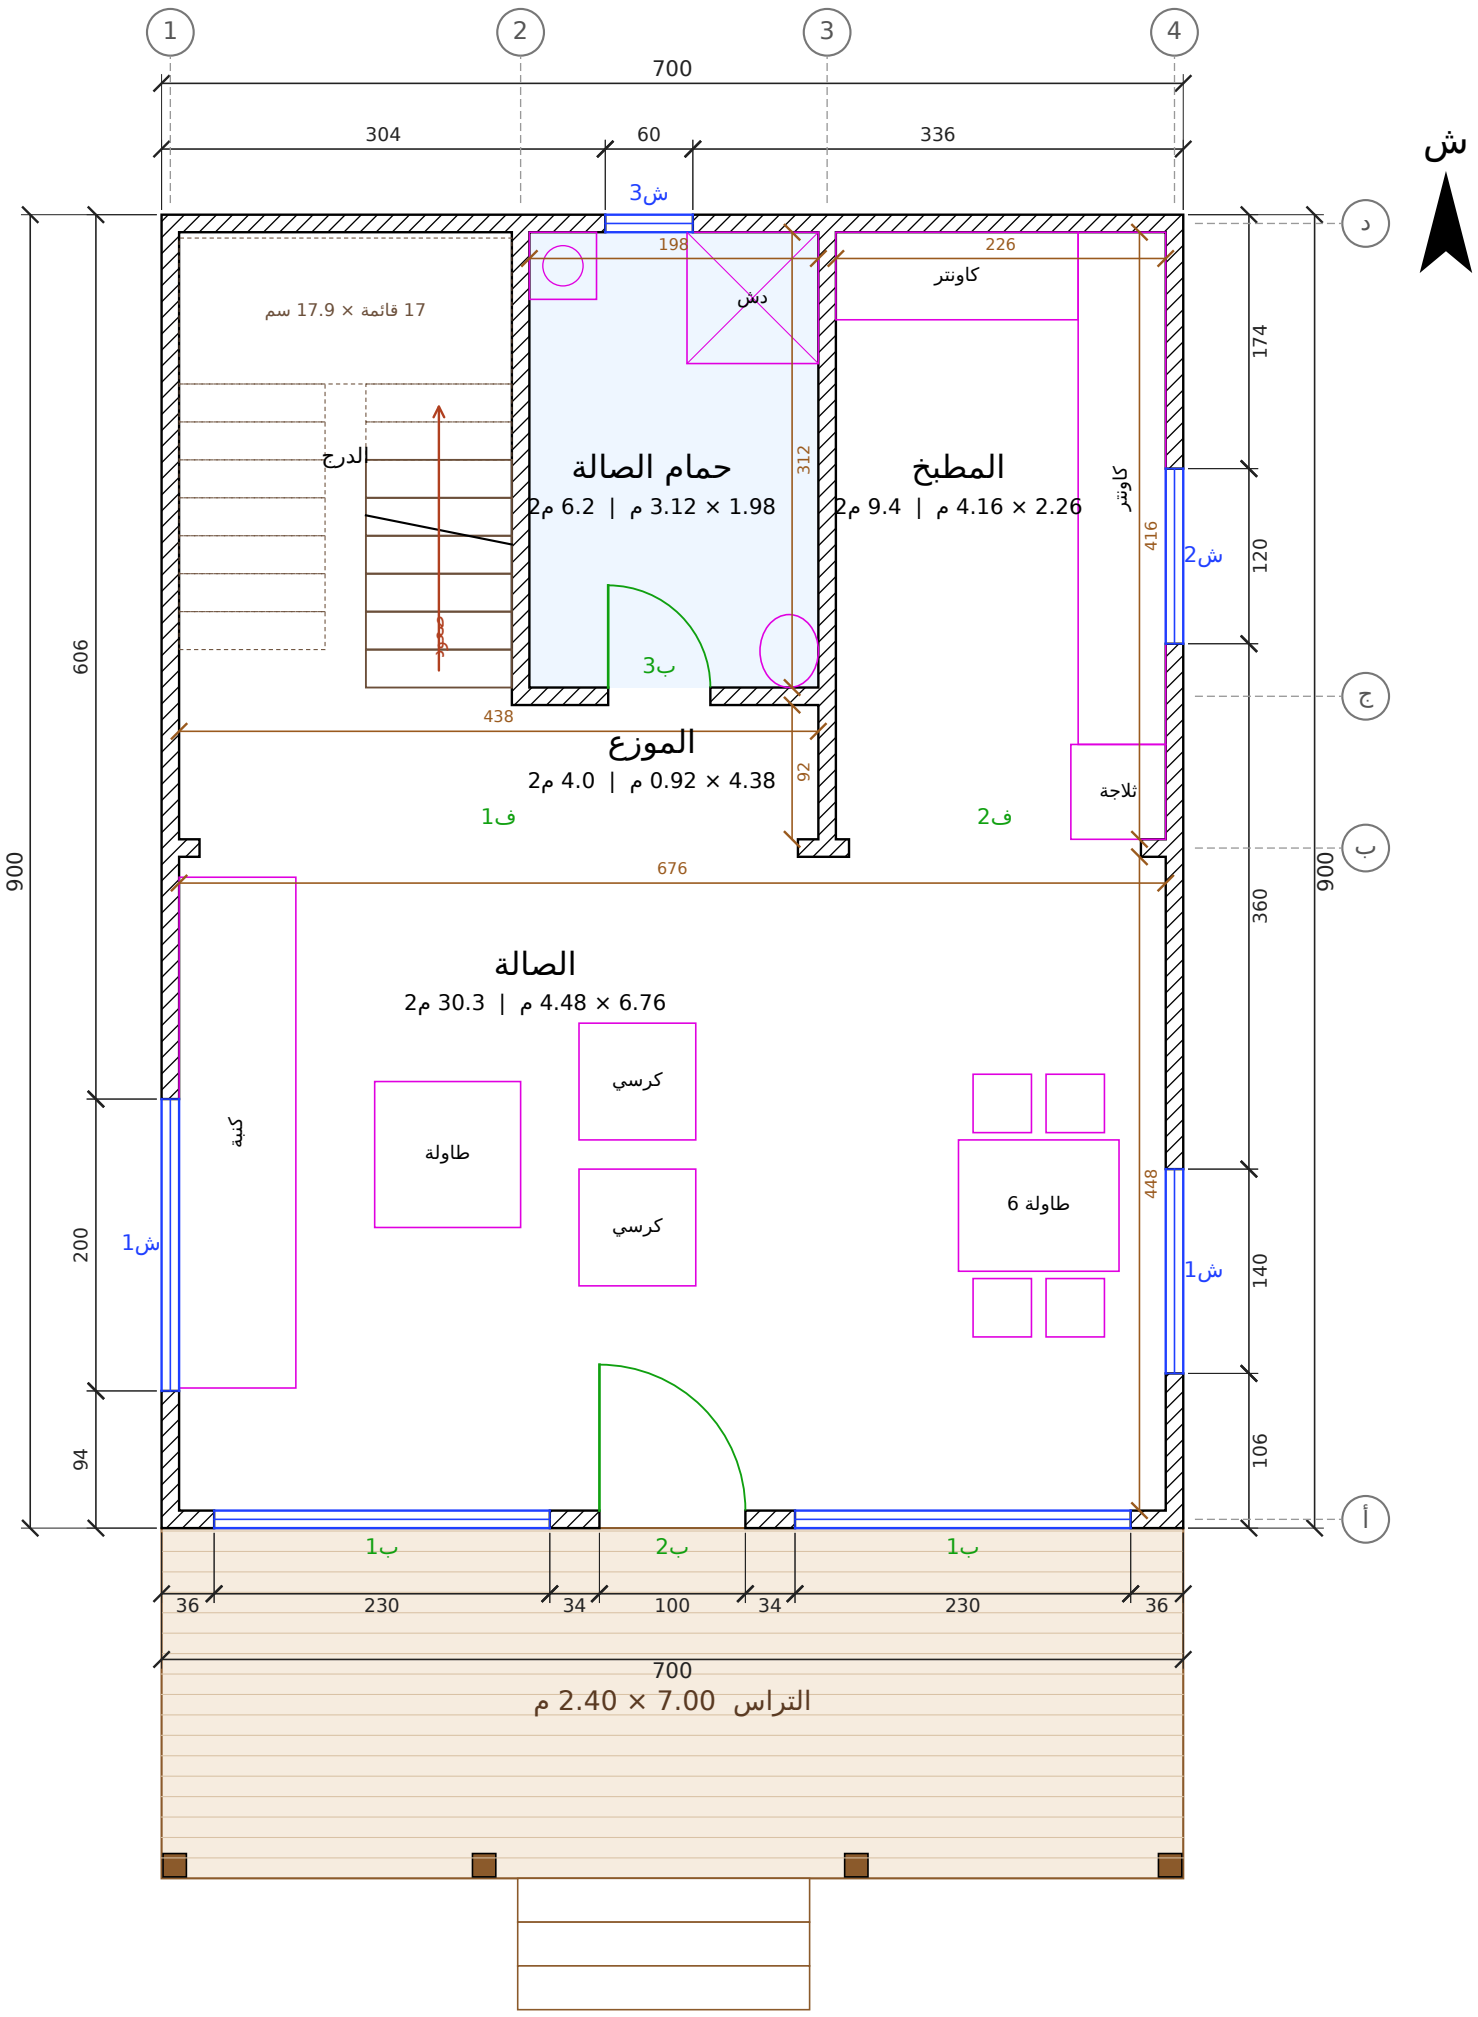



3 درجات × 15 سم

| | | | | | |
|---|---|---|---|---|---|
| مصنع وتد الأخشاب<br>Watad Wood Factory | المشروع / العميل<br>شاليهين الهدا الاستثماري — دورين — غرفتين وصالة لكل شاليه — 7.00 × 9.00 × 2 دور<br>عميل — الهدا (استثماري) | عنوان اللوحة<br>المسقط الأفقي — الدور الأرضي | المقياس<br>1:50 | التاريخ<br>2026-10-23 | رقم اللوحة<br>A-02 (2/12) |


# المسقط الأفقي مع الفرش — الدور الأول

الأبعاد بالسنتيمتر - الجدران: قوائم 7×5 + تلبيس 2.5 من الجهتين (12 سم) | منسوب الأرضية +3.05

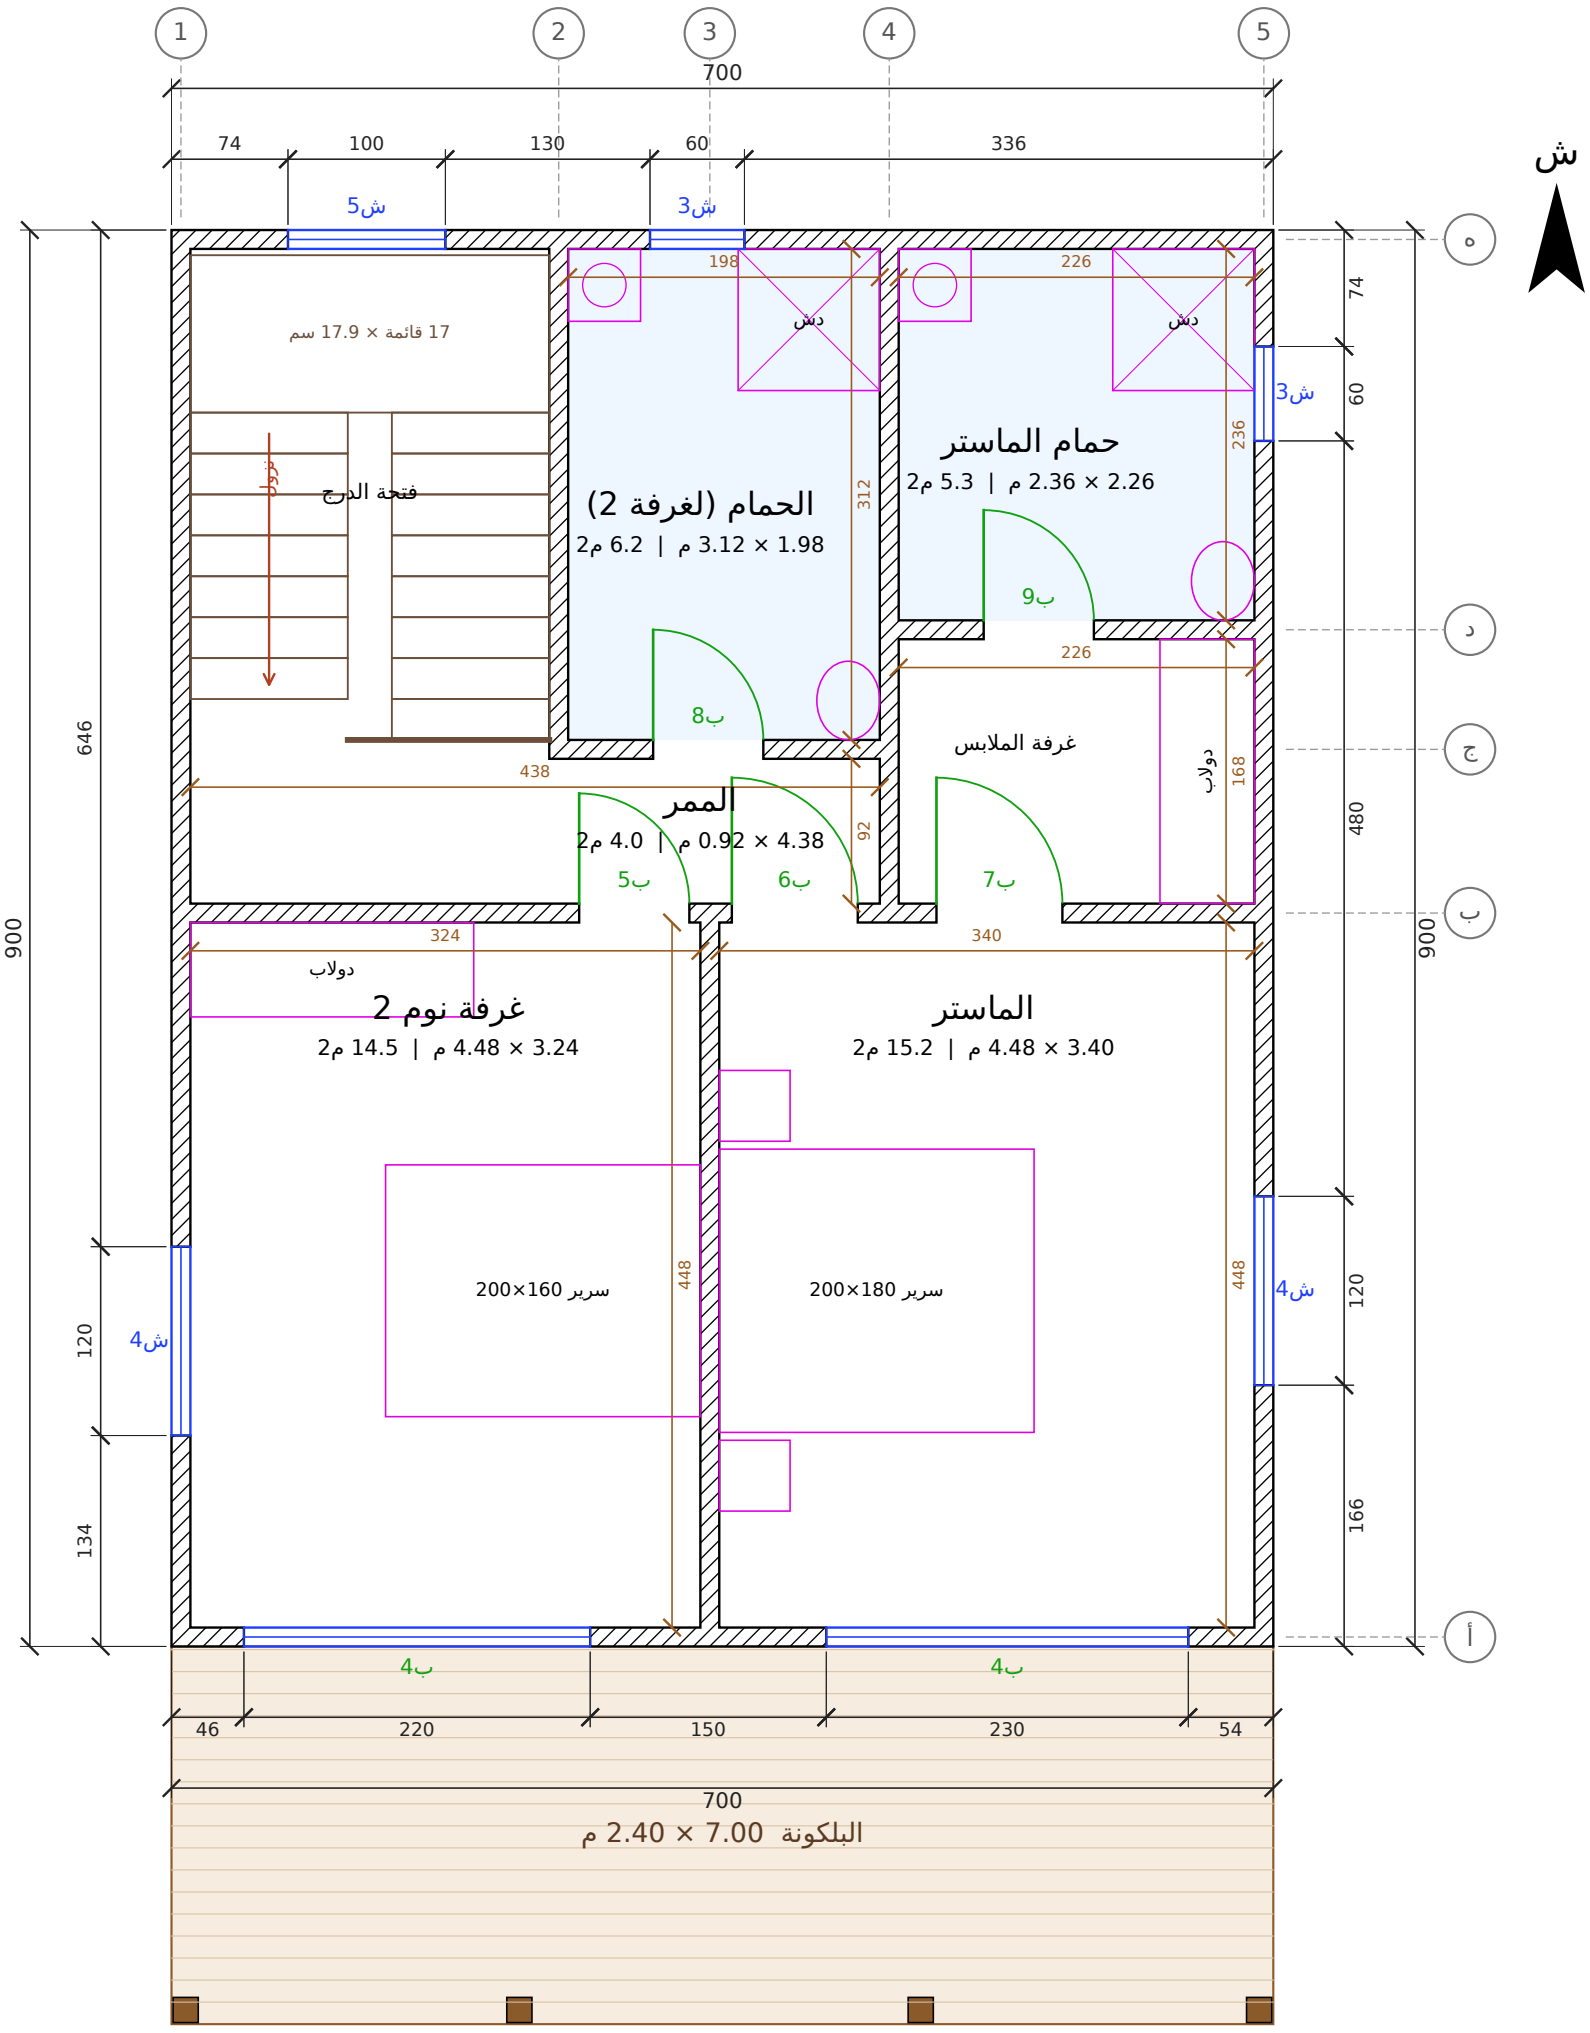



| المشروع / العميل | عنوان اللوحة | المقياس | التاريخ | رقم اللوحة |
|---|---|---|---|---|
| **شاليهين الهدا الاستثماري — دورين — غرفتين وصالة لكل شاليه — 7.00 × 9.00 × 2 دور**<br>**عميل — الهدا (استثماري)** | **المسقط الأفقي — الدور الأول** | **1:50** | **2026-10-23** | **A-03 (3/12)** |

**مصنع وتد الأخشاب**
Watad Wood Factory

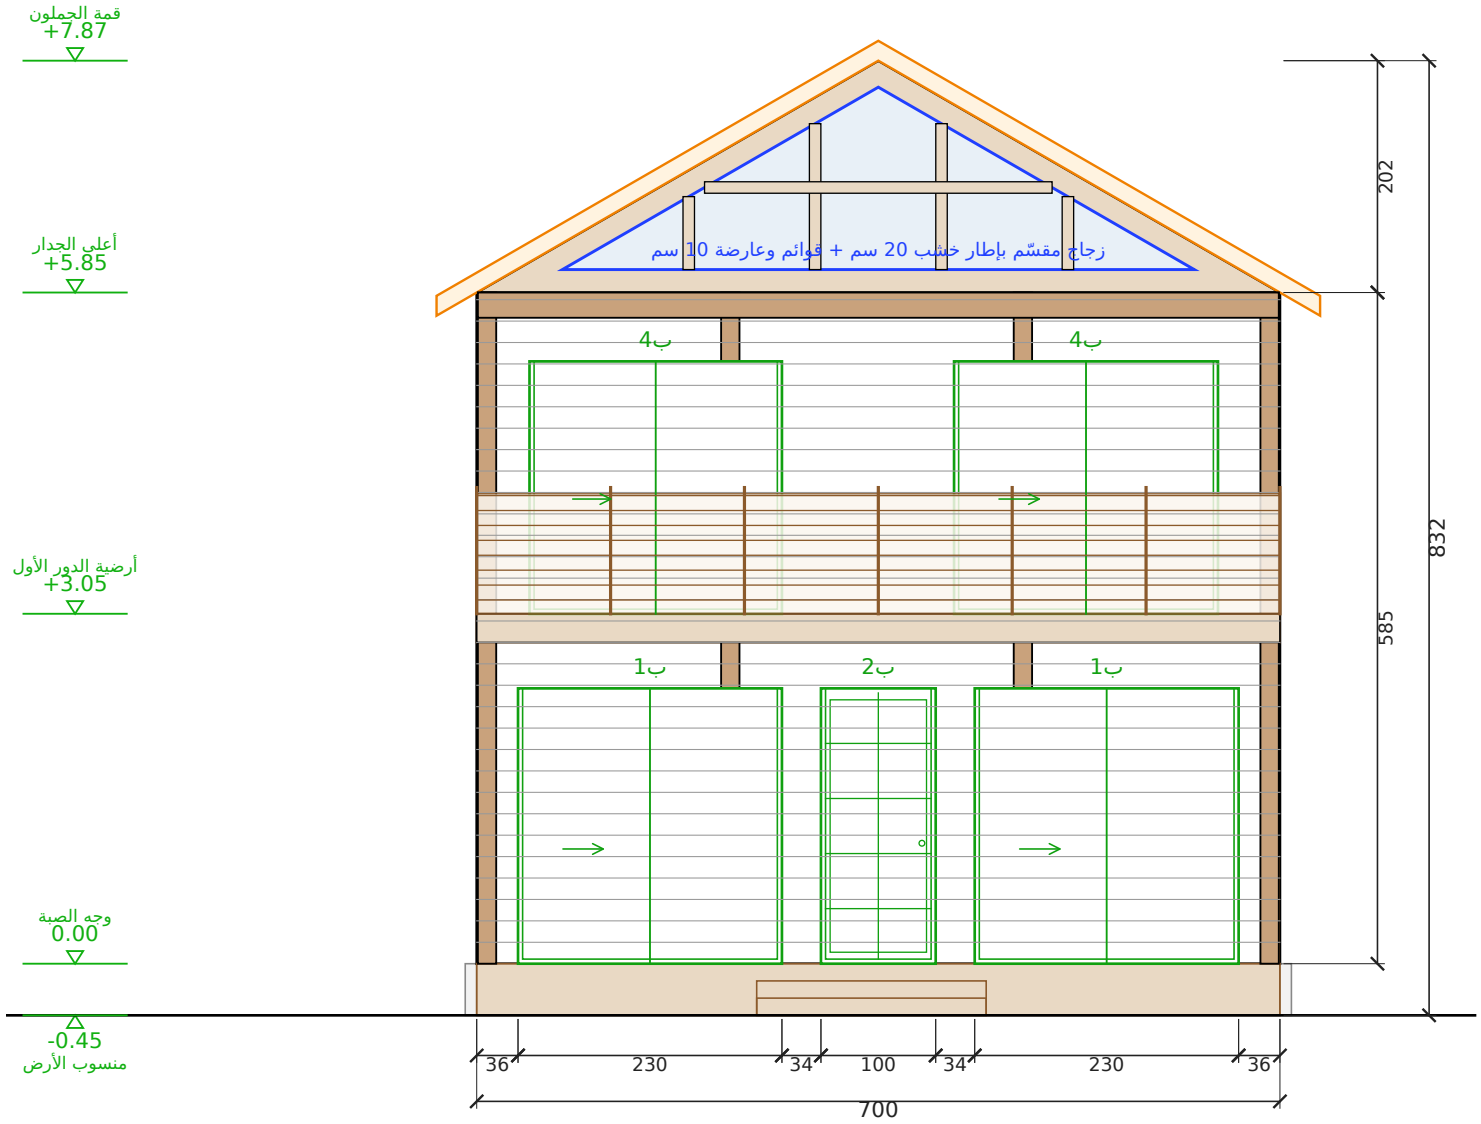


## الواجهة الأمامية

مقياس 1:50 | الوحدة: سم

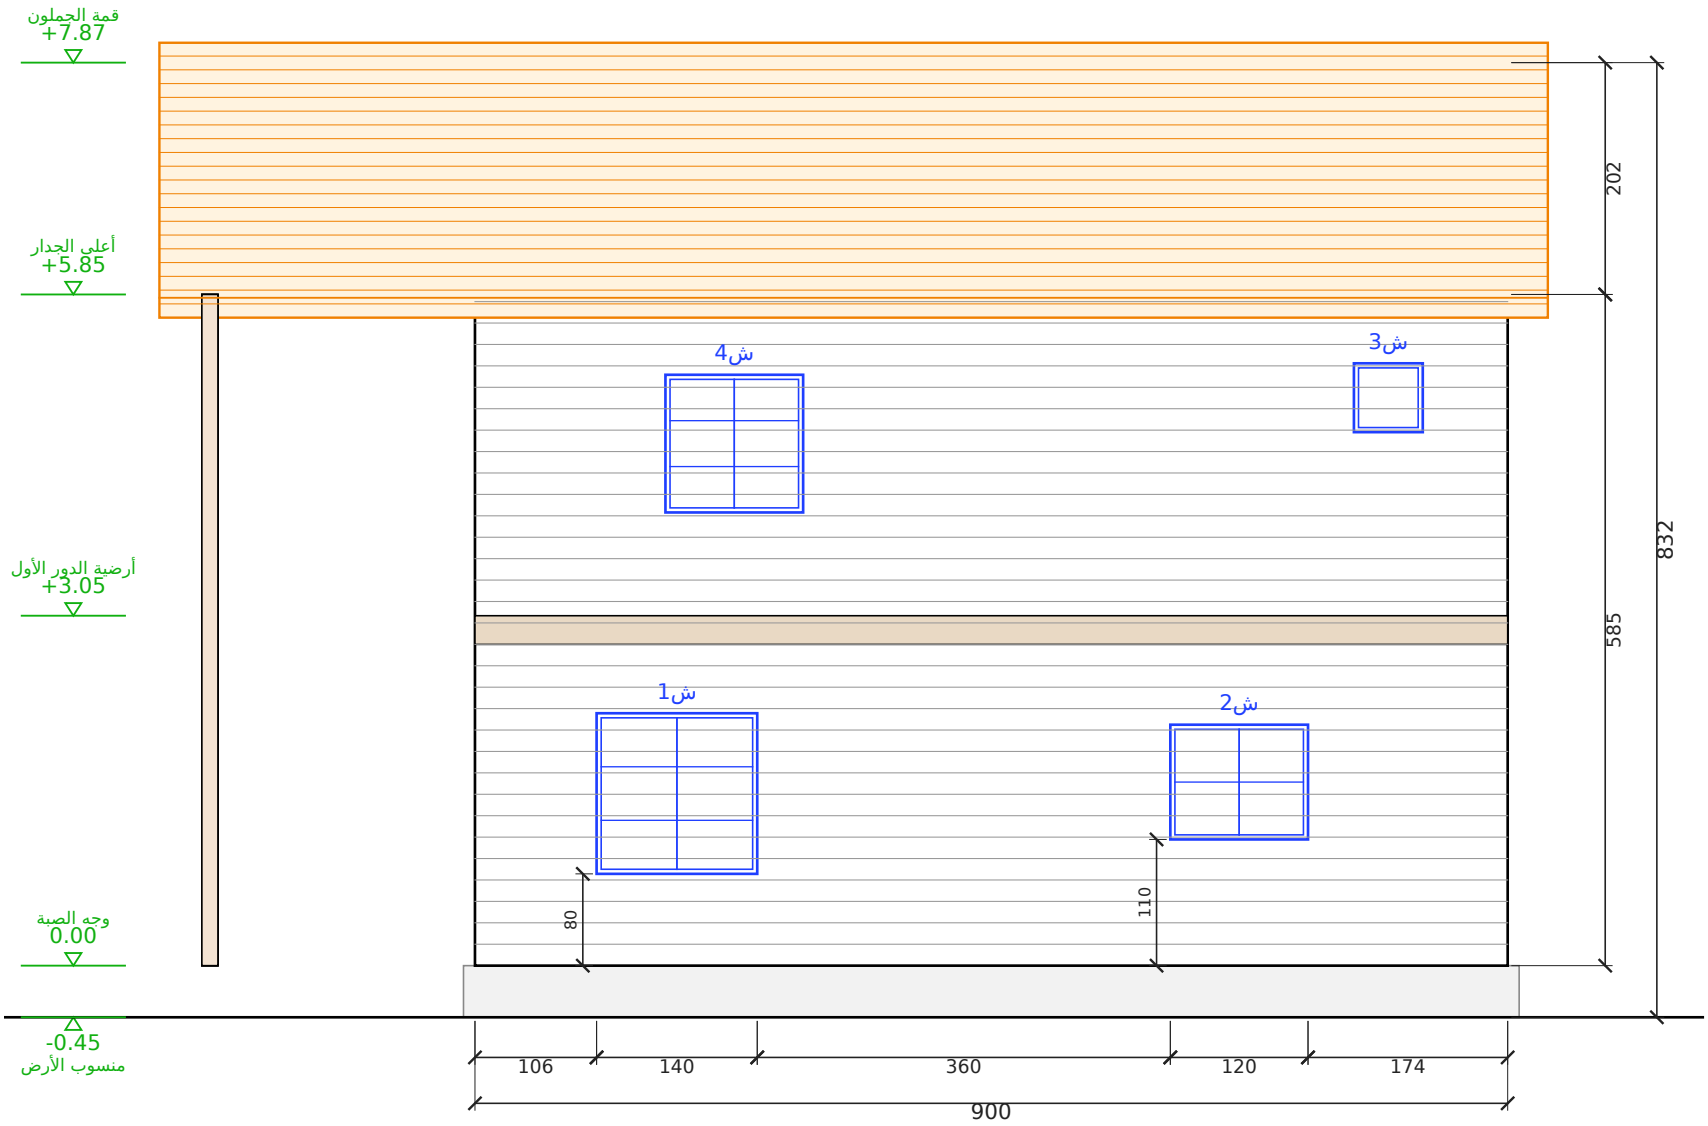



## الواجهة الشرقية

مقياس 1:50 | الوحدة: سم


| المشروع / العميل | عنوان اللوحة | المقياس | التاريخ | رقم اللوحة |
|---|---|---|---|---|
| شاليهين الهدا الاستثماري — دورين — غرفتين وصالة لكل شاليه — 7.00 × 9.00 × 2 دور<br>عميل — الهدا (استثماري) | الواجهة الأمامية والواجهة الشرقية | 1:50 | 2026-10-23 | A-04 (4/12) |

مصنع وتد الأخشاب
Watad Wood Factory

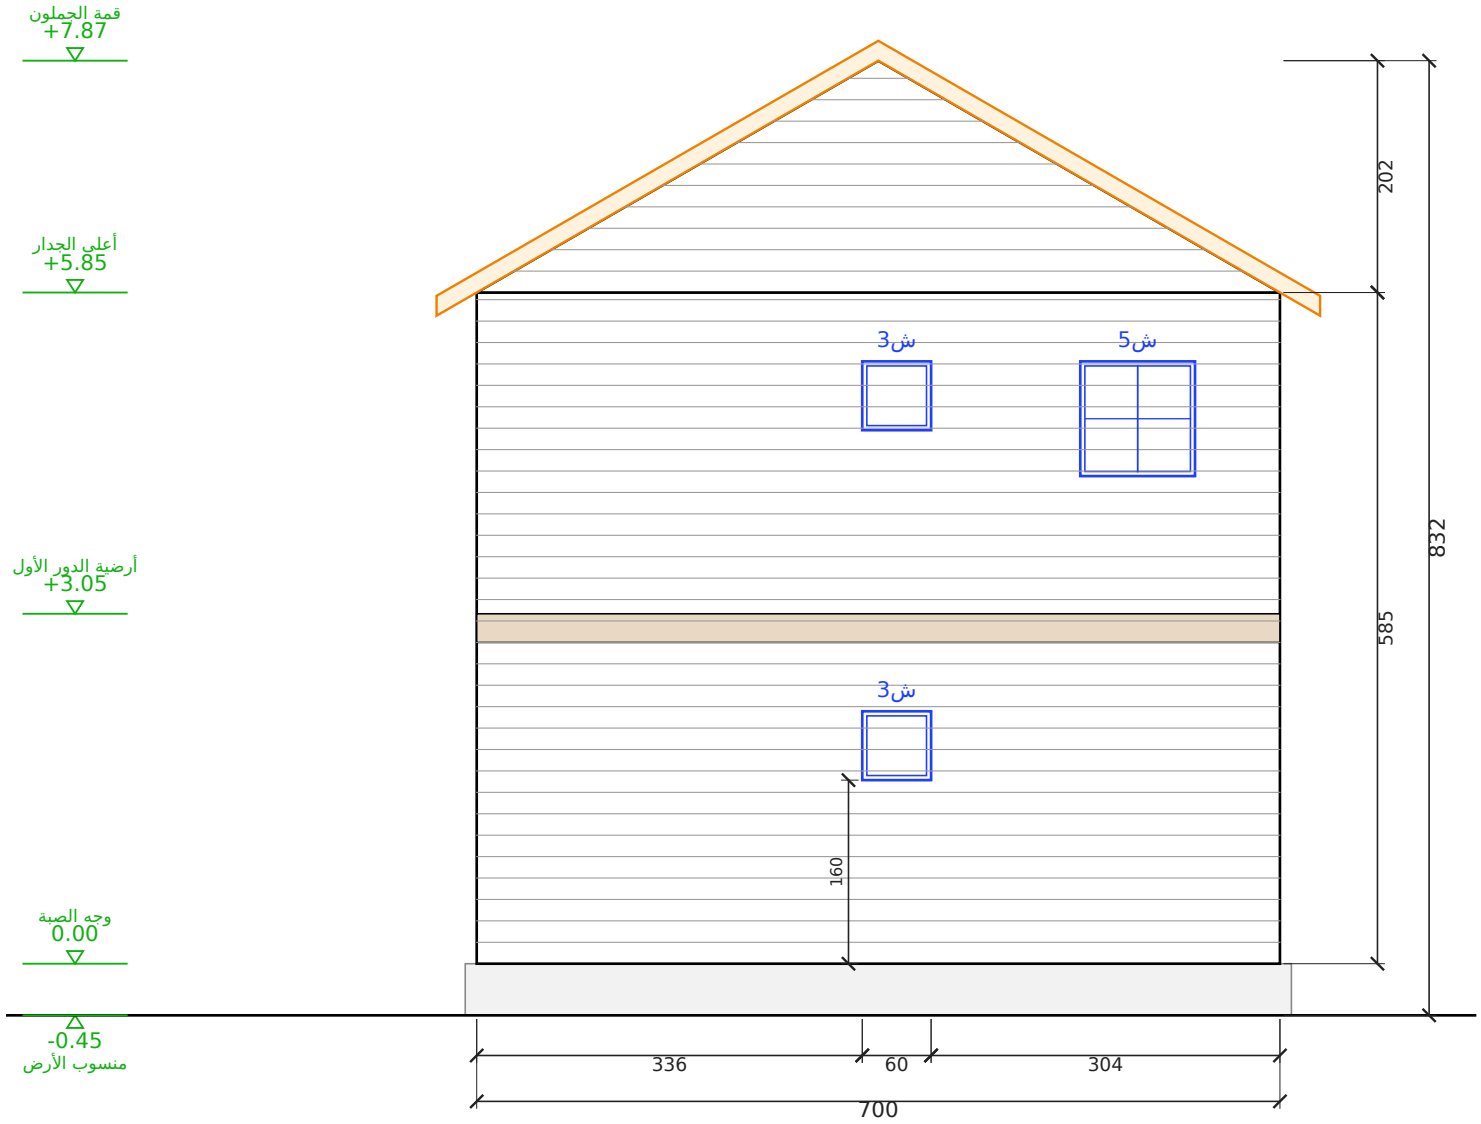


## الواجهة الخلفية

مقياس 1:50 | الوحدة: سم

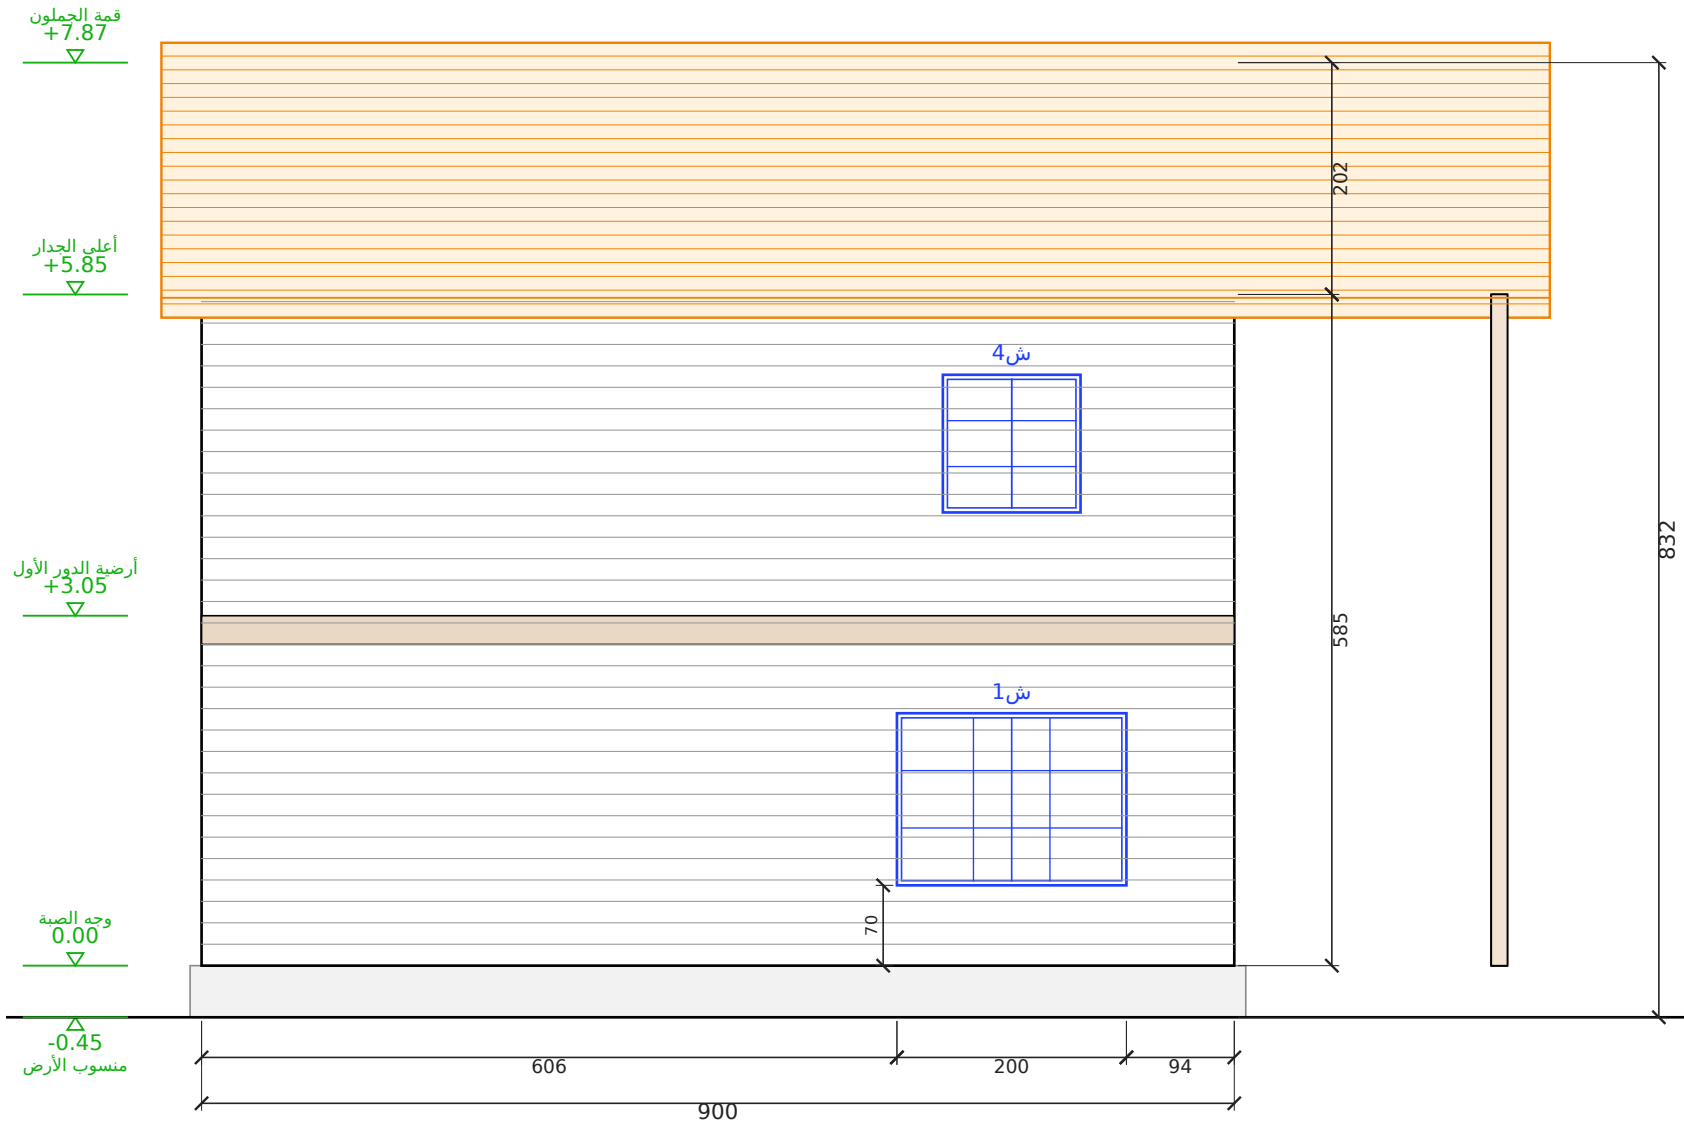



## الواجهة الغربية

مقياس 1:50 | الوحدة: سم


| المشروع / العميل | عنوان اللوحة | المقياس | التاريخ | رقم اللوحة |
|---|---|---|---|---|
| شاليهين الهدا الاستثماري — دورين — غرفتين وصالة لكل شاليه — 7.00 × 9.00 × 2 دور<br>عميل — الهدا (استثماري) | الواجهة الخلفية والواجهة الغربية | 1:50 | 2026-10-23 | A-05 (5/12) |

مصنع وتد الأخشاب
Watad Wood Factory


## مسقط السقف (جملون)
رفرف 35 سم من كل جهة | مقياس 1:50

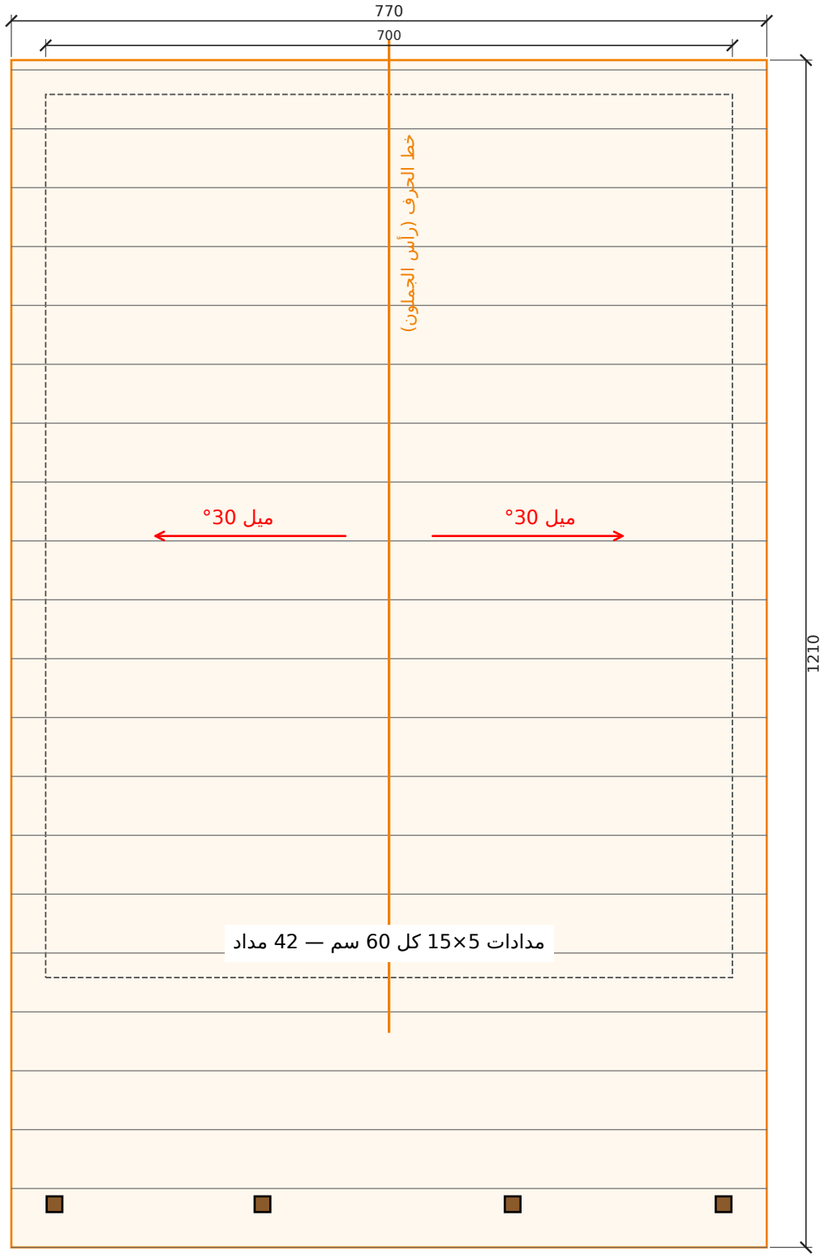


## قطاع عرضي أ-أ
مقياس 1:50 | الوحدة: سم

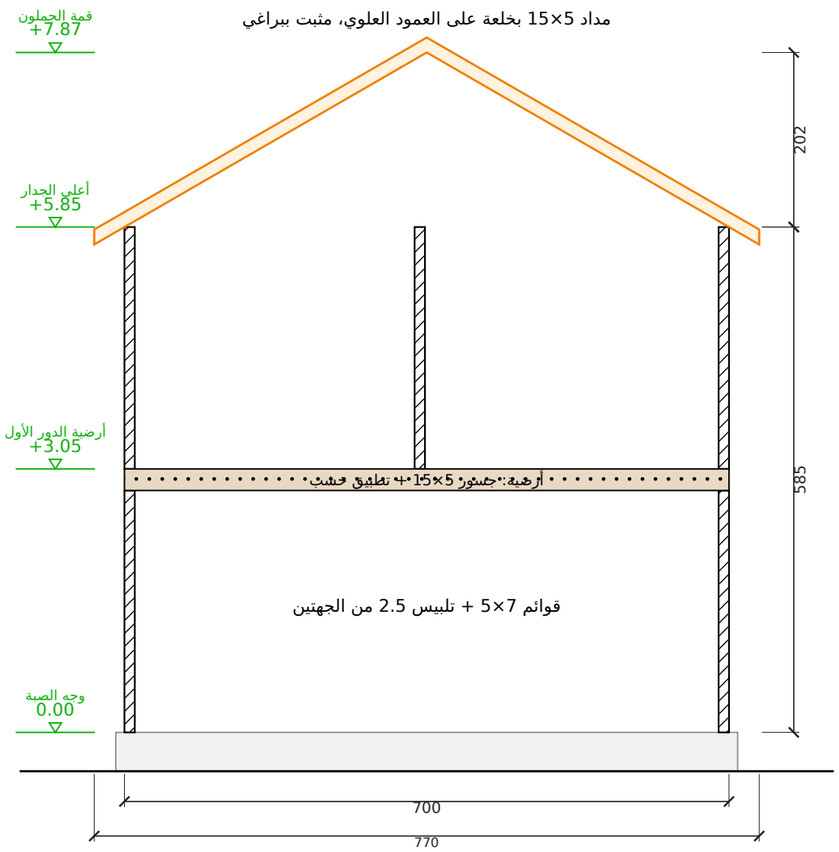


تفصيلة جلوس المداد على العلوي (1:5)

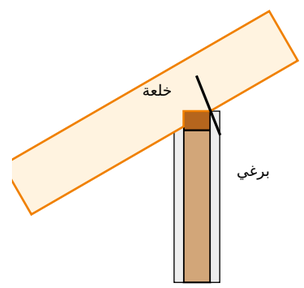


علوي 7×5 على قائم 7×5

| | | | | |
|---|---|---|---|---|
| المشروع / العميل | عنوان اللوحة | المقياس | التاريخ | رقم اللوحة |
| شاليهين الهدا الاستثماري — دورين — غرفتين وصالة لكل شاليه — 9.00 × 7.00 × 2 دور<br>عميل — الهدا (استثماري) | مسقط السقف والقطاع | 1:50 | 2026-10-23 | A-06 (6/12) |

مصنع وتد الأخشاب
Watad Wood Factory

# جدول مقاسات الأبواب والشبابيك
## مقاس الفتحة الصافي في الجدار - الوحدة: سم

| الرمز | النوع | العرض (سم) | الارتفاع (سم) | ارتفاع الجلسة (سم) | العدد | الموقع |
|---|---|---|---|---|---|---|
| ب1 | باب مزدوج | 230 | 240 | - | 2 | الأمامية 2 |
| ب2 | باب | 100 | 240 | - | 1 | الأمامية |
| ب3 | باب | 70 | 210 | - | 1 | حمام الصالة |
| ب4 | باب مزدوج | 220 | 220 | - | 1 | الأمامية (على البلكونة) |
| ب4 | باب مزدوج | 230 | 220 | - | 1 | الأمامية (على البلكونة) |
| ب5 | باب | 70 | 210 | - | 1 | غرفة نوم 2 |
| ب6 | باب | 80 | 210 | - | 1 | الماستر |
| ب7 | باب | 80 | 210 | - | 1 | غرفة الملابس |
| ب8 | باب | 70 | 210 | - | 1 | الحمام |
| ب9 | باب | 70 | 210 | - | 1 | حمام الماستر |
| ف1 | باب | 410 | 220 | - | 1 | فتحة الموزع والدرج |
| ف2 | باب | 200 | 220 | - | 1 | فتحة المطبخ |
| ش1 | شباك | 140 | 140 | 80 | 1 | الشرقية |
| ش1 | شباك | 200 | 150 | 70 | 1 | الغربية |
| ش2 | شباك | 120 | 100 | 110 | 1 | الشرقية |
| ش3 | شباك | 60 | 60 | 160 | 3 | الخلفية 2 - الشرقية |
| ش4 | شباك | 120 | 120 | 90 | 2 | الشرقية - الغربية |
| ش5 | شباك | 100 | 100 | 120 | 1 | الخلفية |

الإجمالي: أبواب 13 - شبابيك 9

# جدول المساحات وبيانات المشروع والتسعير

## بيانات المشروع

| البند | البيان |
|---|---|
| المشروع | شاليهين الهدا الاستثماري — دورين — غرفتين وصالة لكل شاليه — 7.00 × 9.00 × 2 دور |
| العميل | عميل — الهدا (استثماري) |
| الموقع | الهدا — الطائف |
| الاستخدام | شاليهين استثماري (تأجير) |
| التاريخ | 2026-10-23 |
| نظام البناء | هيكل خشب 7×5 + تلبيس 2.5 سم من الجهتين |
| السقف | جملون 30° — قرميد معدني |

## جدول المساحات

| م | الفراغ | الأبعاد (م) | المساحة (م2) |
|---|---|---|---|
| 1 | أرضي — الصالة | 6.76 × 4.48 | 30.28 |
| 2 | أرضي — الموزع | 4.38 × 0.92 | 4.03 |
| 3 | أرضي — الدرج | 2.28 × 3.00 | 6.84 |
| 4 | أرضي — حمام الصالة | 1.98 × 3.12 | 6.18 |
| 5 | أرضي — المطبخ | 2.26 × 4.16 | 9.40 |
| 6 | أول — غرفة نوم 2 | 3.24 × 4.48 | 14.52 |
| 7 | أول — الماستر | 3.40 × 4.48 | 15.23 |
| 8 | أول — الممر | 4.38 × 0.92 | 4.03 |
| 9 | أول — الحمام (لغرفة 2) | 1.98 × 3.12 | 6.18 |
| 10 | أول — غرفة الملابس | 2.26 × 1.68 | 3.80 |
| 11 | أول — حمام الماستر | 2.26 × 2.36 | 5.33 |
| | المساحة الصافية الداخلية | | 105.82 |
| | **التراس** | **7.00 × 2.40** | **16.80** |
| | **البلكونة** | **7.00 × 2.40** | **16.80** |
| | **المساحة الإجمالية المبنية** | **7.00 × 9.00 × 2 دور** | **126.00** |
| | **المساحة الكلية (المبنية + التراس والبلكونة)** | | **159.60** |

## التسعير المفصّل


| البند | المبلغ (ريال) |
|---|---|
| الكوخ المبني 126.00 م² × 1,096 | 138,096 |
| تراس الأرضي + بلكونة الأول للشاليه الأول (7.00 × 2.40 × 2) — 33.60 م² × 1,096 | 36,826 |
| الشاليه الثاني (مطابق — 126 م² + تراس وبلكونة 33.6 م²) — 159.60 م² × 1,096 | 174,922 |
| **الإجمالي (ريال)** | **349,843** |

**ملاحظات:**


- السعر للشاليهين (الدورين) والتراسات والبلكونات حسب المخطط المعتمد — التراس يُسعّر بنفس سعر متر الكوخ.
- أعمال الموقع (السور والبوابات والمسابح والجلسات الشتوية والبلاط والزراعة) عن طريق المقاول وتُسعّر منفصلة.
- الصبة والتمديدات الخارجية على العميل ما لم يُذكر غير ذلك.

# لقطات المنظور الخارجي


المنظور الأمامي

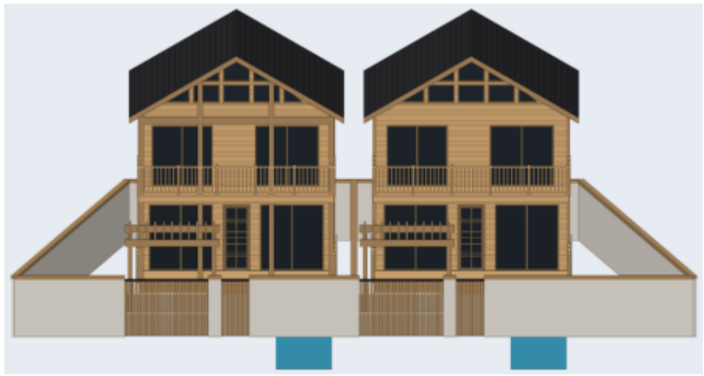


منظور أمامي من اليسار

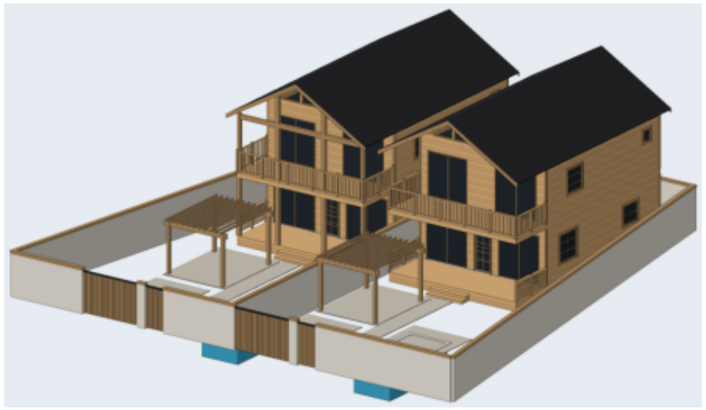


منظور أمامي من اليمين

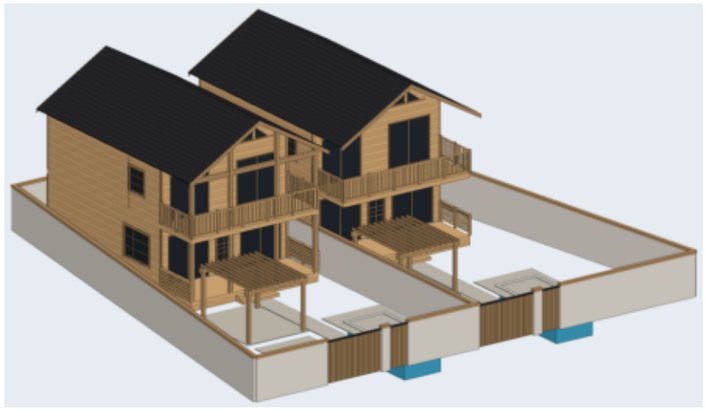


المنظور الخلفي

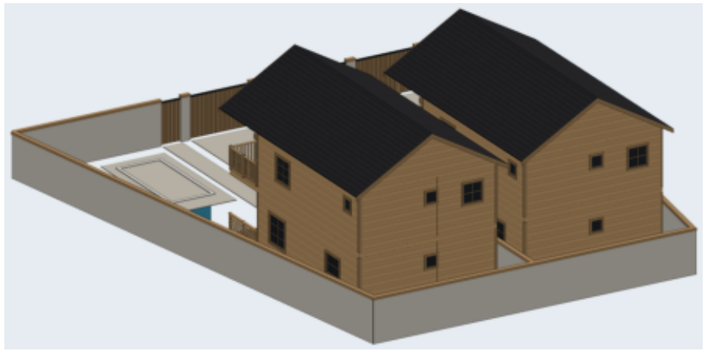

منظور خلفي من اليمين

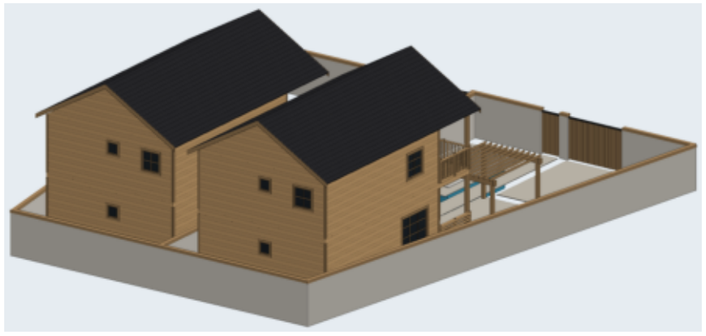


منظر علوي

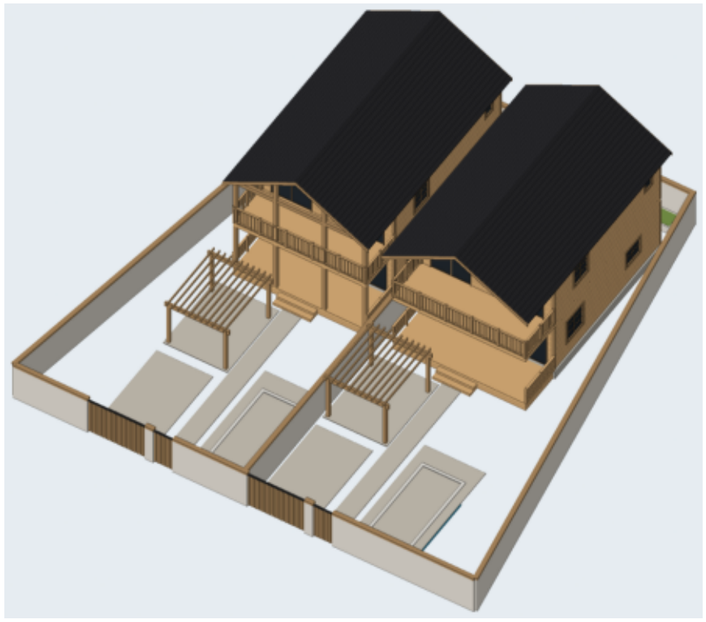

| | | | | |
|---|---|---|---|---|
| **مصنع وتد الأخشاب**<br>Watad Wood Factory | المشروع / العميل<br>**شاليهين الهدا الاستثماري — دورين — غرفتين وصالة لكل شاليه — 9.00 × 7.00 × 2 دور**<br>**عميل — الهدا (استثماري)** | عنوان اللوحة<br>**لقطات المنظور** | المقياس<br>**—** | التاريخ<br>**2026-10-23** | رقم اللوحة<br>**A-09 (9/12)** |

# المقطع العلوي بالفرش — الدور الأرضي


مقطع أفقي على ارتفاع 1.90 م — توزيع الفرش ومسار الحركة

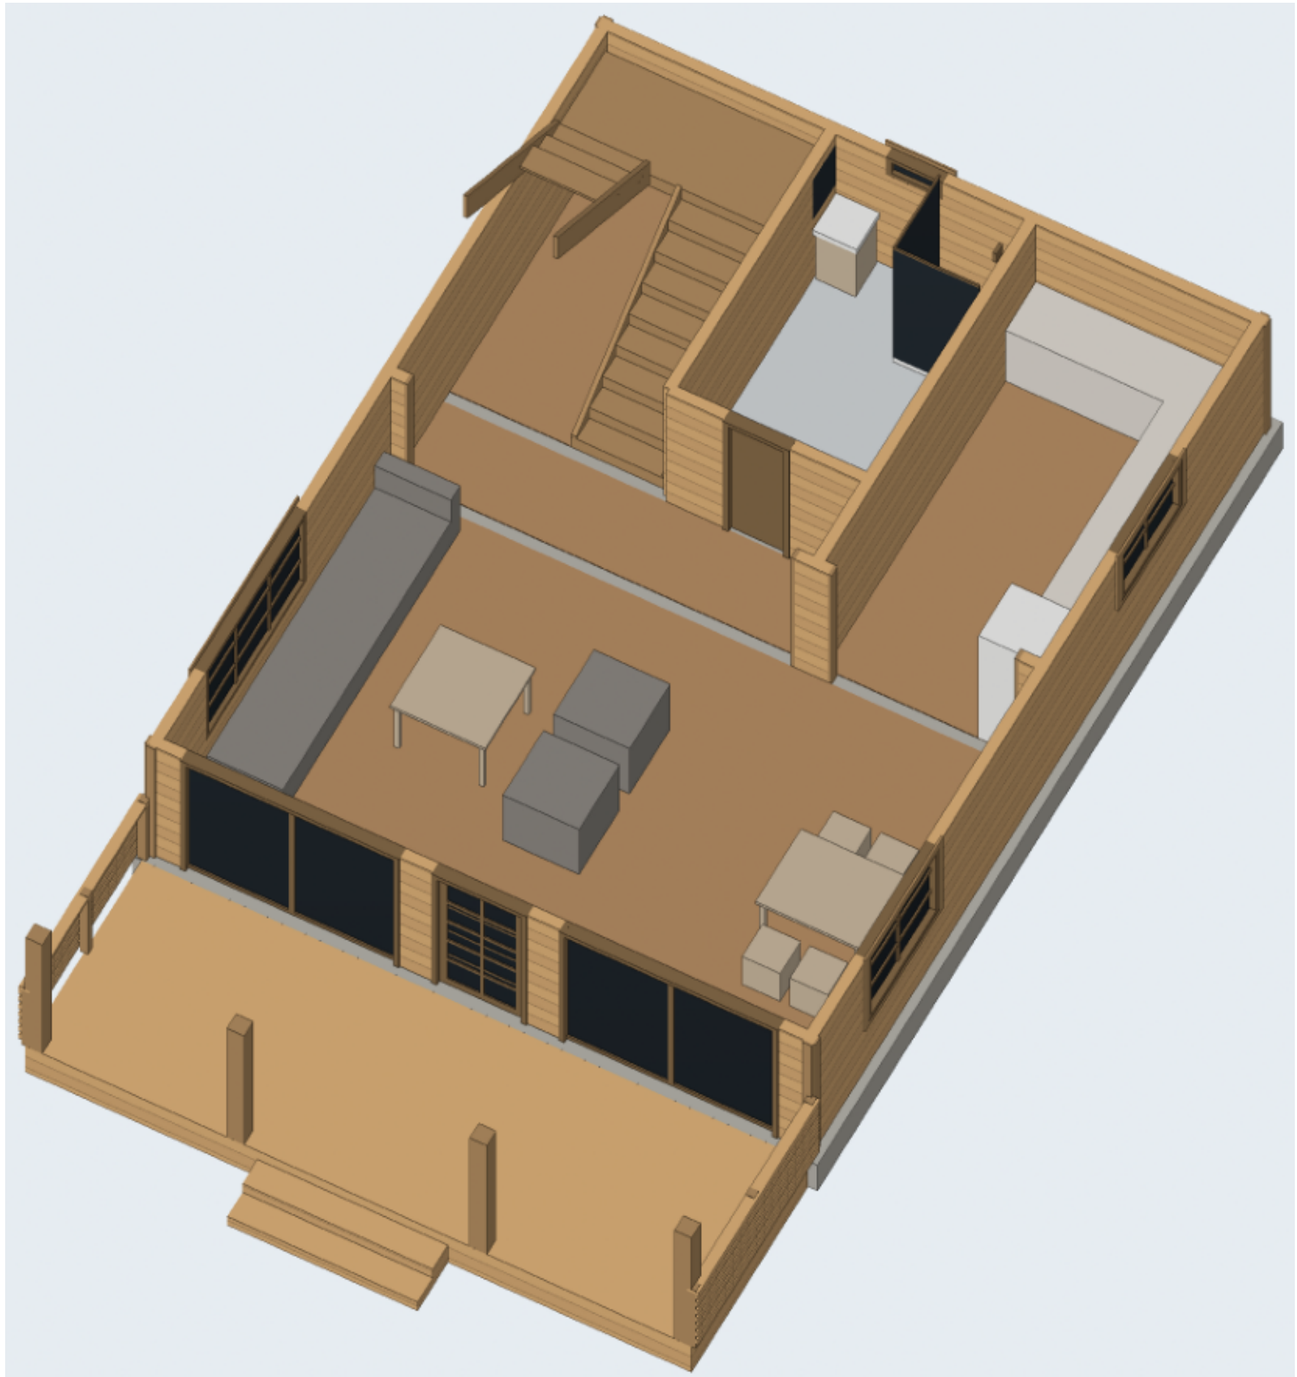

| | | | | | |
|---|---|---|---|---|---|
| مصنع وتد الأخشاب<br>Watad Wood Factory | المشروع / العميل<br>شاليهين الهدا الاستثماري — دورين — غرفتين وصالة لكل شاليه — 9.00 × 7.00 × 2 دور<br>عميل — الهدا (استثماري) | عنوان اللوحة<br>المقطع العلوي بالفرش — الدور الأرضي | المقياس<br>— | التاريخ<br>2026-10-23 | رقم اللوحة<br>A-10 (10/12) |

# المقطع العلوي بالفرش — الدور الأول


مقطع أفقي على ارتفاع 1.90 م — توزيع الفرش ومسار الحركة

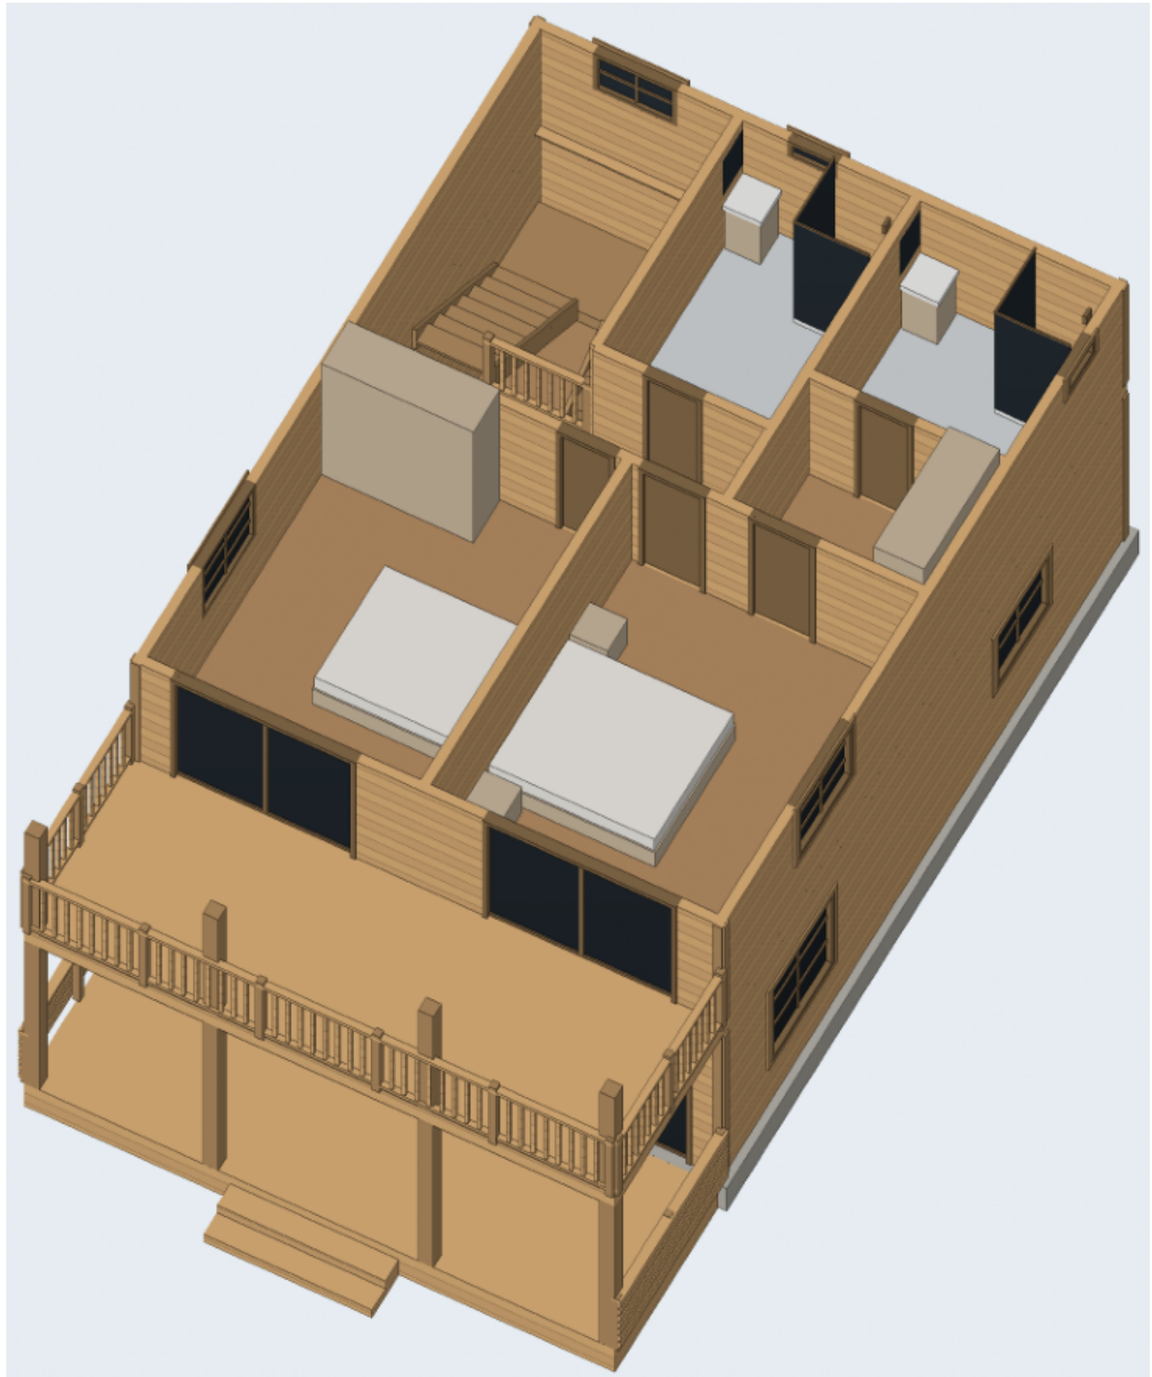

| | | | | | |
|---|---|---|---|---|---|
| مصنع وتد الأخشاب<br>Watad Wood Factory | المشروع / العميل<br>شاليهين الهدا الاستثماري — دورين — غرفتين وصالة لكل شاليه — 9.00 × 7.00 × 2 دور<br>عميل — الهدا (استثماري) | عنوان اللوحة<br>المقطع العلوي بالفرش — الدور الأول | المقياس<br>— | التاريخ<br>2026-10-23 | رقم اللوحة<br>A-11 (11/12) |

# المنظور ثلاثي الأبعاد والمواد

النمط: جوزي غامق + إطارات سوداء — رندر واقعي بخامات حقيقية

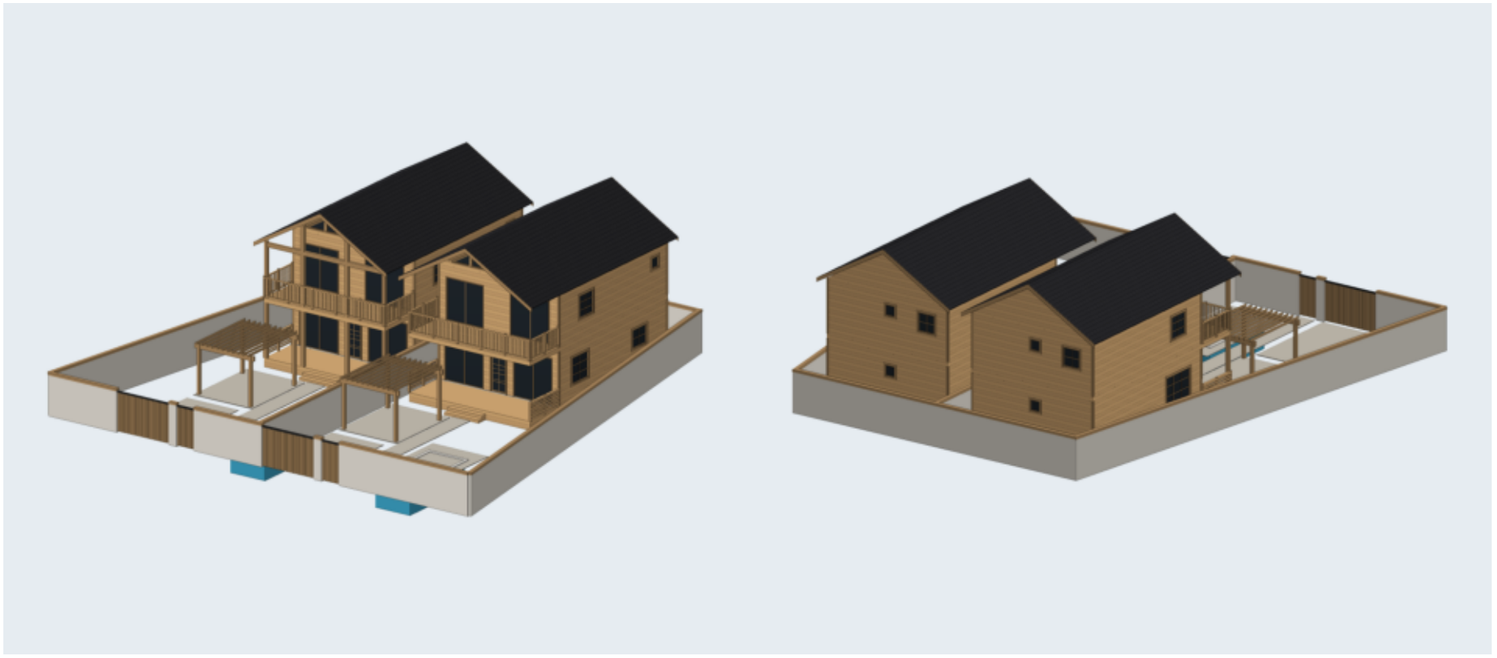

## جدول المواد والألوان

**الخشب / الصبغة**

خشب طبيعي فاتح (بدون صبغة)

**القرميد**

قرميد رمادي غامق

**الزجاج**

زجاج عاكس غامق

**إطارات الشبابيك والأبواب**

إطار خشب بنفس الصبغة أغمق

**الكنار والزوايا**

نفس الصبغة أغمق درجة


**الصبة**

خرسانة 45 سم


الدربزين: ألواح أفقية متقاربة (عصري)

تقسيم الشبابيك: بدون | الباب الرئيسي: سحاب زجاج

## أنواع الدربزين المعتمدة (من مشاريع المصنع)

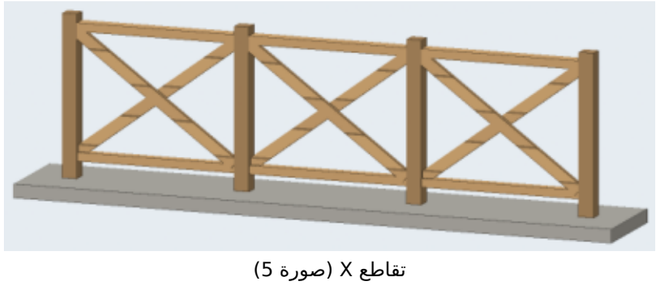

تقاطع X (صورة 5)

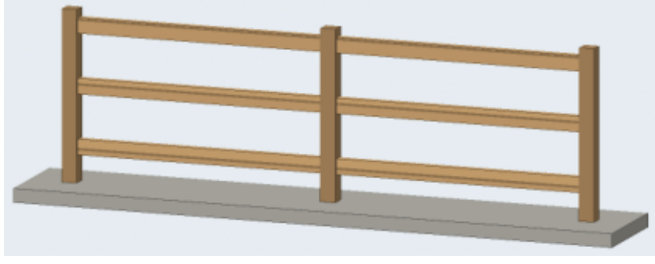

3 مرابيع أفقية (صورة 2)



قوائم رأسية متقاربة (صورة 1)

| المشروع / العميل | عنوان اللوحة | المقياس | التاريخ | رقم اللوحة |
|---|---|---|---|---|
| **شاليهين الهدا الاستثماري — دورين — غرفتين وصالة لكل شاليه — 9.00 × 7.00 × 2 دور**<br>**عميل — الهدا (استثماري)** | **المنظور والمواد** | **—** | **2026-10-23** | **A-12 (12/12)** |

**مصنع وتد الأخشاب**
Watad Wood Factory