
المسقط الأفقي مع الفرش — الدور الأرضي


الأبعاد بالسنتيمتر - الجدران: قوائم 7×5 + تلبيس 2.5 من الجهتين (12 سم) | منسوب الأرضية +0.00

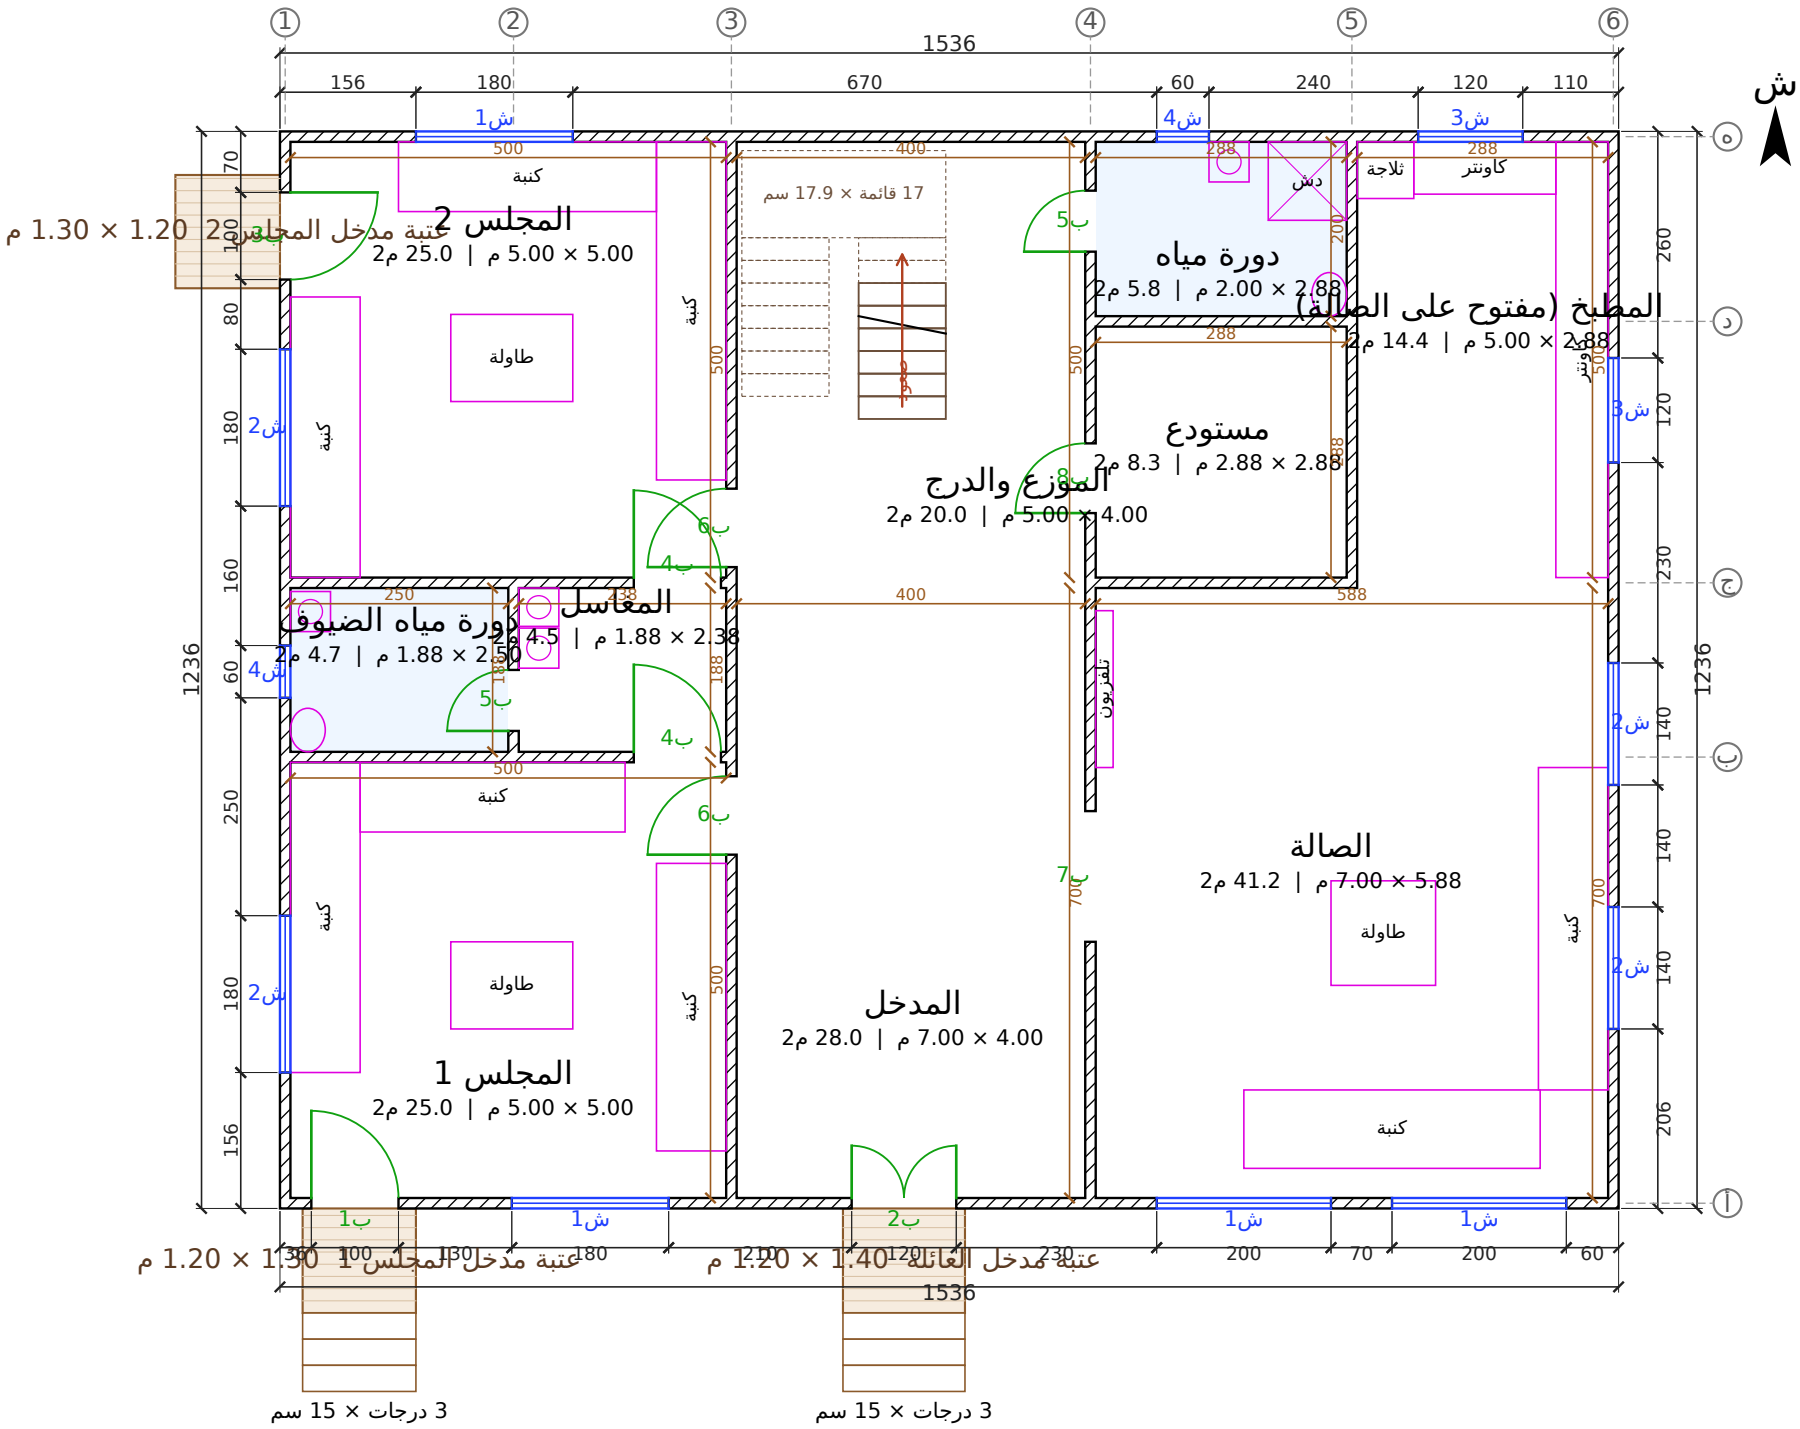


مصنع وتد الأخشاب Watad Wood Factory	المشروع / العميل الخيار 2 — مجلسين وصالة + 3 غرف — دورين بسطح علوي عميل — 3 خيارات	عنوان اللوحة المسقط الأفقي — الدور الأرضي	المقياس 1:50	التاريخ 2026-10-21	رقم اللوحة A-01 (1/11)

المسقط الأفقي مع الفرش — الدور الأول

الأبعاد بالسنتيمتر - الجدران: قوائم 5×7 + تلبيس 2.5 من الجهتين (12 سم) | منسوب الأرضية +3.05

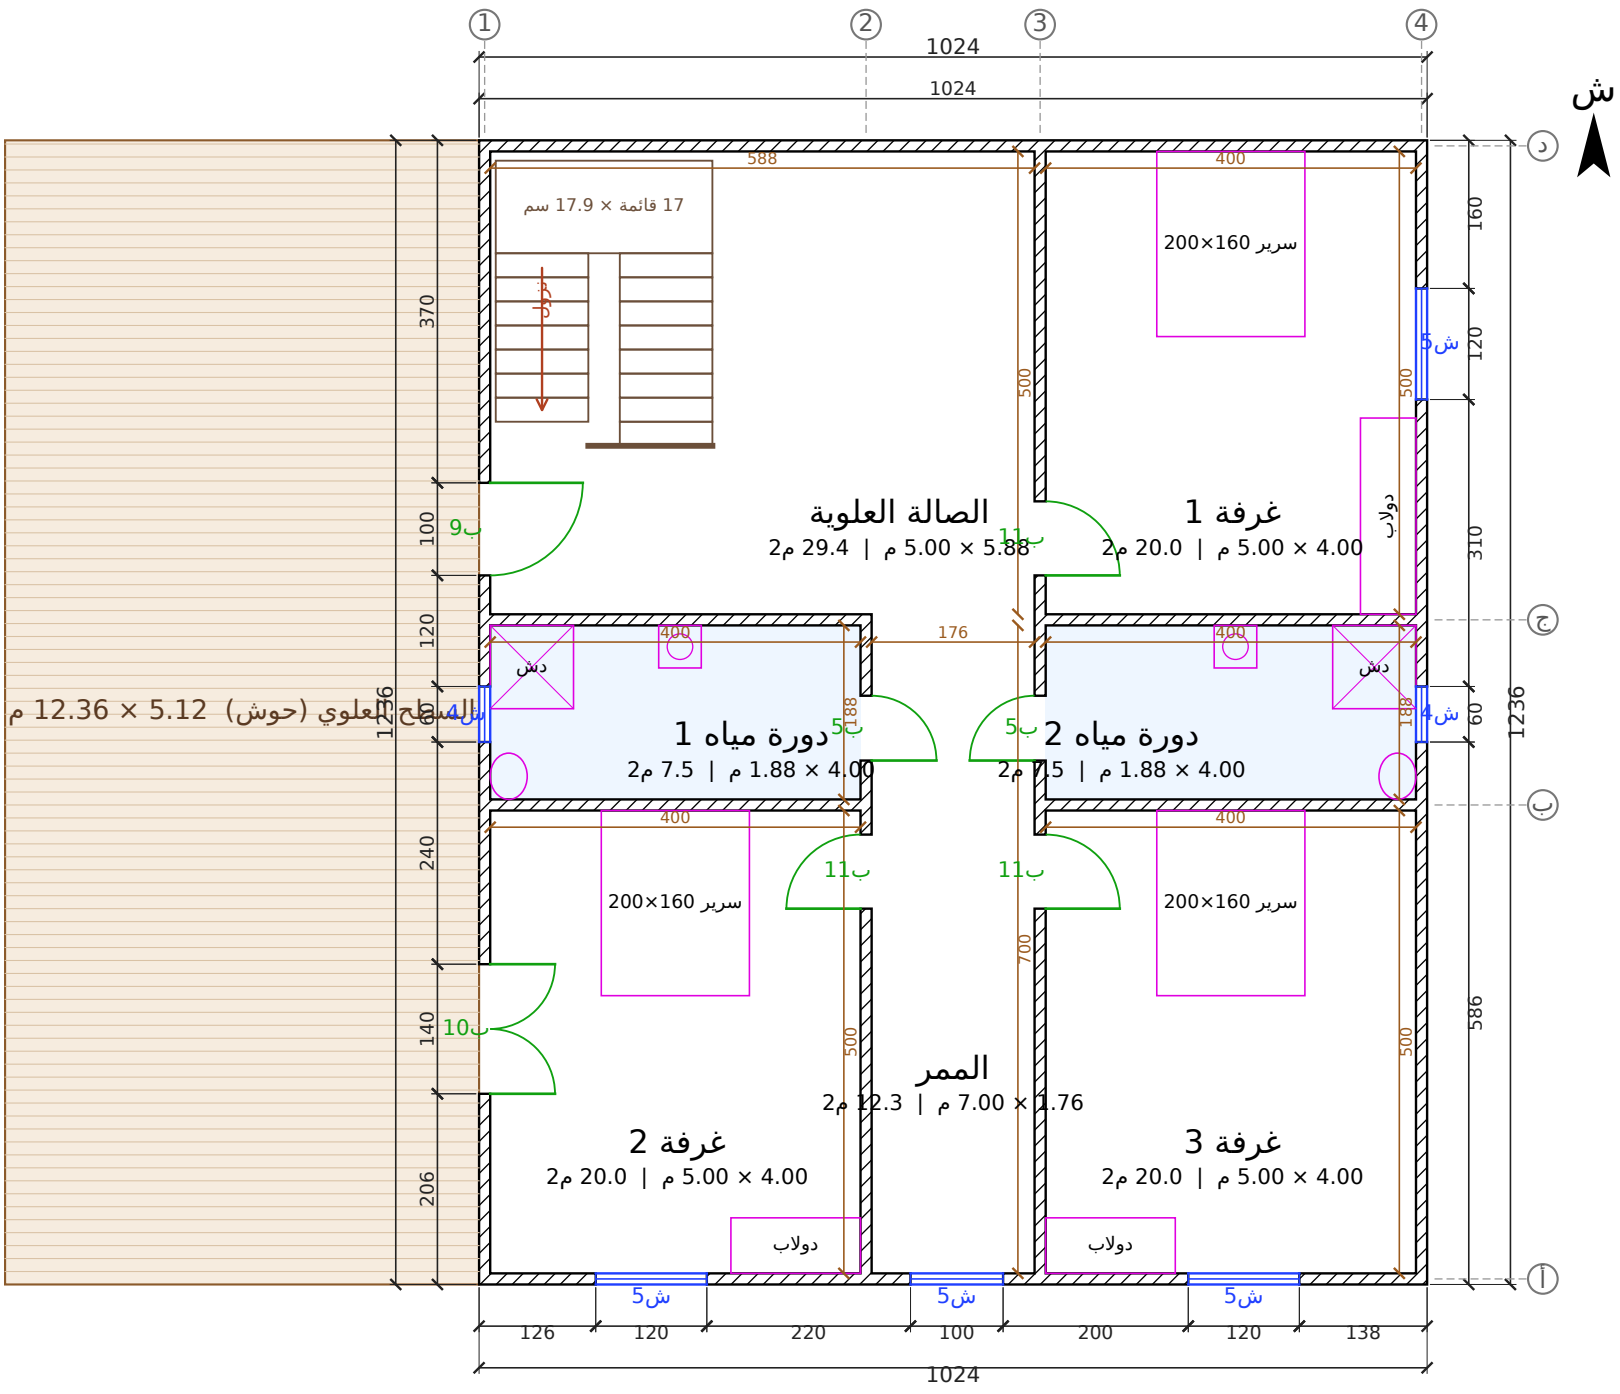


المشروع / العميل	عنوان اللوحة	المقياس	التاريخ	رقم اللوحة
مصنع وتد الأخشاب Watad Wood Factory **الخيار 2 — مجلسين وصالة + 3 غرف — دورين بسطح علوي** **عميل — 3 خيارات**	**المسقط الأفقي — الدور الأول**	**1:50**	**2026-10-21**	**A-02 (2/11)**

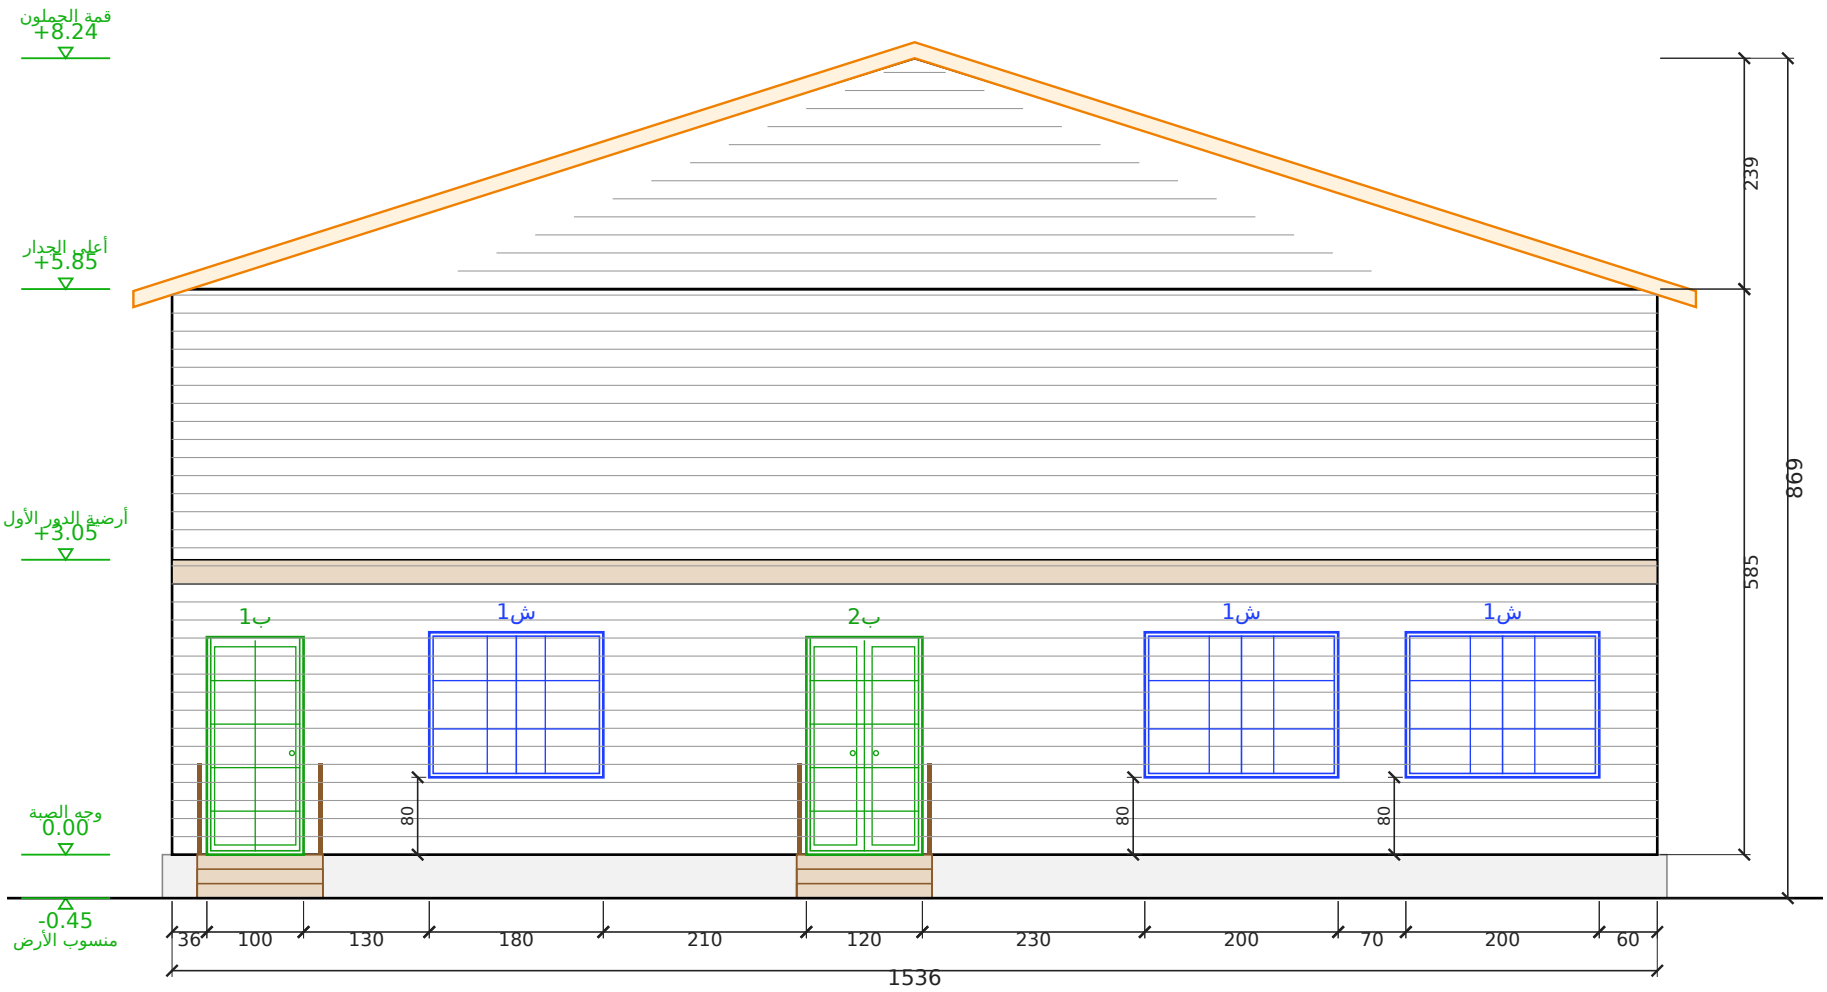

الواجهة الأمامية

مقياس 1:50 | الوحدة: سم

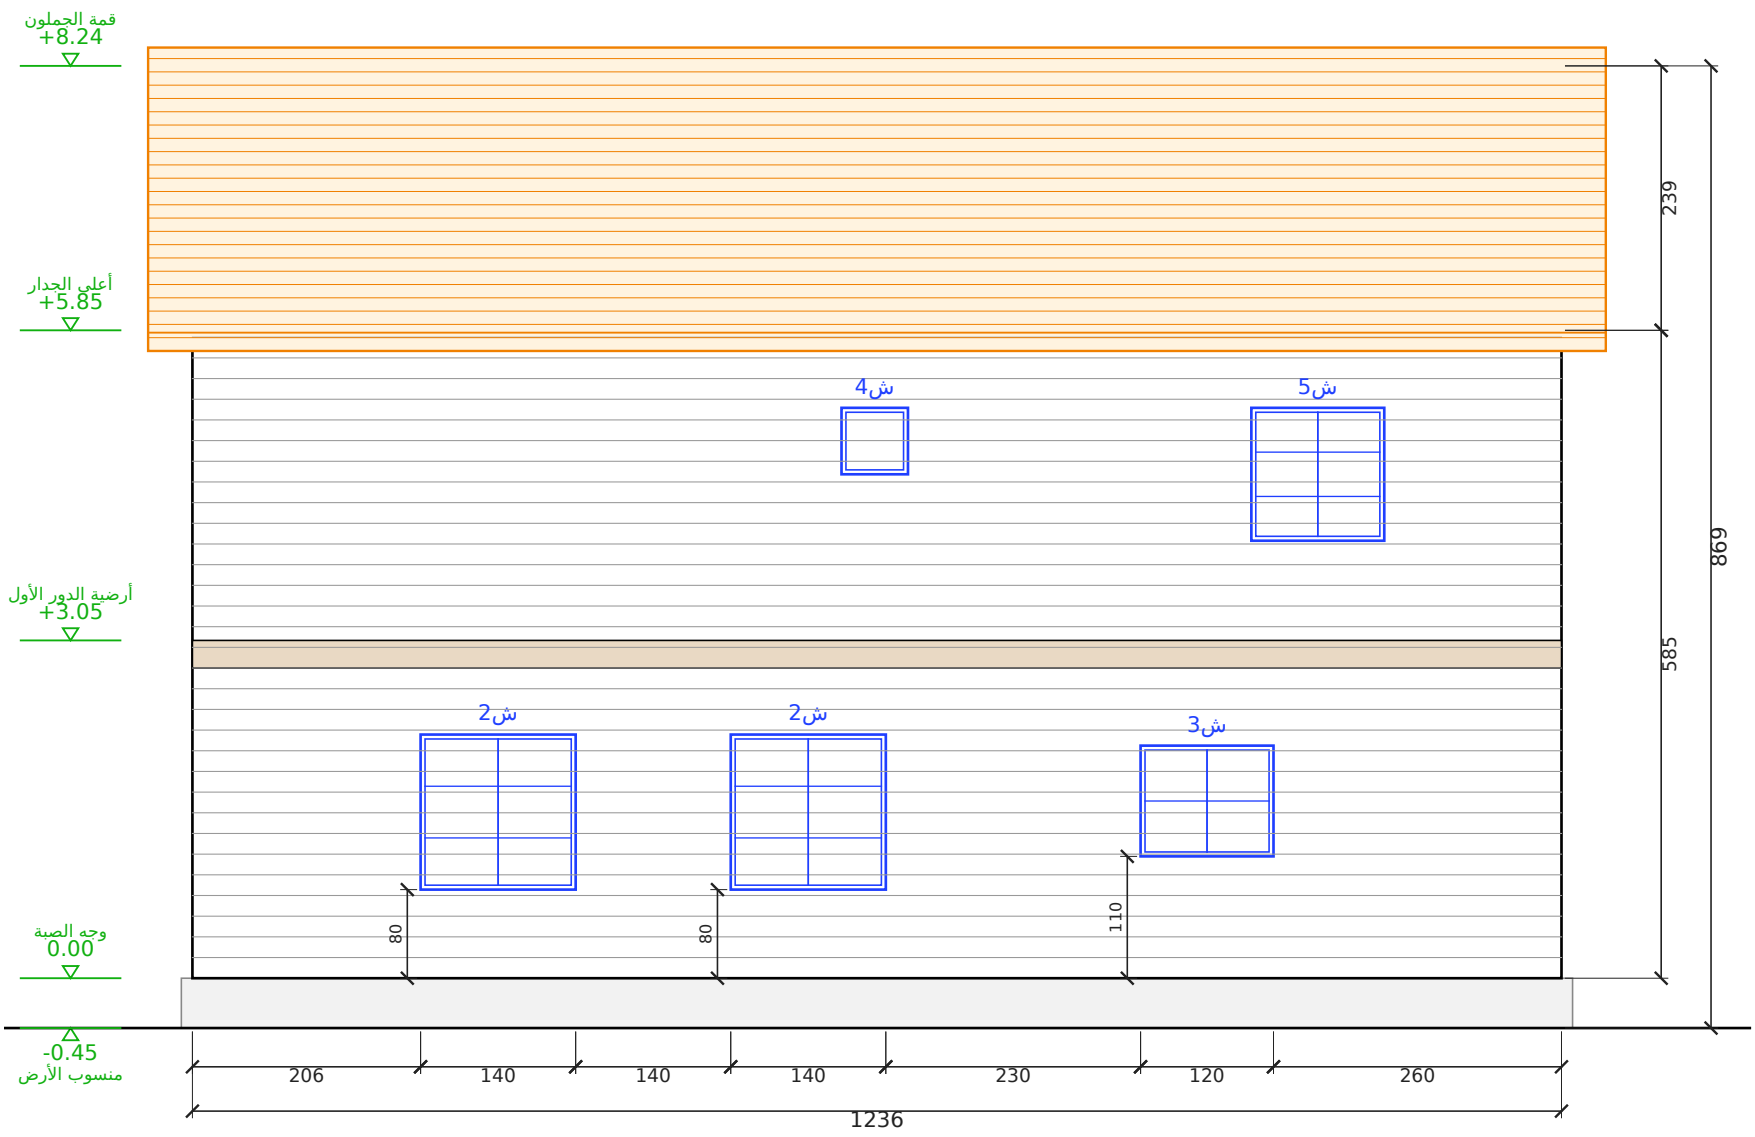


الواجهة الشرقية

مقياس 1:50 | الوحدة: سم


المشروع / العميل	عنوان اللوحة	المقياس	التاريخ	رقم اللوحة
الخيار 2 — مجلسين وصالة + 3 غرف — دورين بسطح علوي **عميل — 3 خيارات**	**الواجهة الأمامية والواجهة الشرقية**	**1:50**	**2026-10-21**	**A-03 (3/11)**

مصنع وتد الأخشاب
Watad Wood Factory

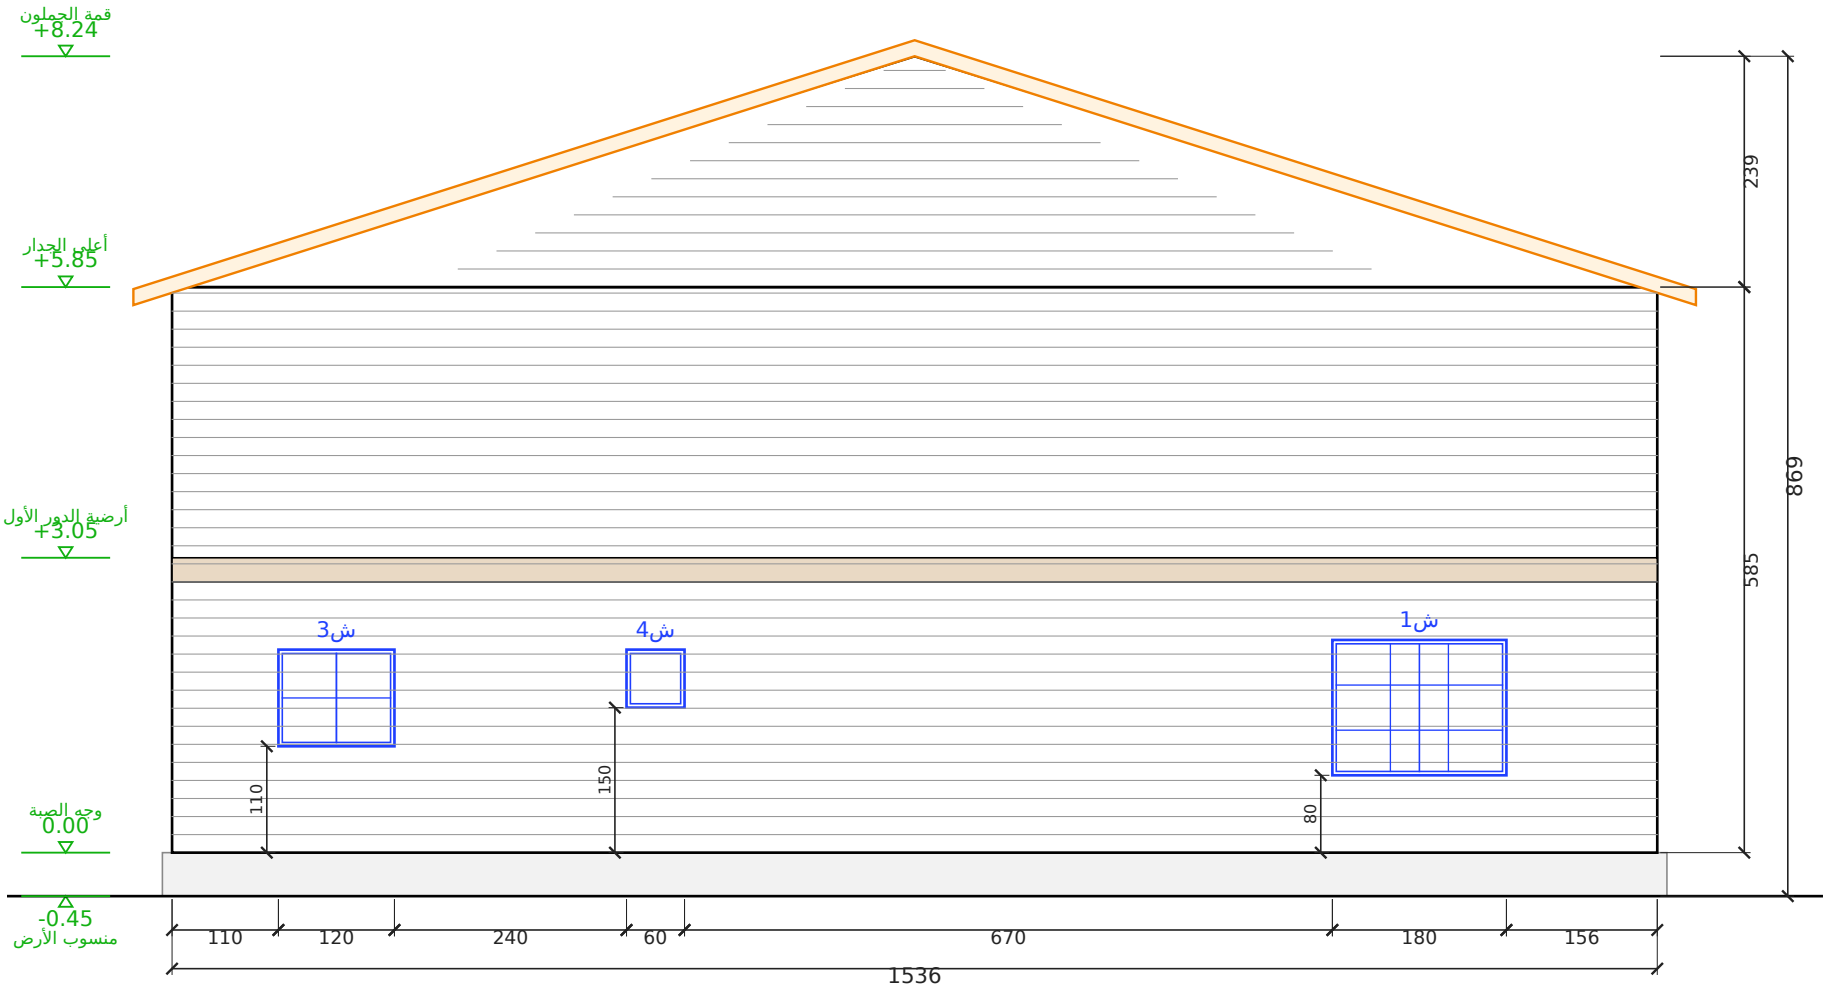

الواجهة الخلفية

مقياس 1:50 | الوحدة: سم

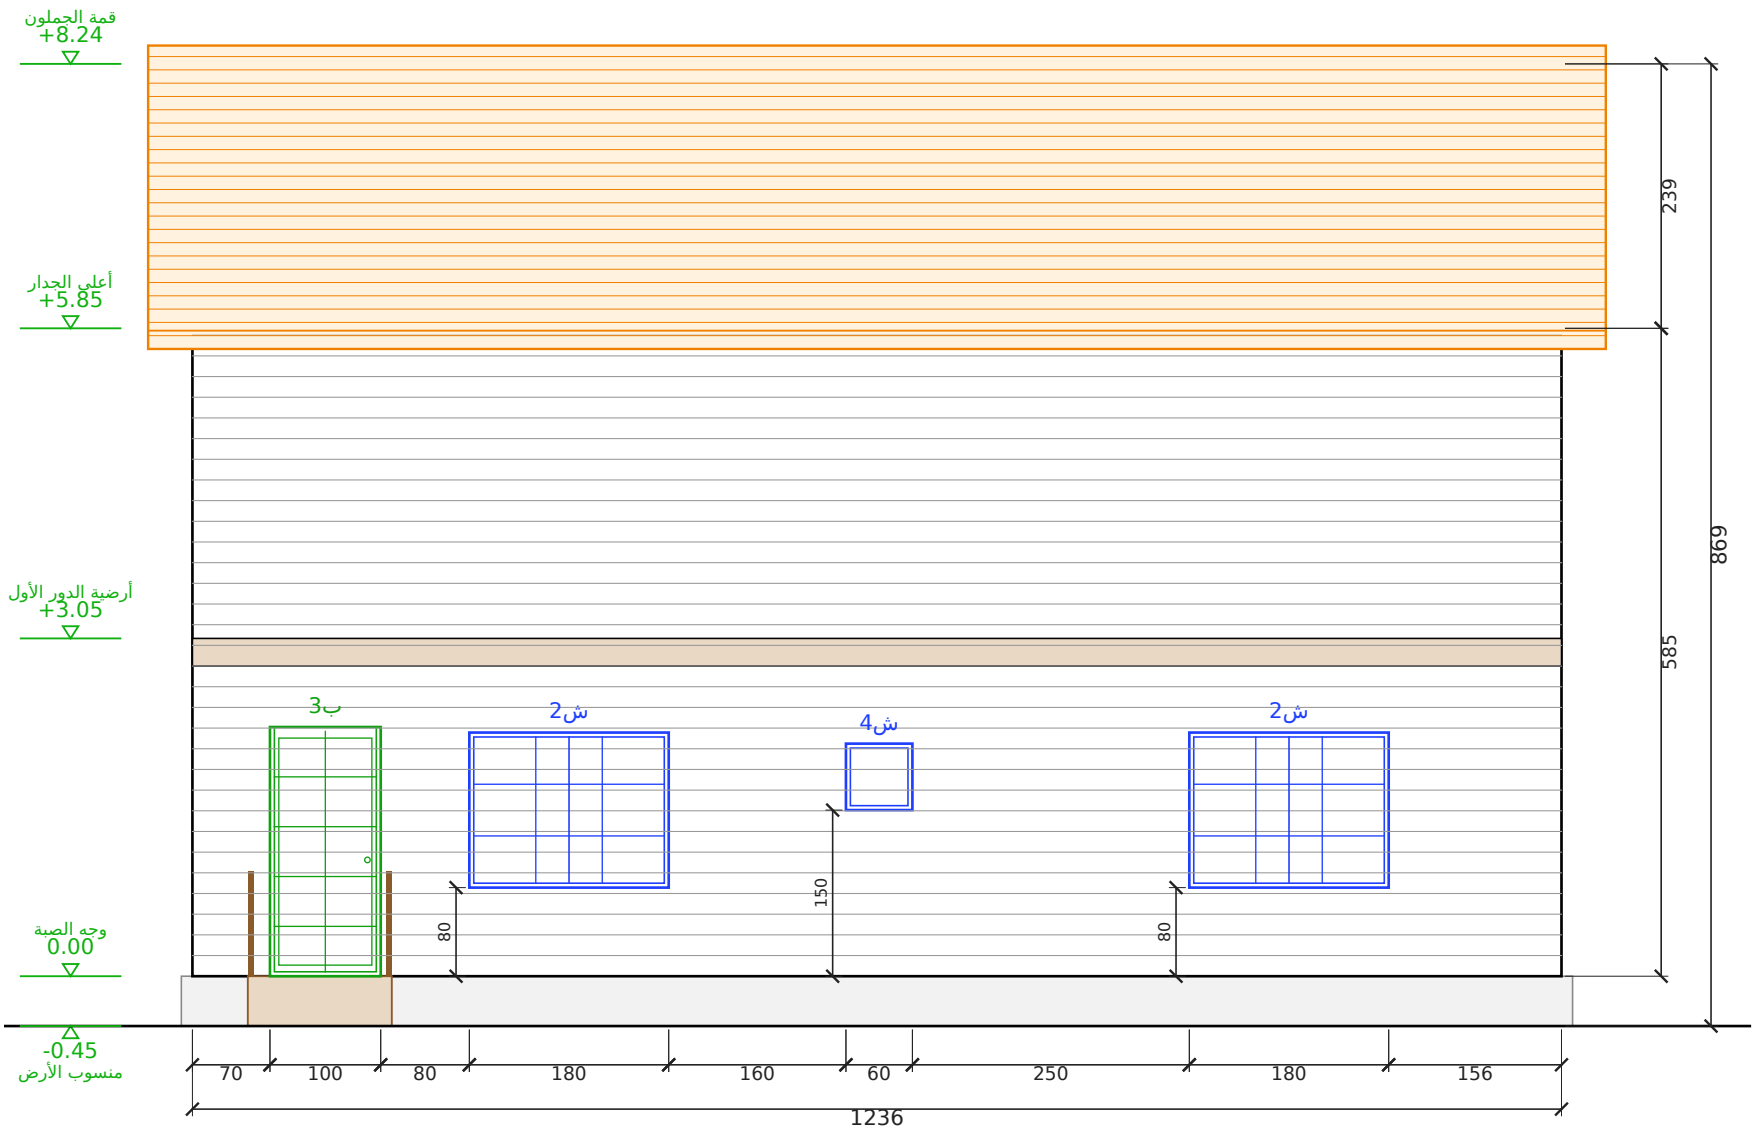


الواجهة الغربية

مقياس 1:50 | الوحدة: سم


المشروع / العميل	عنوان اللوحة	المقياس	التاريخ	رقم اللوحة
الخيار 2 — مجلسين وصالة + 3 غرف — دورين بسطح علوي **عميل — 3 خيارات**	**الواجهة الخلفية والواجهة الغربية**	**1:50**	**2026-10-21**	**A-04 (4/11)**

مصنع وتد الأخشاب
Watad Wood Factory


مسقط السقف (جملون)
رفرف 40 سم من كل جهة | مقياس 1:50

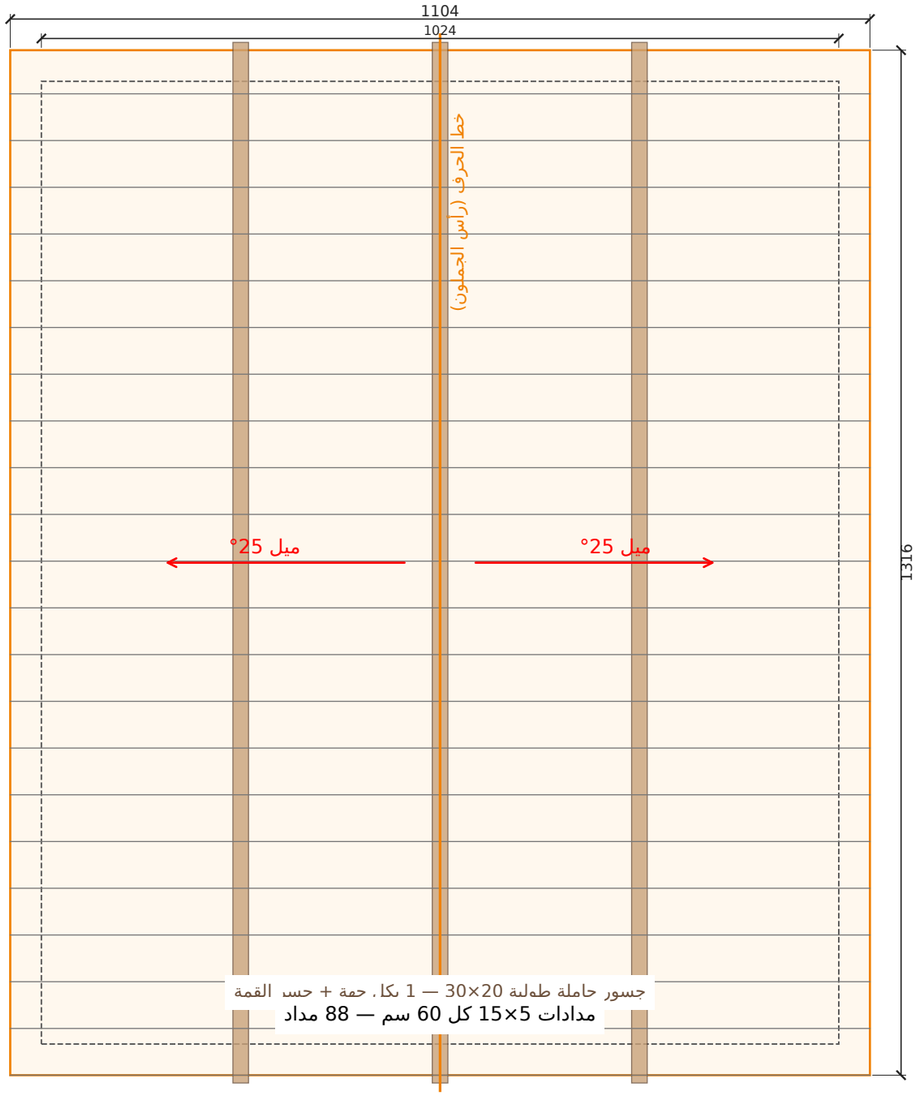

قطاع عرضي أ-أ
مقياس 1:50 | الوحدة: سم

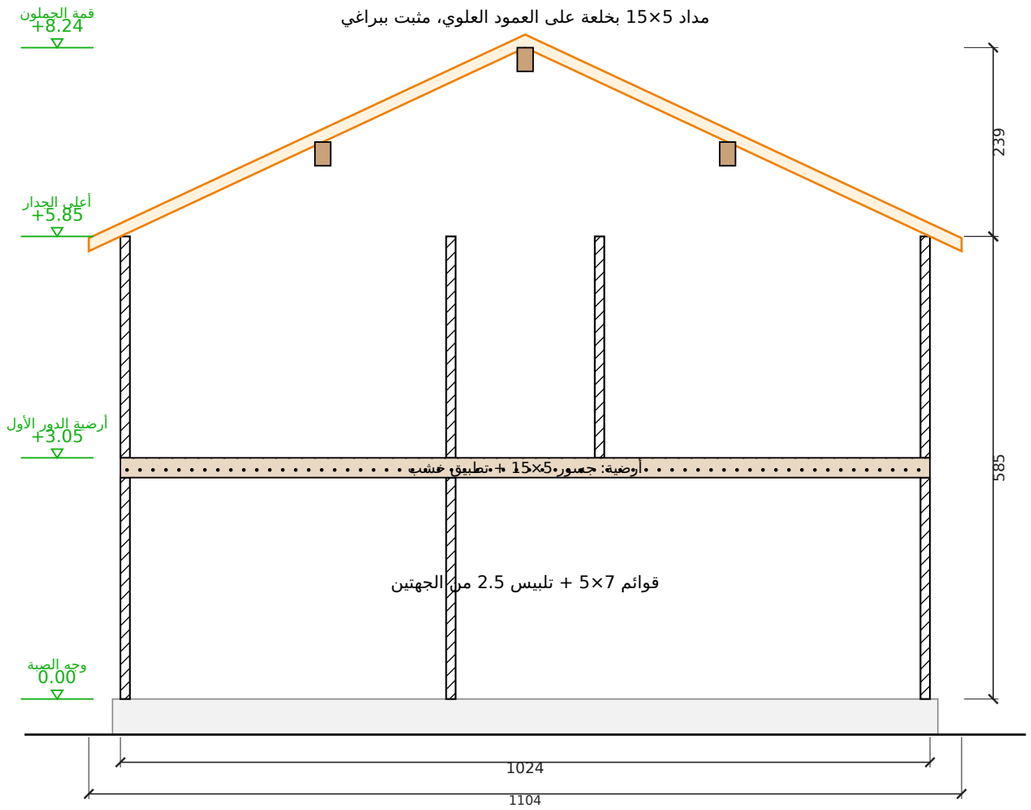

تفصيلة جلوس المداد على العلوي (1:5)

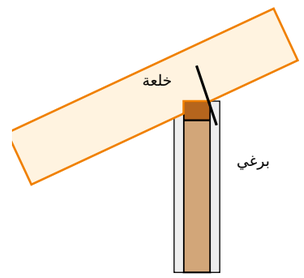

علوي 7×5 على قائم 7×5

المشروع / العميل **الخيار 2 — مجلسين وصالة + 3 غرف — دورين بسطح علوي** **عميل — 3 خيارات**	عنوان اللوحة **مسقط السقف والقطاع**	المقياس **1:50**	التاريخ **2026-10-21**	رقم اللوحة **A-05 (5/11)**

مصنع وتد الأخشاب
Watad Wood Factory

جدول مقاسات الأبواب والشبابيك
مقاس الفتحة الصافي في الجدار - الوحدة: سم

الرمز	النوع	العرض (سم)	الارتفاع (سم)	ارتفاع الجلسة (سم)	العدد	الموقع
ب1	باب	100	225	-	1	الأمامية
ب10	باب مزدوج	140	220	-	1	الغربية (على السطح)
ب11	باب	80	210	-	3	غرفة 2 - غرفة 3 - غرفة 1
ب2	باب مزدوج	120	225	-	1	الأمامية
ب3	باب	100	225	-	1	الغربية
ب4	باب	100	210	-	2	المجلس 1 — المغاسل - المجلس 2 — المغاسل
ب5	باب	70	210	-	4	دورة مياه الضيوف - دورة مياه - دورة مياه 1 - دورة مياه 2
ب6	باب	90	210	-	2	المجلس 1 — المدخل - المجلس 2 — الموزع
ب7	باب	150	210	-	1	فتحة المدخل — الصالة
ب8	باب	80	210	-	1	المستودع
ب9	باب	100	220	-	1	الغربية (على السطح)
ش1	شباك	180	150	80	1	الأمامية
ش1	شباك	200	150	80	2	الأمامية 2
ش1	شباك	180	140	80	1	الخلفية
ش2	شباك	140	140	80	2	الشرقية 2
ش2	شباك	180	140	80	2	الغربية 2
ش3	شباك	120	100	110	2	الشرقية - الخلفية
ش4	شباك	60	60	150	4	الخلفية - الغربية - الشرقية - الغربية (على السطح)
ش5	شباك	120	120	90	3	الأمامية 2 - الشرقية
ش5	شباك	100	120	90	1	الأمامية

الإجمالي: أبواب 18 - شبابيك 18

جدول المساحات وبيانات المشروع والتسعير

بيانات المشروع

البند	البيان
المشروع	الخيار 2 — مجلسين وصالة + 3 غرف — دورين بسطح علوي
العميل	عميل — 3 خيارات
الموقع	—
الاستخدام	سكن
التاريخ	2026-10-21
نظام البناء	هيكل خشب 5×7 + تلبيس 2.5 سم من الجهتين
السقف	جملون 25° — قرميد معدني

التسعير

البند	القيمة
المساحة المبنية (م2)	316.42
سعر المتر المربع	1,096 ريال
الإجمالي	**346,796 ريال**

ملاحظات:

- السعر على المساحة المبنية للدورين بسعر المصنع 1,096 ريال/م².
- السطح العلوي (حوش) 63 م² يُسعّر منفصل (أرضية + عزل مائي + دربزين).

جدول المساحات

م	الفراغ	الأبعاد (م)	المساحة (م2)
1	أرضي — المجلس 1	5.00 × 5.00	25.00
2	أرضي — دورة مياه الضيوف	2.50 × 1.88	4.70
3	أرضي — المغاسل	2.38 × 1.88	4.47
4	أرضي — المجلس 2	5.00 × 5.00	25.00
5	أرضي — المدخل	4.00 × 7.00	28.00
6	أرضي — الموزع والدرج	4.00 × 5.00	20.00
7	أرضي — الصالة	5.88 × 7.00	41.16
8	أرضي — مستودع	2.88 × 2.88	8.29
9	أرضي — دورة مياه	2.88 × 2.00	5.76
10	أرضي — المطبخ (مفتوح على الصالة)	2.88 × 5.00	14.40
11	أول — غرفة 2	4.00 × 5.00	20.00
12	أول — دورة مياه 1	4.00 × 1.88	7.52
13	أول — الممر	1.76 × 7.00	12.32
14	أول — الصالة العلوية	5.88 × 5.00	29.40
15	أول — غرفة 3	4.00 × 5.00	20.00
16	أول — دورة مياه 2	4.00 × 1.88	7.52
17	أول — غرفة 1	4.00 × 5.00	20.00
	المساحة الصافية الداخلية		293.55
	عتبة مدخل المجلس 1	1.30 × 1.20	1.56
	عتبة مدخل العائلة	1.40 × 1.20	1.68
	عتبة مدخل المجلس 2	1.20 × 1.30	1.56
	السطح العلوي (حوش)	5.12 × 12.36	63.28
	مسطح الدور الأرضي	15.36 × 12.36	189.85
	مسطح الدور الأول	**10.24 × 12.36**	**126.57**
	المساحة الإجمالية المبنية	**مجموع الأدوار**	**316.42**

لقطات المنظور الخارجي

المنظور الأمامي




منظور أمامي من اليسار




منظور أمامي من اليمين




المنظور الخلفي

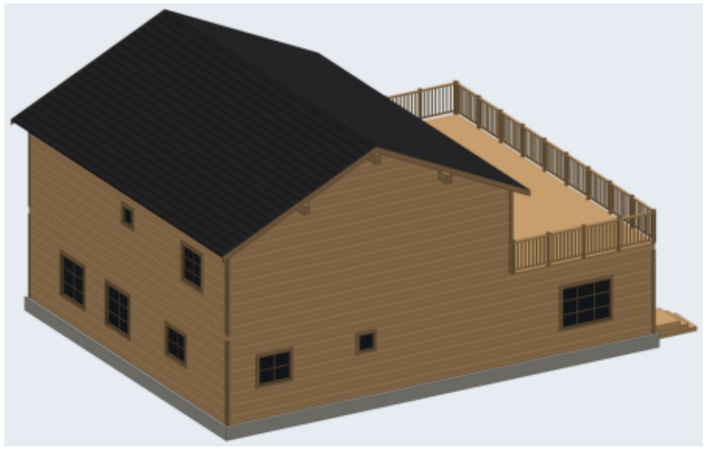

منظور خلفي من اليمين

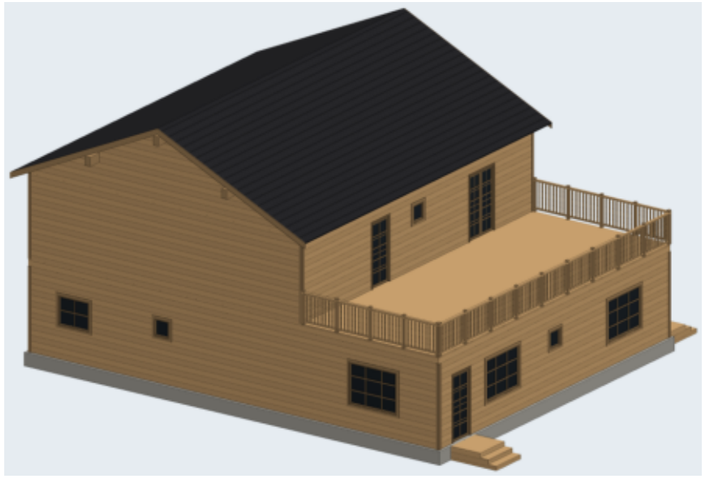

منظور علوي

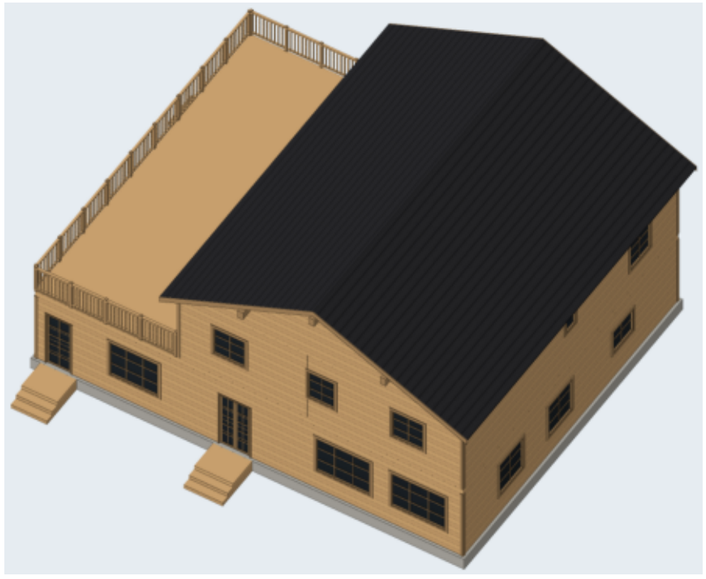


المشروع / العميل	عنوان اللوحة	المقياس	التاريخ	رقم اللوحة
الخيار 2 — مجلسين وصالة + 3 غرف — دورين بسطح علوي **عميل — 3 خيارات**	**لقطات المنظور**	**—**	**2026-10-21**	**A-08 (8/11)**

مصنع وتد الأخشاب
Watad Wood Factory

المقطع العلوي بالفرش — الدور الأرضي

مقطع أفقي على ارتفاع 1.90 م — توزيع الفرش ومسار الحركة

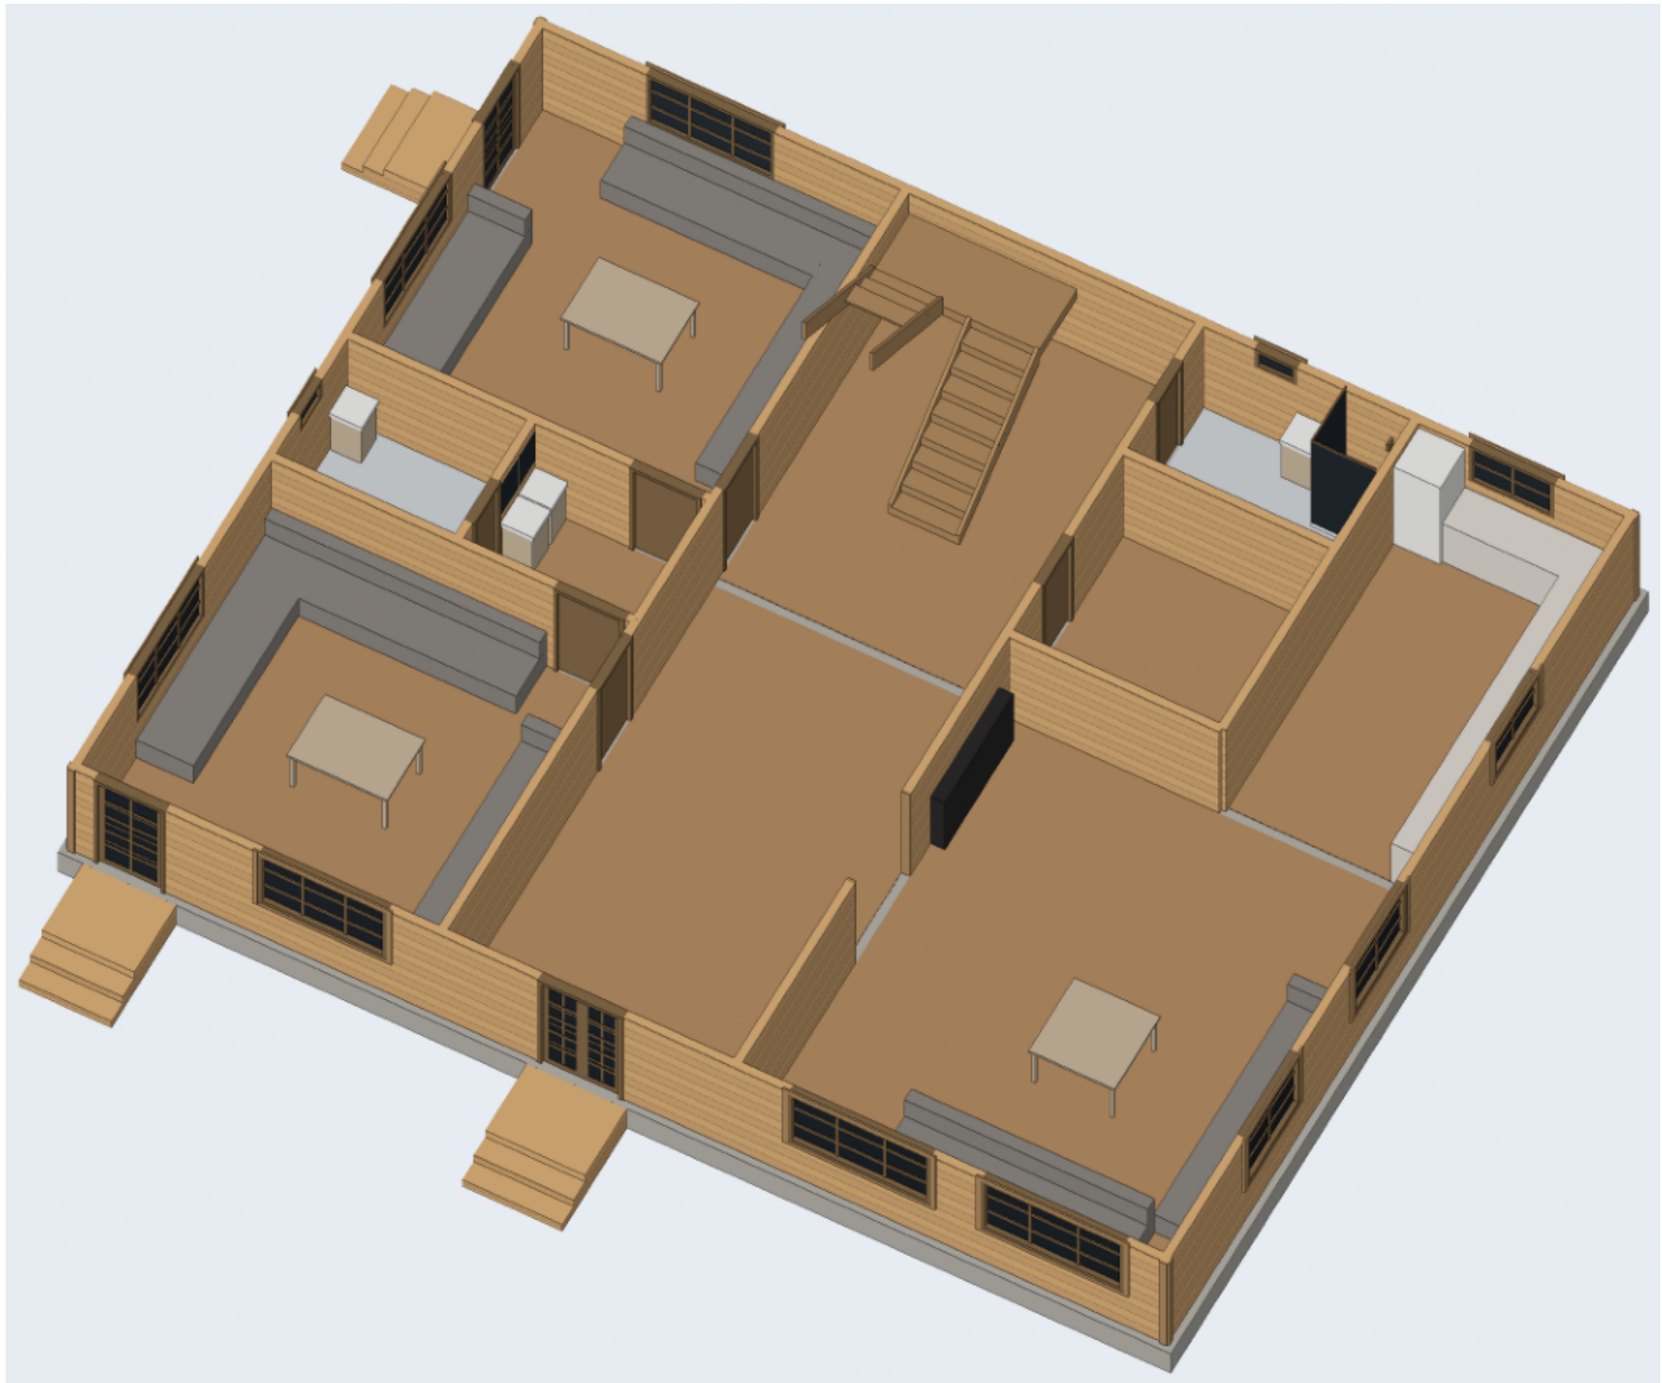


المشروع / العميل	عنوان اللوحة	المقياس	التاريخ	رقم اللوحة
الخيار 2 — مجلسين وصالة + 3 غرف — دورين بسطح علوي **عميل — 3 خيارات**	**المقطع العلوي بالفرش — الدور الأرضي**	**—**	**2026-10-21**	**A-09 (9/11)**

مصنع وتد الأخشاب
Watad Wood Factory

المقطع العلوي بالفرش — الدور الأول

مقطع أفقي على ارتفاع 1.90 م — توزيع الفرش ومسار الحركة

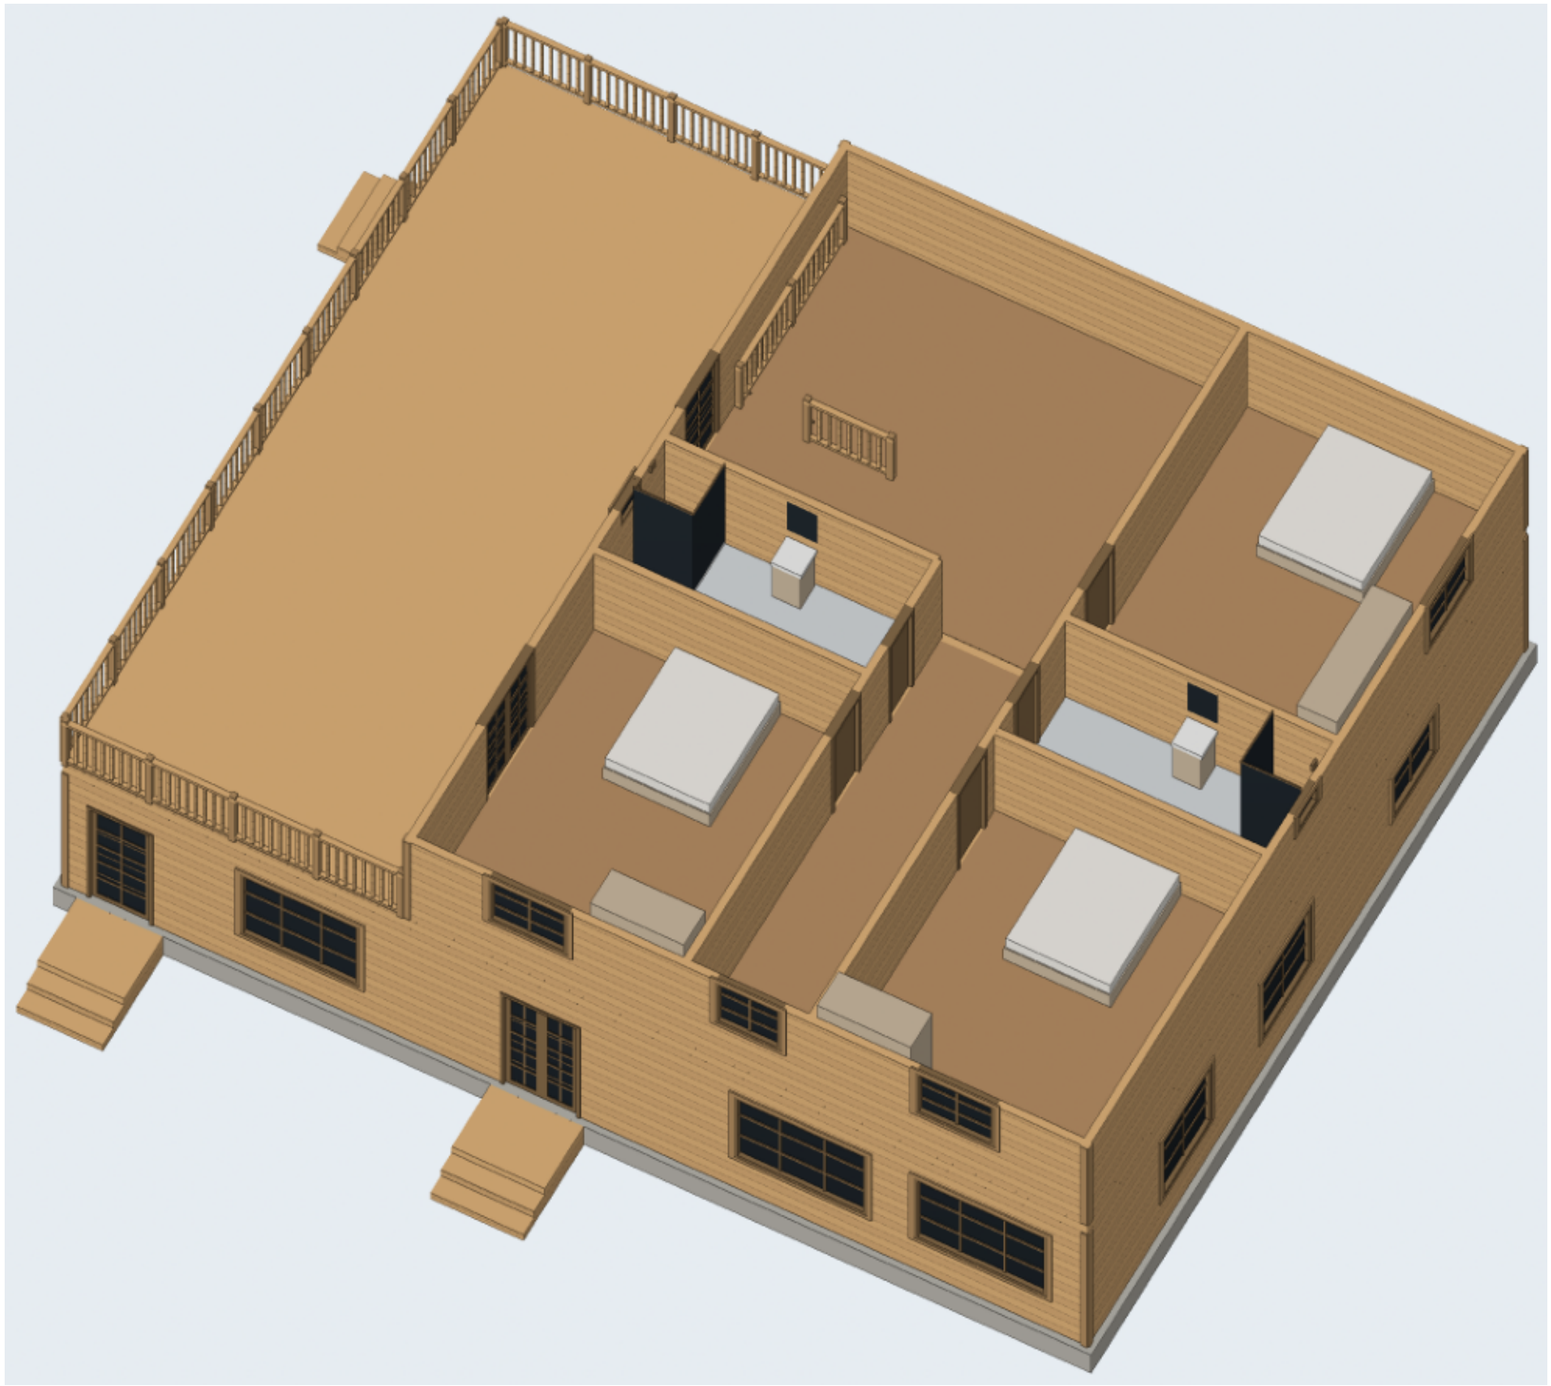


المشروع / العميل	عنوان اللوحة	المقياس	التاريخ	رقم اللوحة
الخيار 2 — مجلسين وصالة + 3 غرف — دورين بسطح علوي **عميل — 3 خيارات**	**المقطع العلوي بالفرش — الدور الأول**	**—**	**2026-10-21**	**A-10 (10/11)**

مصنع وتد الأخشاب
Watad Wood Factory

المنظور ثلاثي الأبعاد والمواد

النمط: جوزي غامق + إطارات سوداء — رندر واقعي بخامات حقيقية

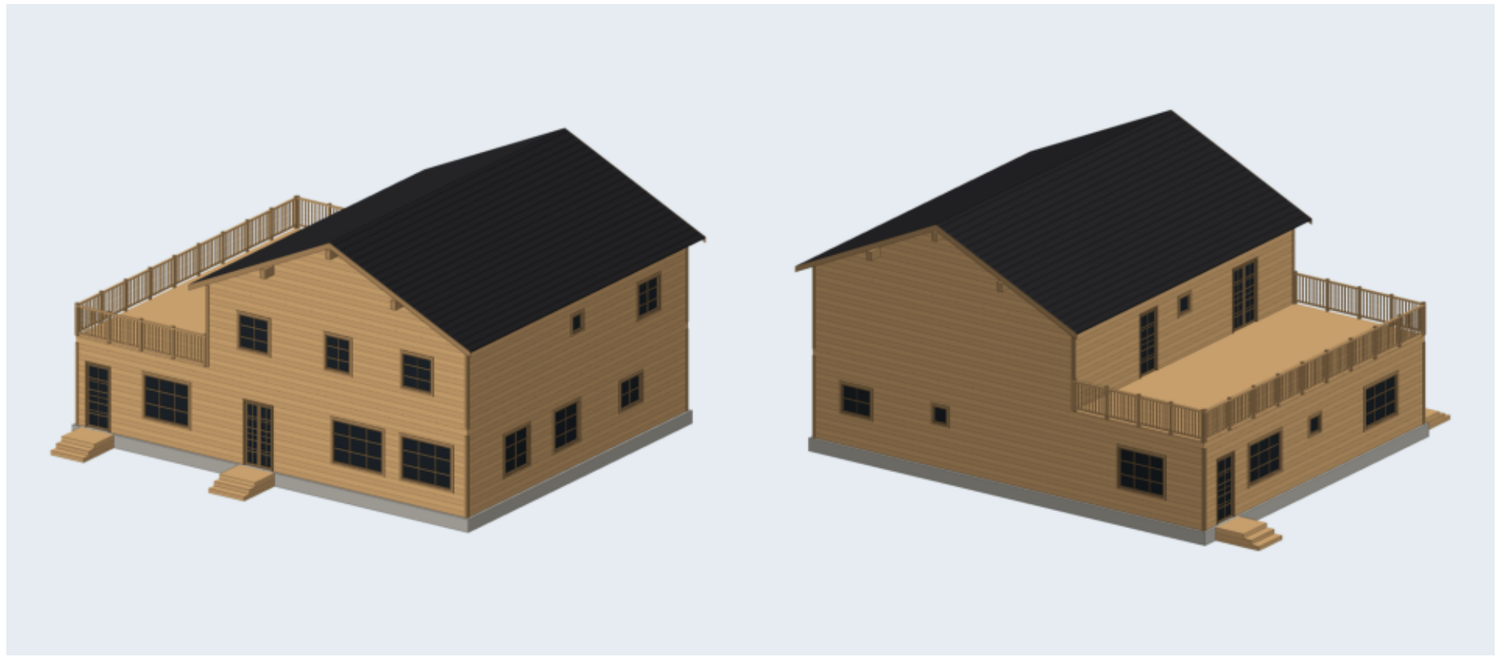

جدول المواد والألوان

الخشب / الصبغة

خشب طبيعي فاتح (بدون صبغة)

القرميد

قرميد رمادي غامق

الزجاج

زجاج عاكس غامق

إطارات الشبابيك والأبواب

إطار خشب بنفس الصبغة أغمق

الكنار والزوايا

نفس الصبغة أغمق درجة


الصبة

خرسانة 45 سم


الدربزين: ألواح أفقية متقاربة (عصري)

تقسيم الشبابيك: بدون | الباب الرئيسي: زجاج بتقسيمات (فرنسي)

أنواع الدربزين المعتمدة (من مشاريع المصنع)

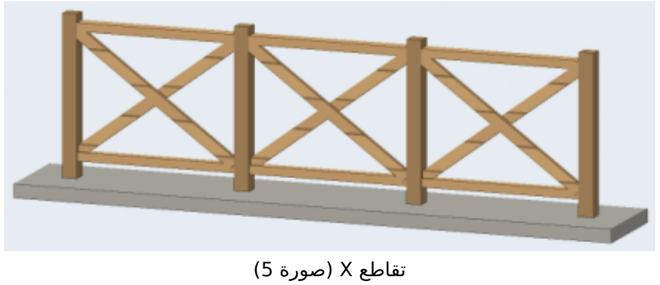

تقاطع X (صورة 5)

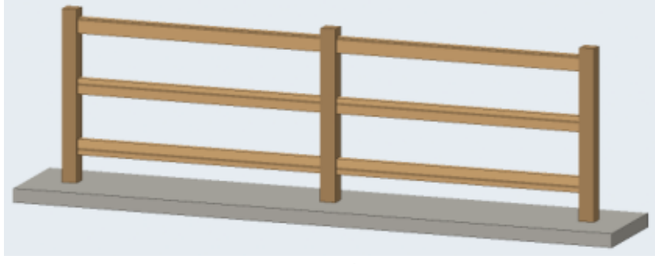

3 مرابيع أفقية (صورة 2)



قوائم رأسية متقاربة (صورة 1)

المشروع / العميل	عنوان اللوحة	المقياس	التاريخ	رقم اللوحة
مصنع وتد الأخشاب Watad Wood Factory **الخيار 2 — مجلسين وصالة + 3 غرف — دورين بسطح علوي عميل — 3 خيارات**	**المنظور والمواد**	—	**2026-10-21**	**A-11 (11/11)**