
المسقط الأفقي مع الفرش — الدور الأرضي


الأبعاد بالسنتيمتر - الجدران: قوائم 7×5 + تلبيس 2.5 من الجهتين (12 سم) | منسوب الأرضية +0.00

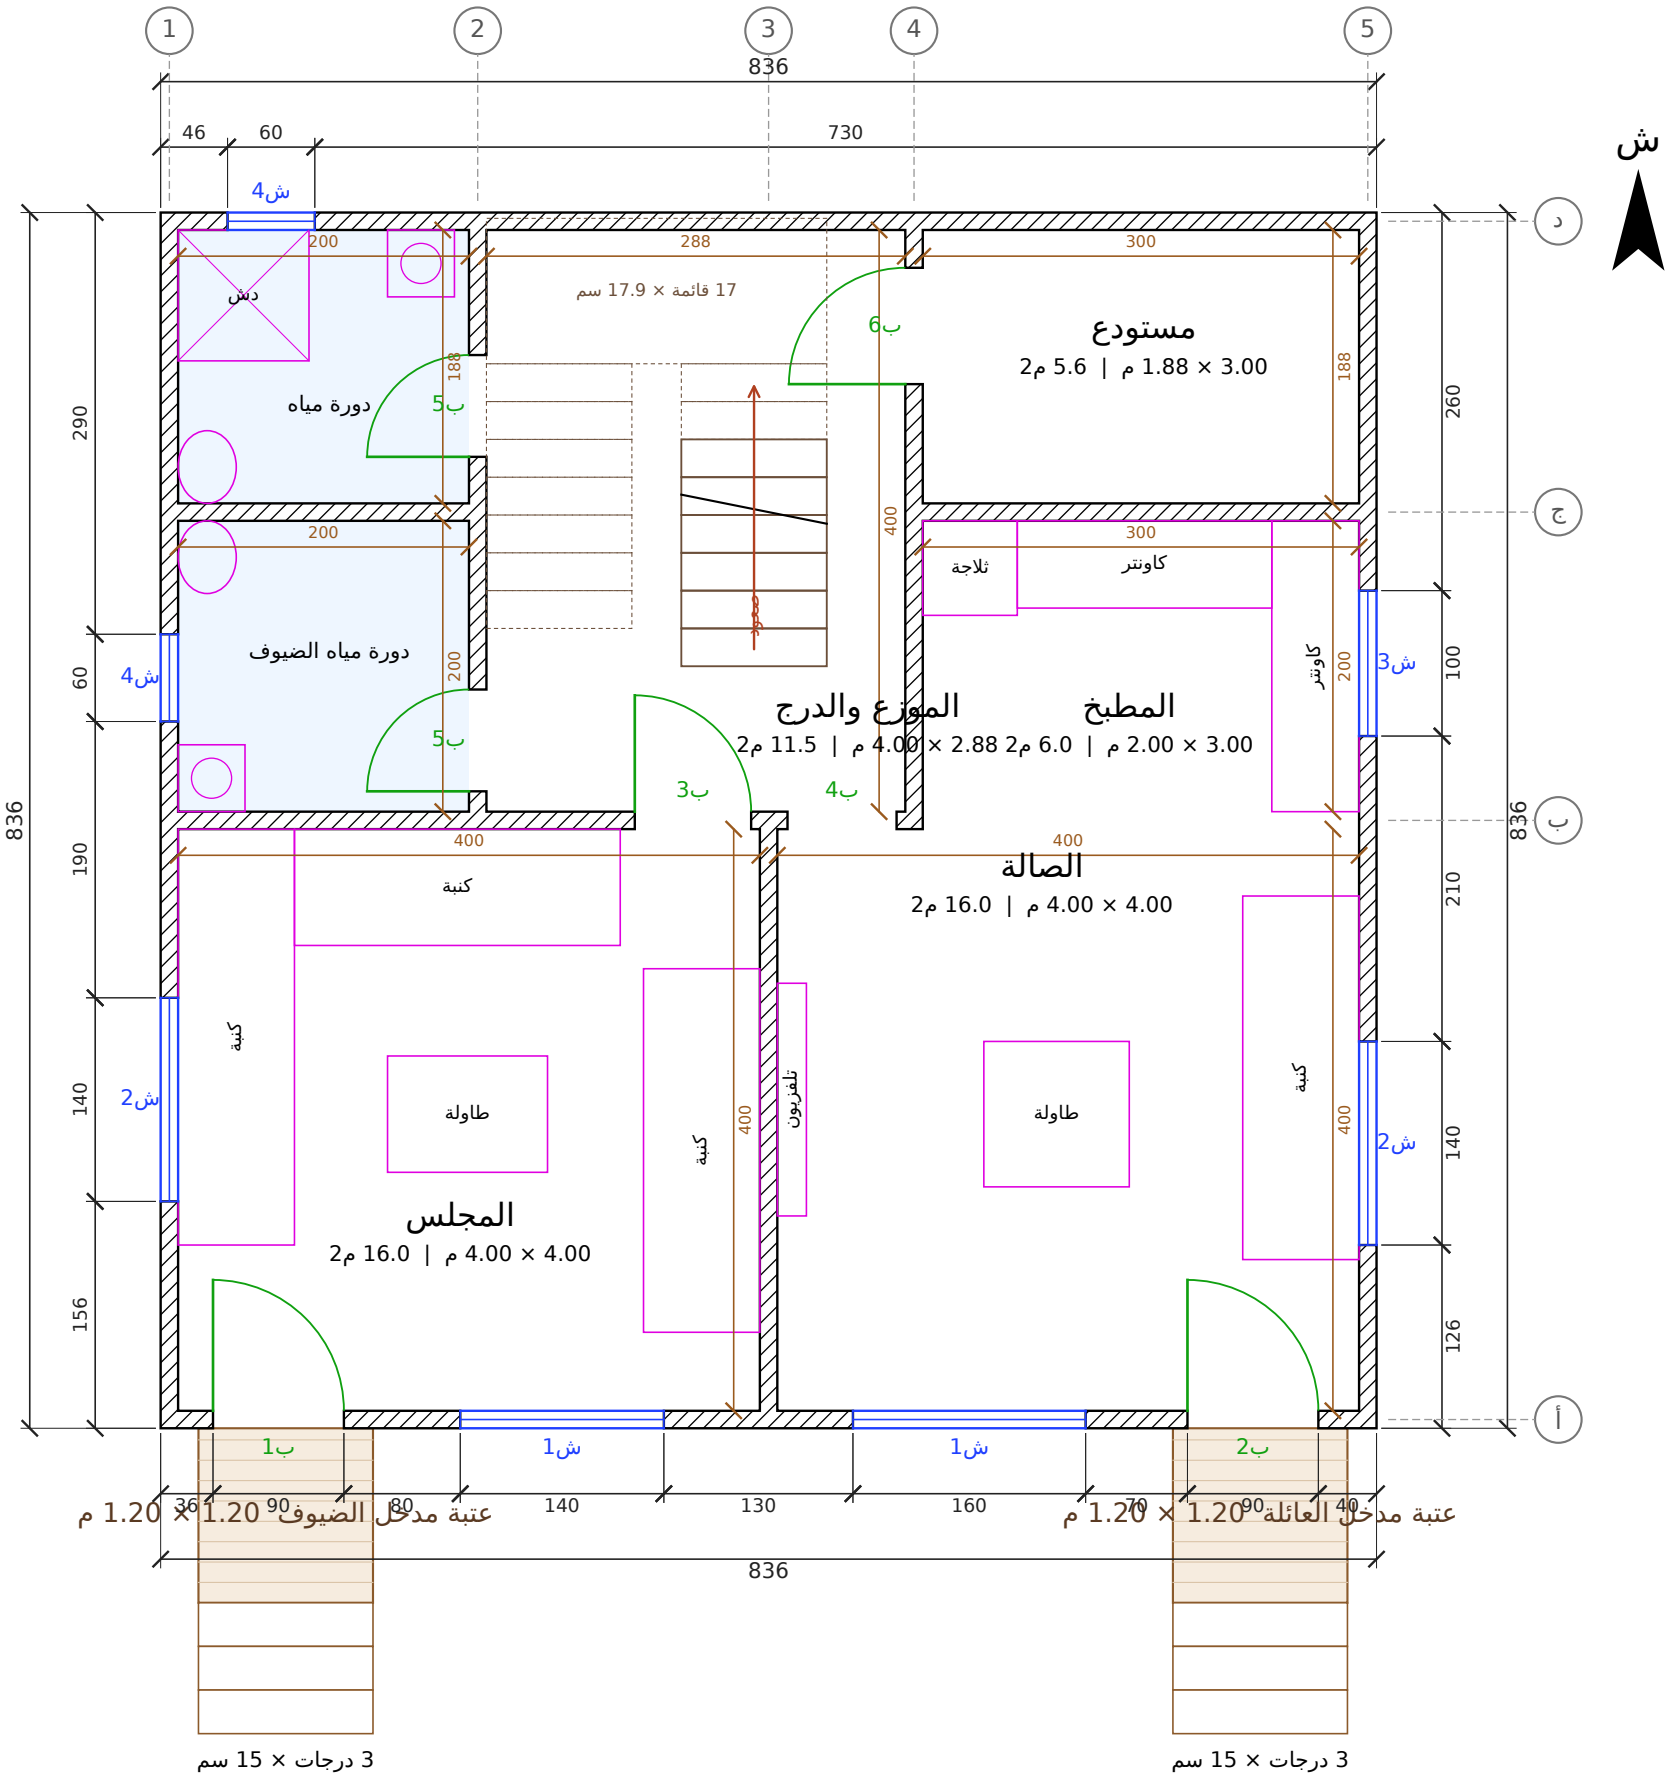


مصنع وتد الأخشاب Watad Wood Factory	المشروع / العميل الخيار 3 — مجلس وصالة + غرفة — دورين بسطح علوي عميل — 3 خيارات	عنوان اللوحة المسقط الأفقي — الدور الأرضي	المقياس 1:50	التاريخ 2026-10-21	رقم اللوحة A-01 (1/11)

المسقط الأفقي مع الفرش — الدور الأول

الأبعاد بالسنتيمتر - الجدران: قوائم 7×5 + تلبيس 2.5 من الجهتين (12 سم) | منسوب الأرضية +3.05

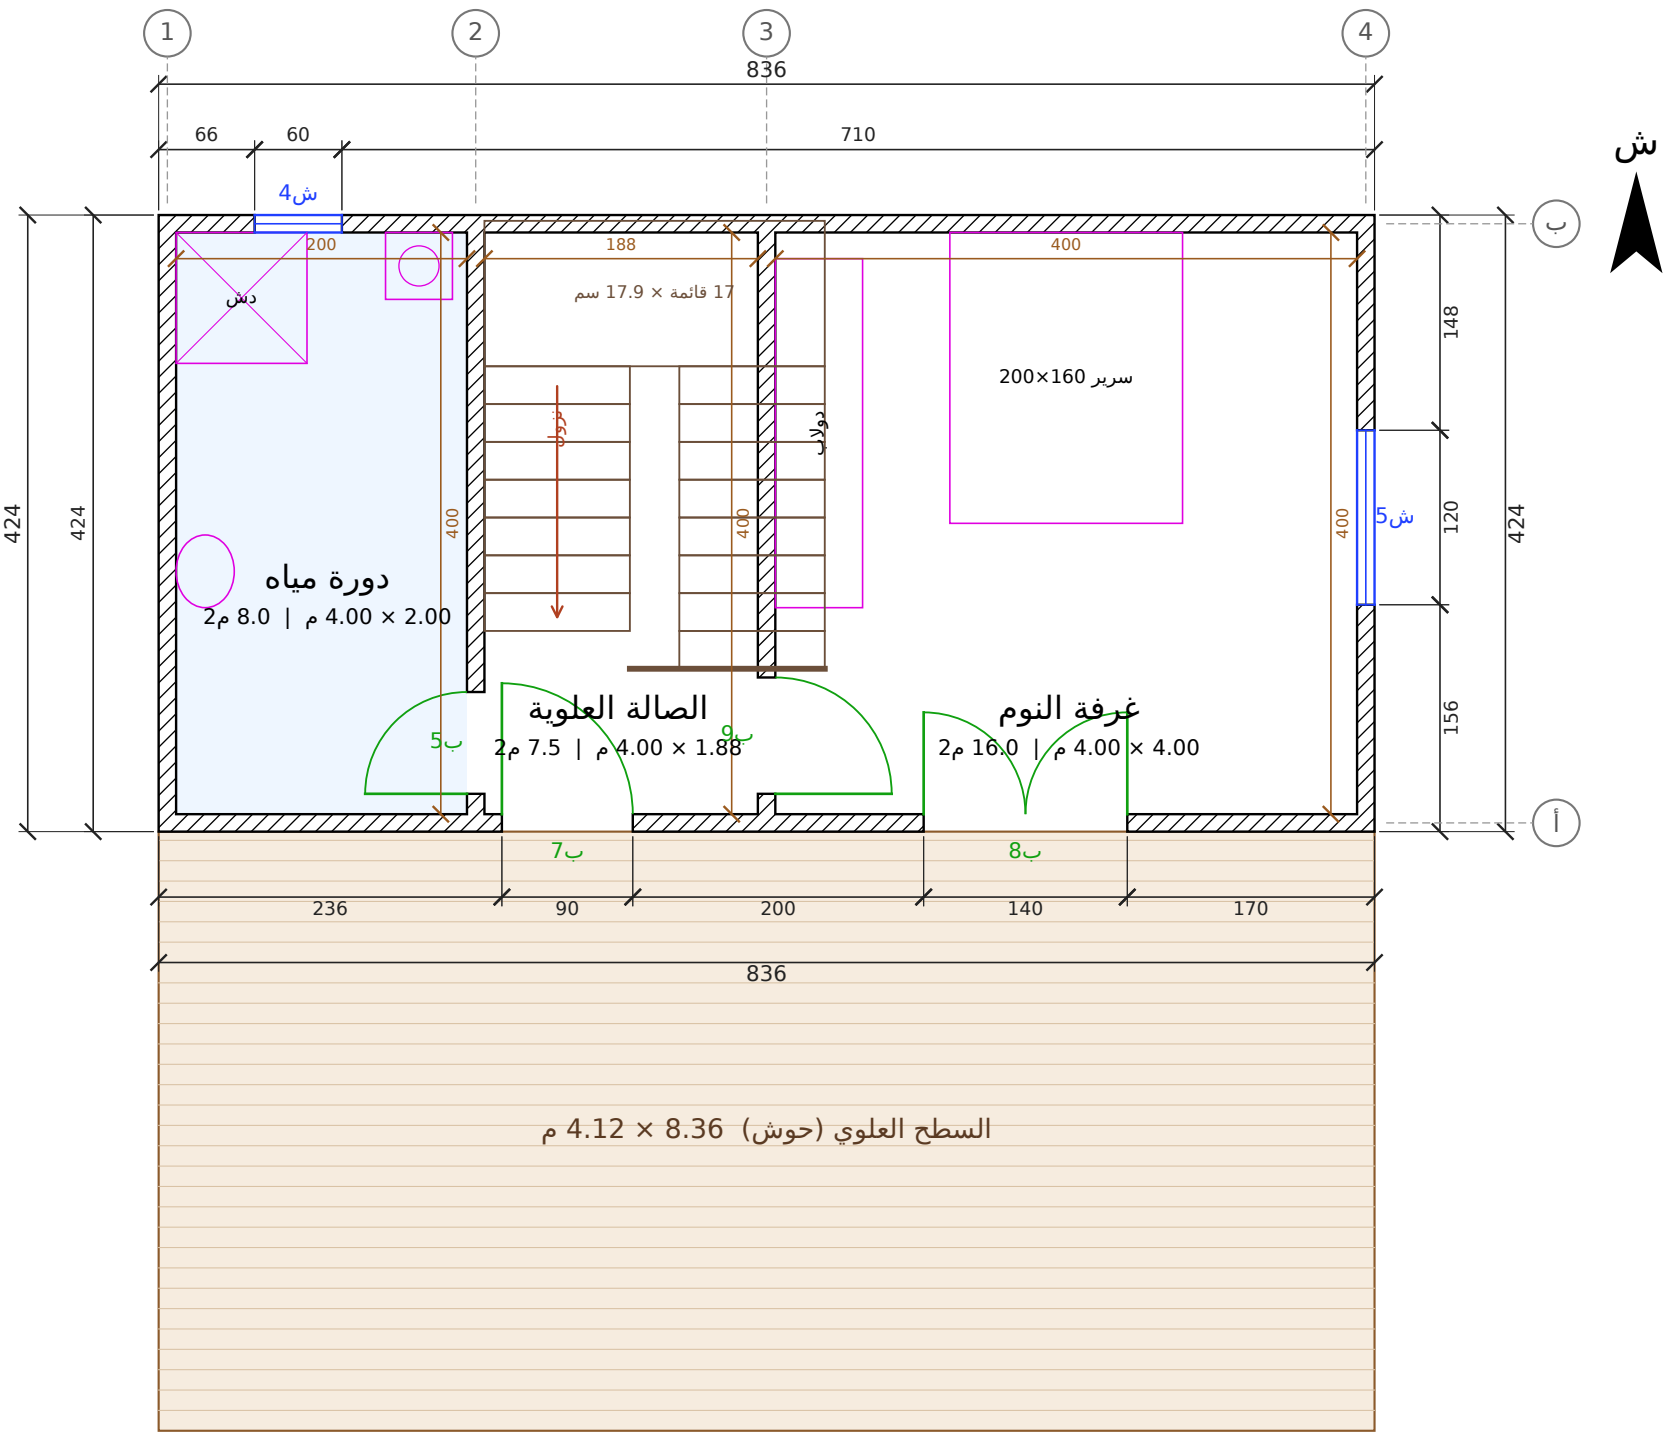


المشروع / العميل	عنوان اللوحة	المقياس	التاريخ	رقم اللوحة
مصنع وتد الأخشاب Watad Wood Factory **الخيار 3 — مجلس وصالة + غرفة — دورين بسطح علوي** **عميل — 3 خيارات**	**المسقط الأفقي — الدور الأول**	**1:50**	**2026-10-21**	**A-02 (2/11)**

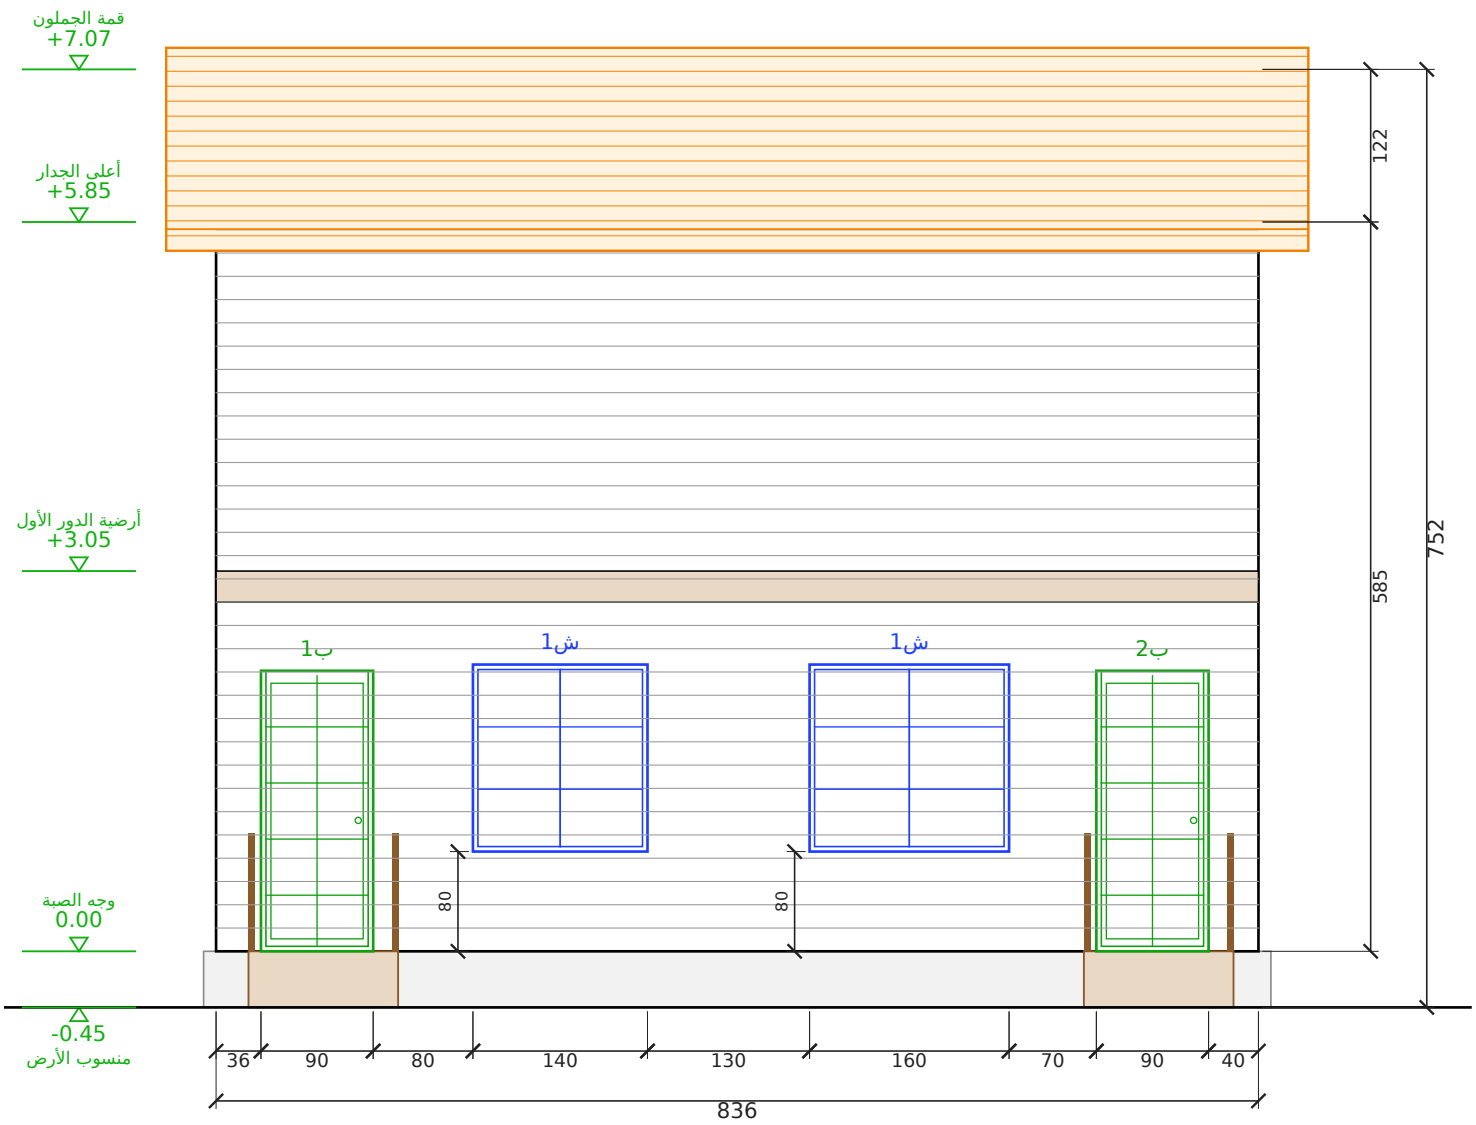

الواجهة الأمامية


مقياس 1:50 | الوحدة: سم

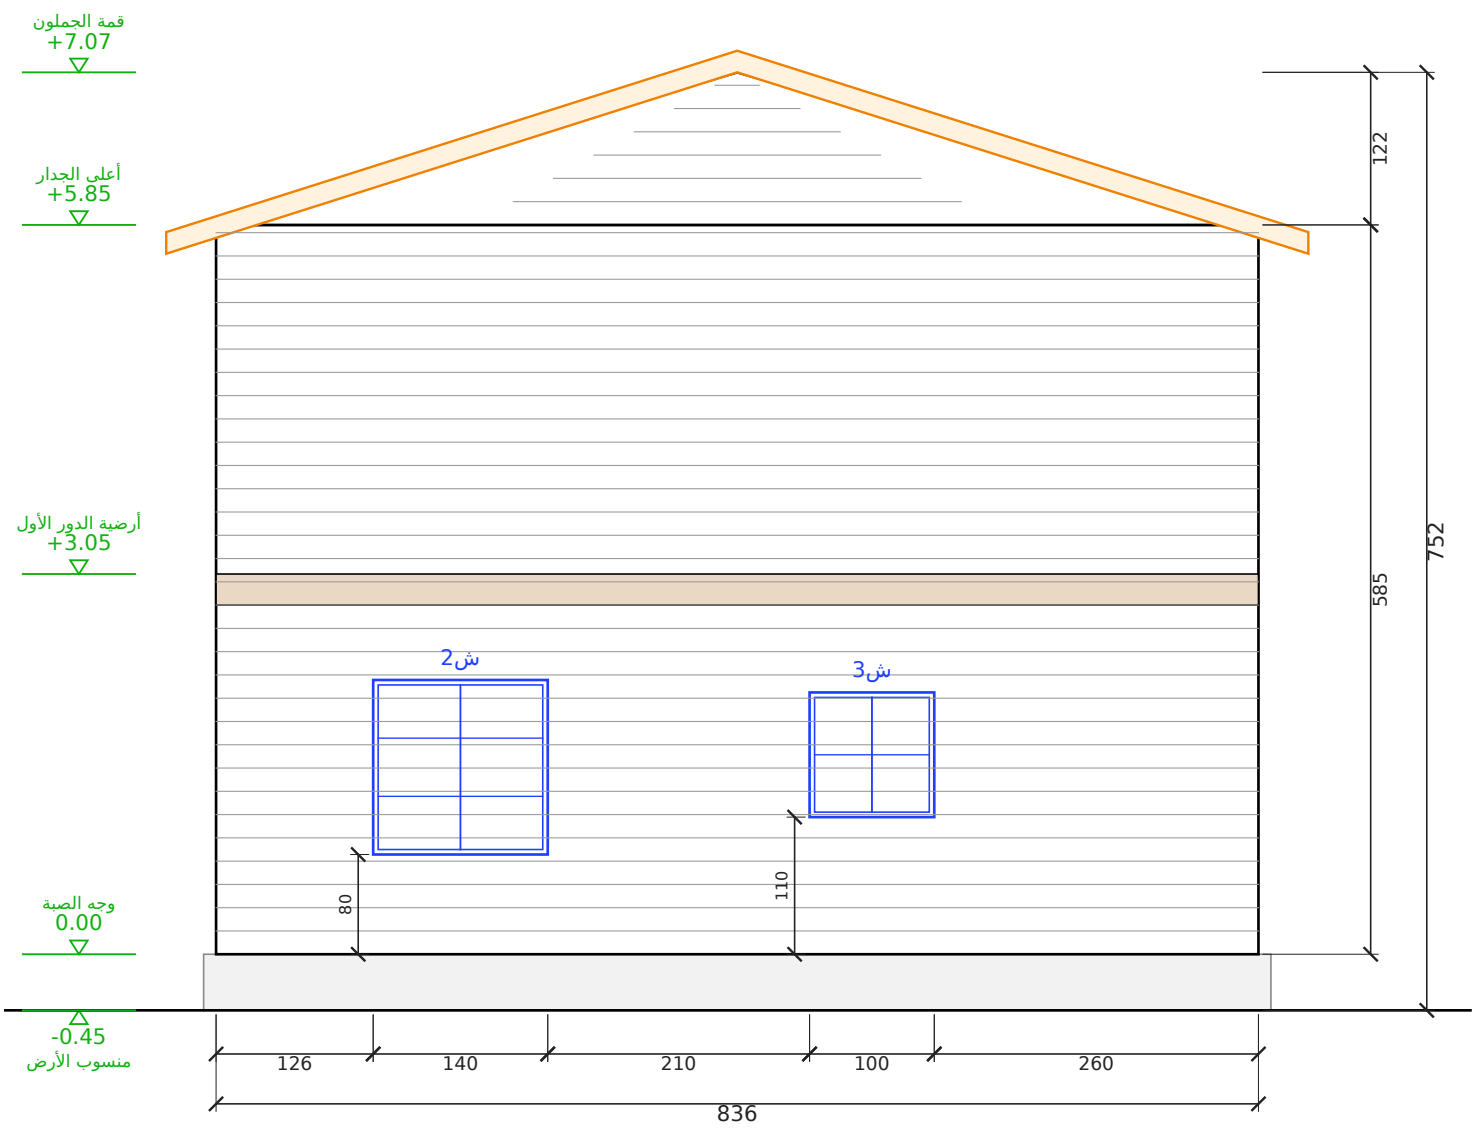

الواجهة الشرقية


مقياس 1:50 | الوحدة: سم

المشروع / العميل	عنوان اللوحة	المقياس	التاريخ	رقم اللوحة
مصنع وتد الأخشاب Watad Wood Factory **الخيار 3 — مجلس وصالة + غرفة — دورين بسطح علوي** **عميل — 3 خيارات**	**الواجهة الأمامية والواجهة الشرقية**	**1:50**	**2026-10-21**	**A-03 (3/11)**

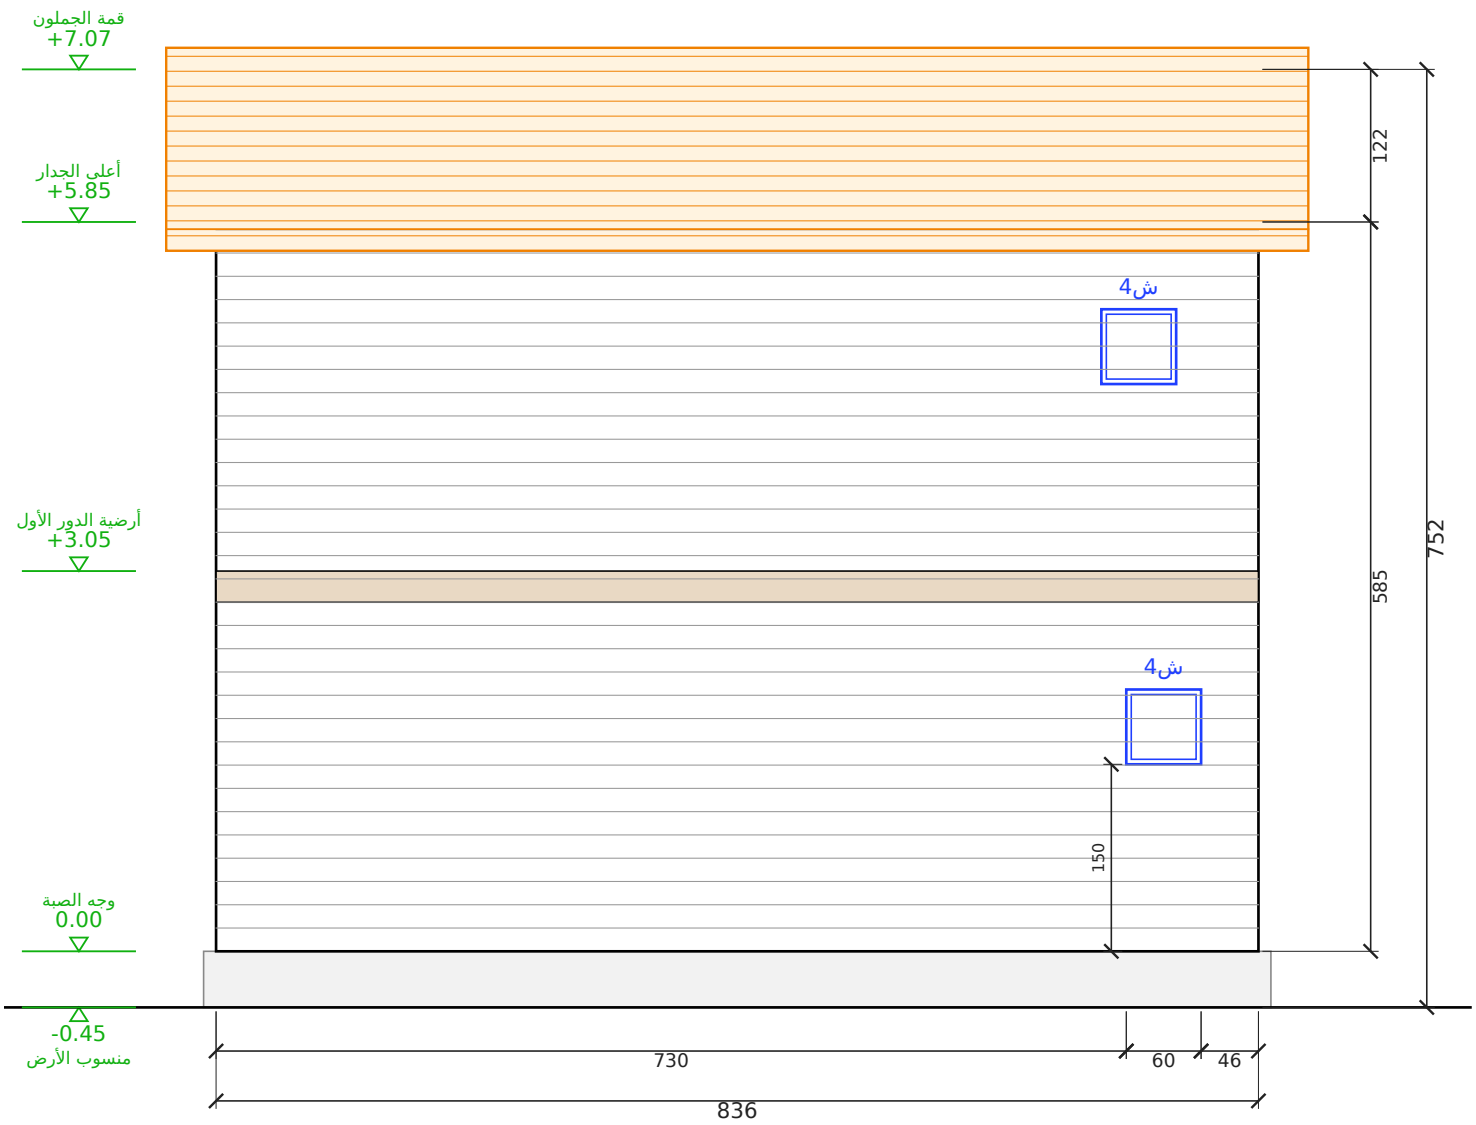

الواجهة الخلفية

مقياس 1:50 | الوحدة: سم

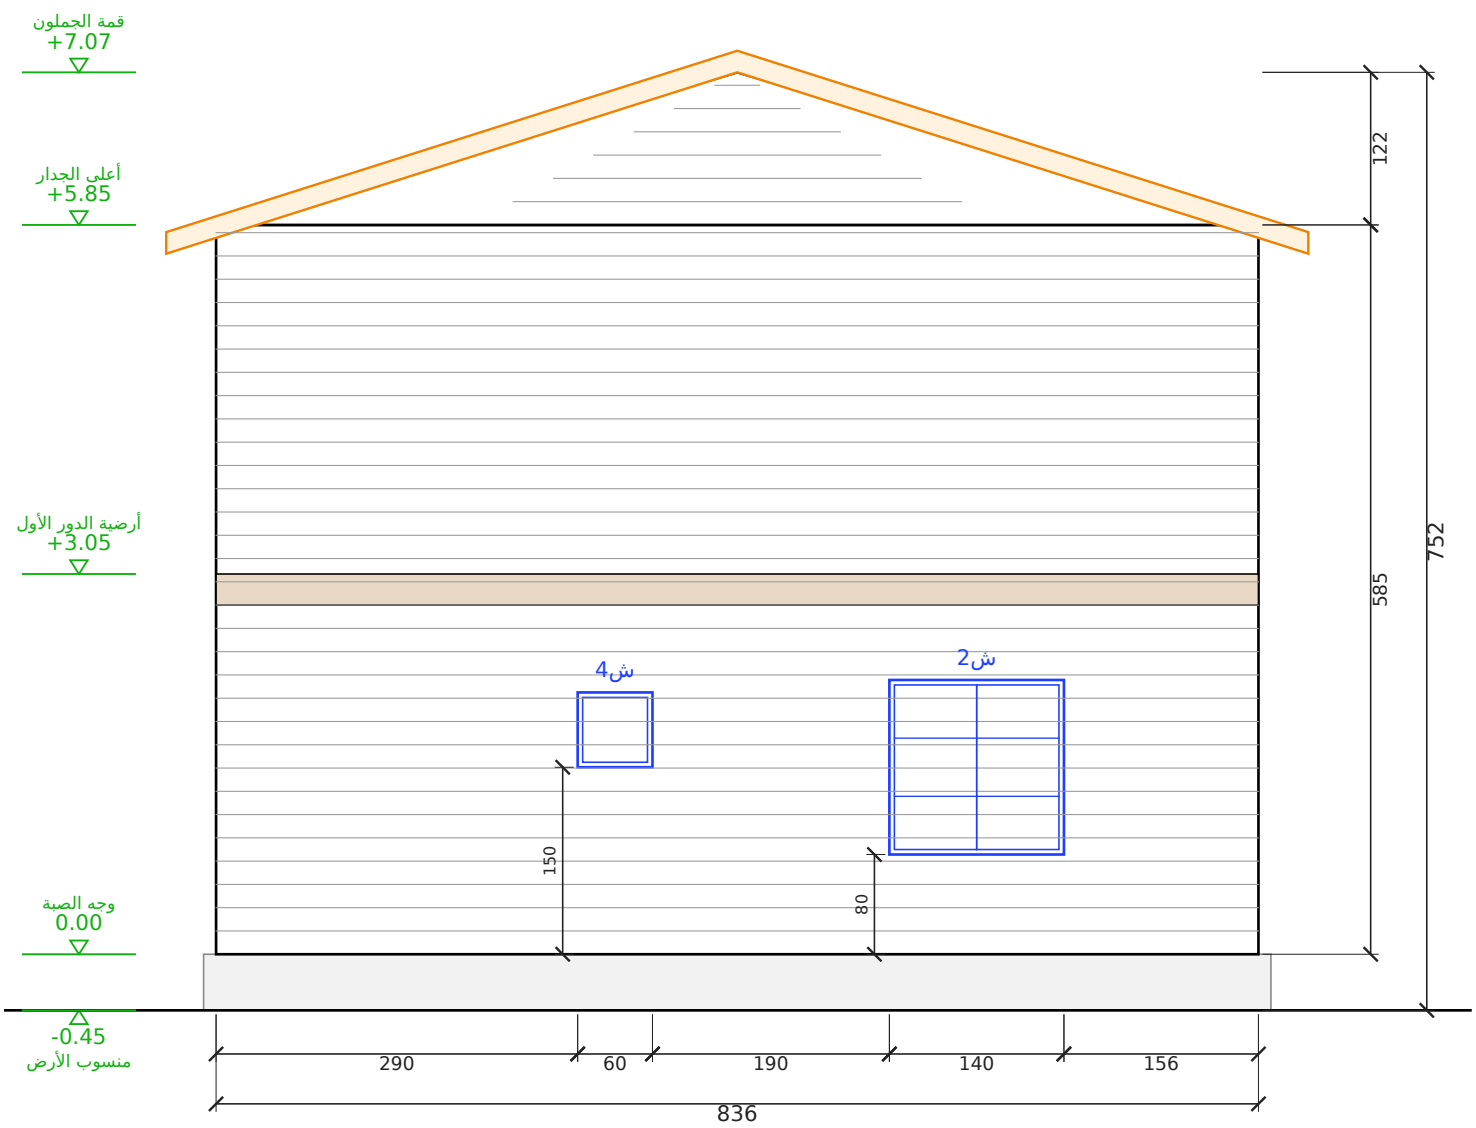


الواجهة الغربية


مقياس 1:50 | الوحدة: سم

المشروع / العميل	عنوان اللوحة	المقياس	التاريخ	رقم اللوحة
مصنع وتد الأخشاب Watad Wood Factory **الخيار 3 — مجلس وصالة + غرفة — دورين بسطح علوي** **عميل — 3 خيارات**	**الواجهة الخلفية والواجهة الغربية**	**1:50**	**2026-10-21**	**A-04 (4/11)**


مسقط السقف (جملون)
رفرف 40 سم من كل جهة | مقياس 1:50

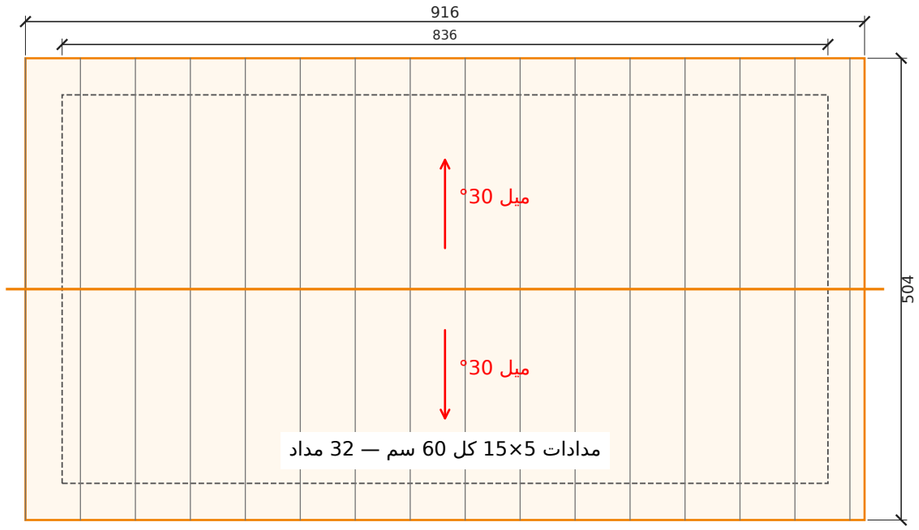

قطاع عرضي أ-أ
مقياس 1:50 | الوحدة: سم

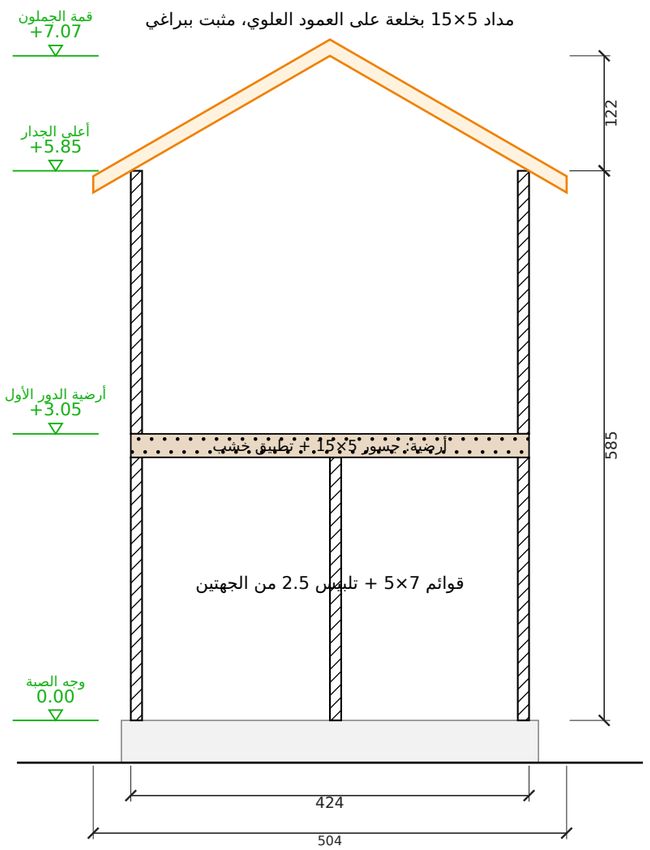

تفصيلة جلوس المداد على العلوي (1:5)

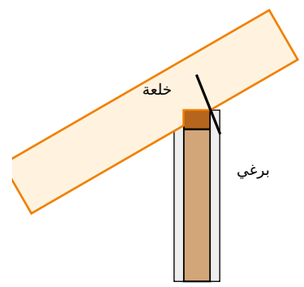

علوي 7×5 على قائم 7×5

المشروع / العميل	عنوان اللوحة	المقياس	التاريخ	رقم اللوحة
الخيار 3 — مجلس وصالة + غرفة — دورين بسطح علوي **عميل — 3 خيارات**	**مسقط السقف والقطاع**	**1:50**	**2026-10-21**	**A-05 (5/11)**

مصنع وتد الأخشاب
Watad Wood Factory

جدول مقاسات الأبواب والشبابيك
مقاس الفتحة الصافي في الجدار - الوحدة: سم

الرمز	النوع	العرض (سم)	الارتفاع (سم)	ارتفاع الجلسة (سم)	العدد	الموقع
ب1	باب	90	225	-	1	الأمامية
ب2	باب	90	225	-	1	الأمامية
ب3	باب	80	210	-	1	المجلس — الموزع
ب4	باب	75	210	-	1	فتحة الصالة — الموزع
ب5	باب	70	210	-	3	دورة مياه الضيوف - دورة مياه 2
ب6	باب	80	210	-	1	المستودع
ب7	باب	90	220	-	1	الأمامية (على السطح)
ب8	باب مزدوج	140	220	-	1	الأمامية (على السطح)
ب9	باب	80	210	-	1	غرفة النوم
ش1	شباك	140	150	80	1	الأمامية
ش1	شباك	160	150	80	1	الأمامية
ش2	شباك	140	140	80	2	الشرقية - الغربية
ش3	شباك	100	100	110	1	الشرقية
ش4	شباك	60	60	150	3	الخلفية 2 - الغربية
ش5	شباك	120	120	90	1	الشرقية

الإجمالي: أبواب 11 - شبابيك 9

جدول المساحات وبيانات المشروع والتسعير

بيانات المشروع

البند	البيان
المشروع	الخيار 3 — مجلس وصالة + غرفة — دورين بسطح علوي
العميل	عميل — 3 خيارات
الموقع	—
الاستخدام	سكن / استراحة
التاريخ	2026-10-21
نظام البناء	هيكل خشب 5×7 + تلبيس 2.5 سم من الجهتين
السقف	جملون 30° — قرميد معدني

التسعير

البند	القيمة
المساحة المبنية (م2)	105.34
سعر المتر المربع	1,096 ريال
الإجمالي	**115,453 ريال**

ملاحظات:

- السعر على المساحة المبنية للدورين بسعر المصنع 1,096 ريال/م².
- السطح العلوي (حوش) 34 م² يُسعّر منفصل (أرضية + عزل مائي + دربزين).

جدول المساحات


م	الفراغ	الأبعاد (م)	المساحة (م2)
1	أرضي — المجلس	4.00 × 4.00	16.00
2	أرضي — الصالة	4.00 × 4.00	16.00
3	أرضي — دورة مياه الضيوف	2.00 × 2.00	4.00
4	أرضي — دورة مياه	2.00 × 1.88	3.76
5	أرضي — الموزع والدرج	2.88 × 4.00	11.52
6	أرضي — المطبخ	3.00 × 2.00	6.00
7	أرضي — مستودع	3.00 × 1.88	5.64
8	أول — دورة مياه	2.00 × 4.00	8.00
9	أول — الصالة العلوية	1.88 × 4.00	7.52
10	أول — غرفة النوم	4.00 × 4.00	16.00
	المساحة الصافية الداخلية		94.44
	عتبة مدخل الضيوف	1.20 × 1.20	1.44
	عتبة مدخل العائلة	1.20 × 1.20	1.44
	السطح العلوي (حوش)	8.36 × 4.12	34.44
	مسطح الدور الأرضي	8.36 × 8.36	69.89
	مسطح الدور الأول	**8.36 × 4.24**	**35.45**
	المساحة الإجمالية المبنية	**مجموع الأدوار**	**105.34**

لقطات المنظور الخارجي

المنظور الأمامي




منظور أمامي من اليسار

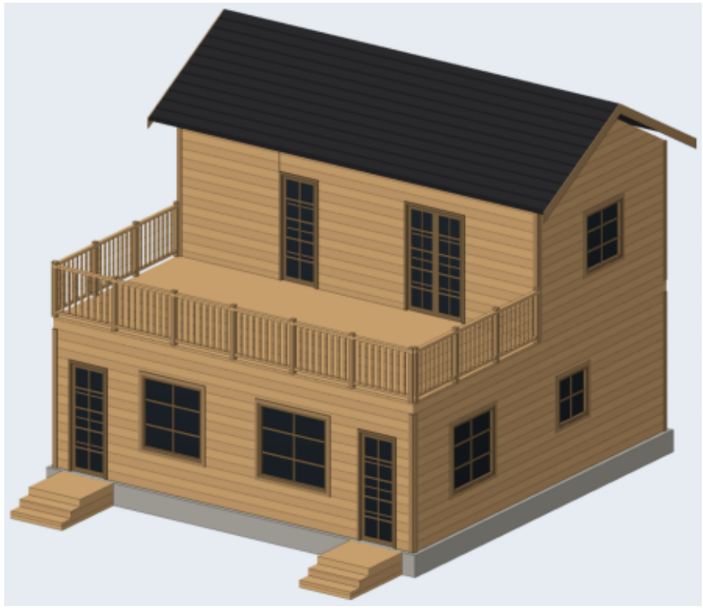


منظور أمامي من اليمين




المنظور الخلفي

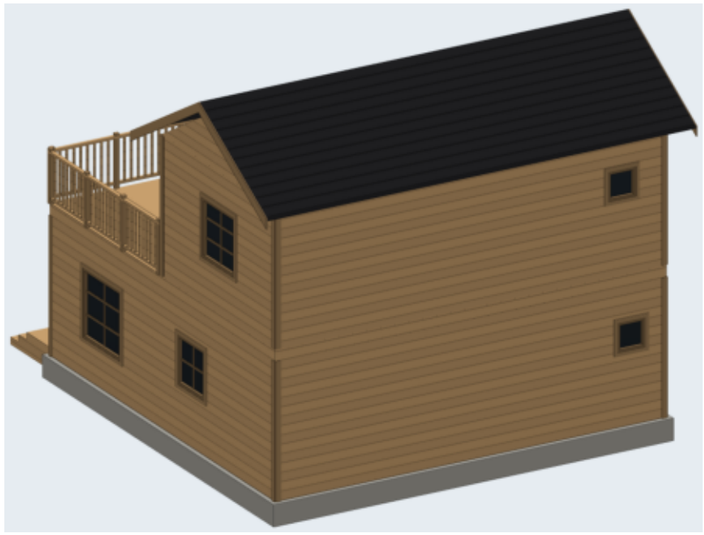

منظور خلفي من اليمين

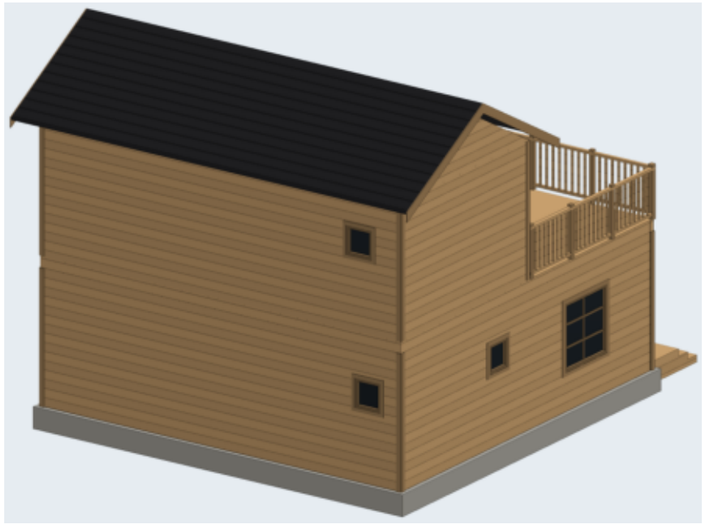

منظر علوي

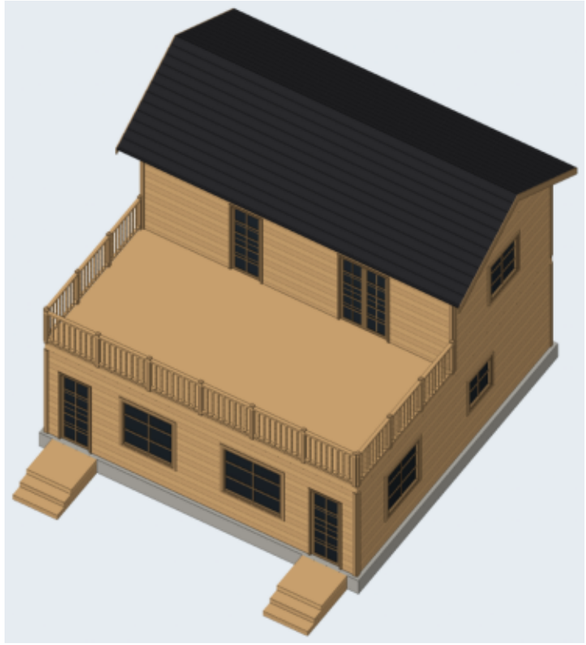


المشروع / العميل	عنوان اللوحة	المقياس	التاريخ	رقم اللوحة
الخيار 3 — مجلس وصالة + غرفة — دورين بسطح علوي **عميل — 3 خيارات**	**لقطات المنظور**	**—**	**2026-10-21**	**A-08 (8/11)**

مصنع وتد الأخشاب
Watad Wood Factory

المقطع العلوي بالفرش — الدور الأرضي

مقطع أفقي على ارتفاع 1.90 م — توزيع الفرش ومسار الحركة

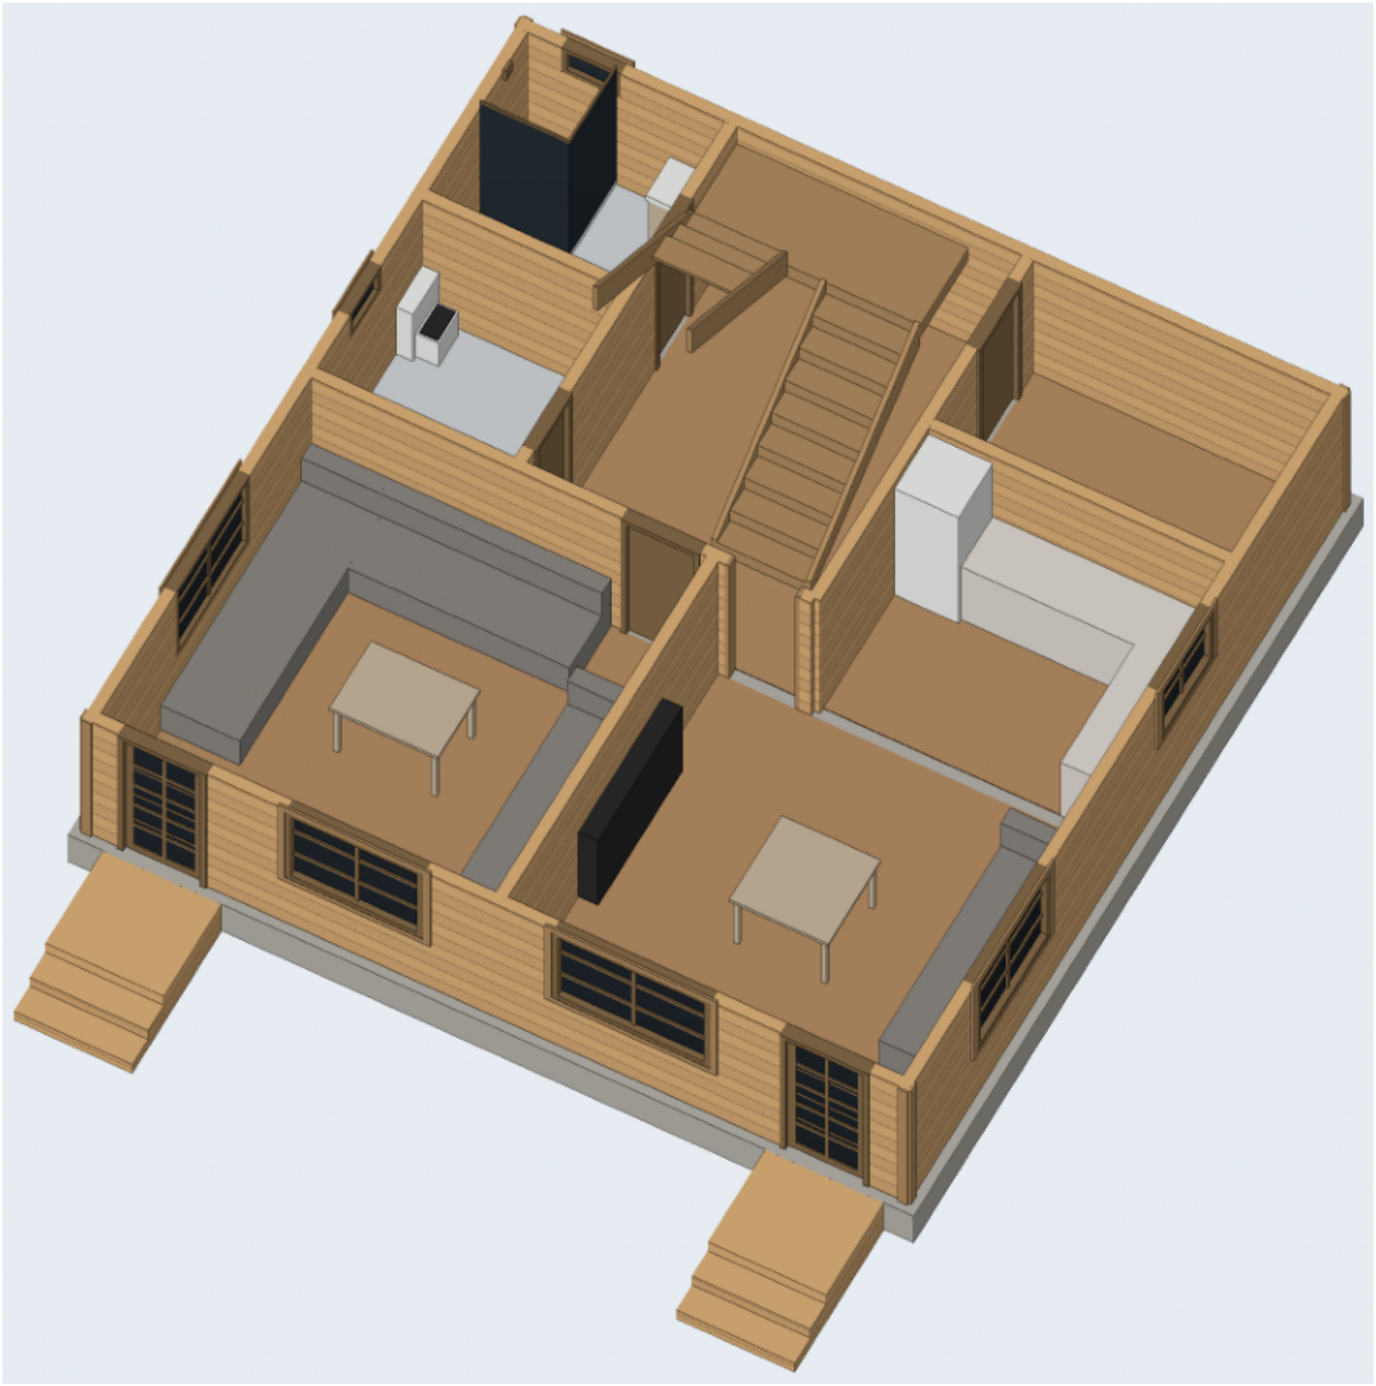


المشروع / العميل	عنوان اللوحة	المقياس	التاريخ	رقم اللوحة
الخيار 3 — مجلس وصالة + غرفة — دورين بسطح علوي **عميل — 3 خيارات**	**المقطع العلوي بالفرش — الدور الأرضي**	**—**	**2026-10-21**	**A-09 (9/11)**

مصنع وتد الأخشاب
Watad Wood Factory

المقطع العلوي بالفرش — الدور الأول

مقطع أفقي على ارتفاع 1.90 م — توزيع الفرش ومسار الحركة

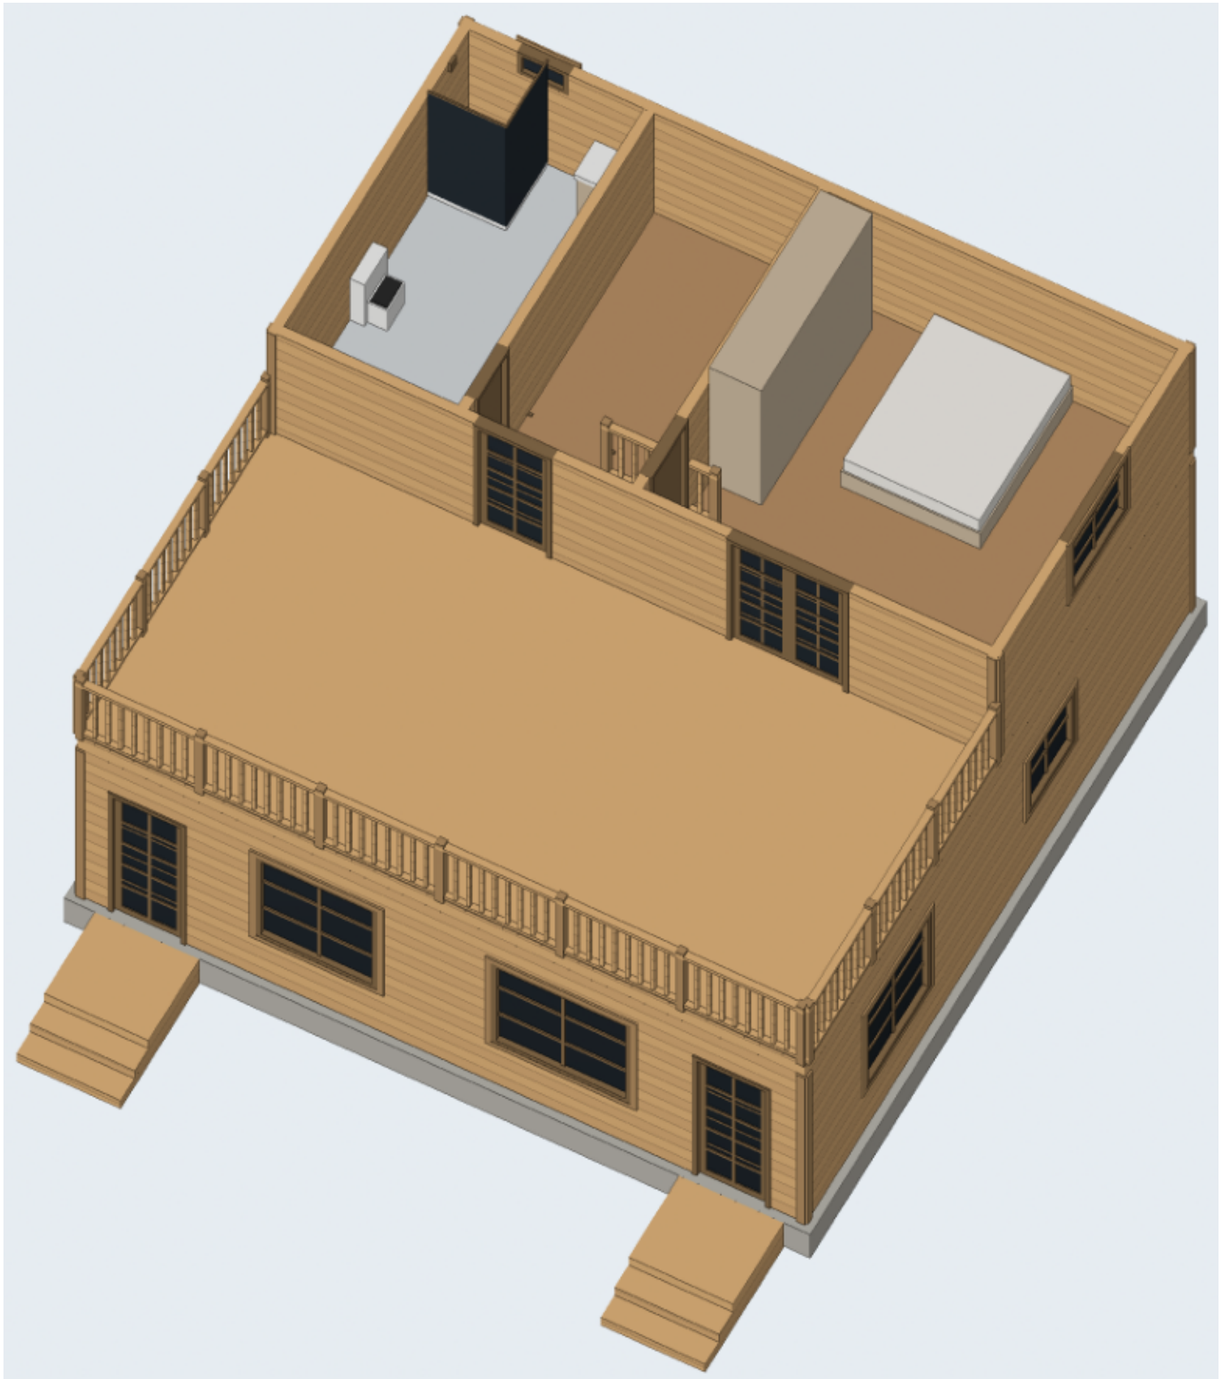


المشروع / العميل	عنوان اللوحة	المقياس	التاريخ	رقم اللوحة
الخيار 3 — مجلس وصالة + غرفة — دورين بسطح علوي **عميل — 3 خيارات**	**المقطع العلوي بالفرش — الدور الأول**	**—**	**2026-10-21**	**A-10 (10/11)**

مصنع وتد الأخشاب
Watad Wood Factory

المنظور ثلاثي الأبعاد والمواد

النمط: جوزي غامق + إطارات سوداء — رندر واقعي بخامات حقيقية

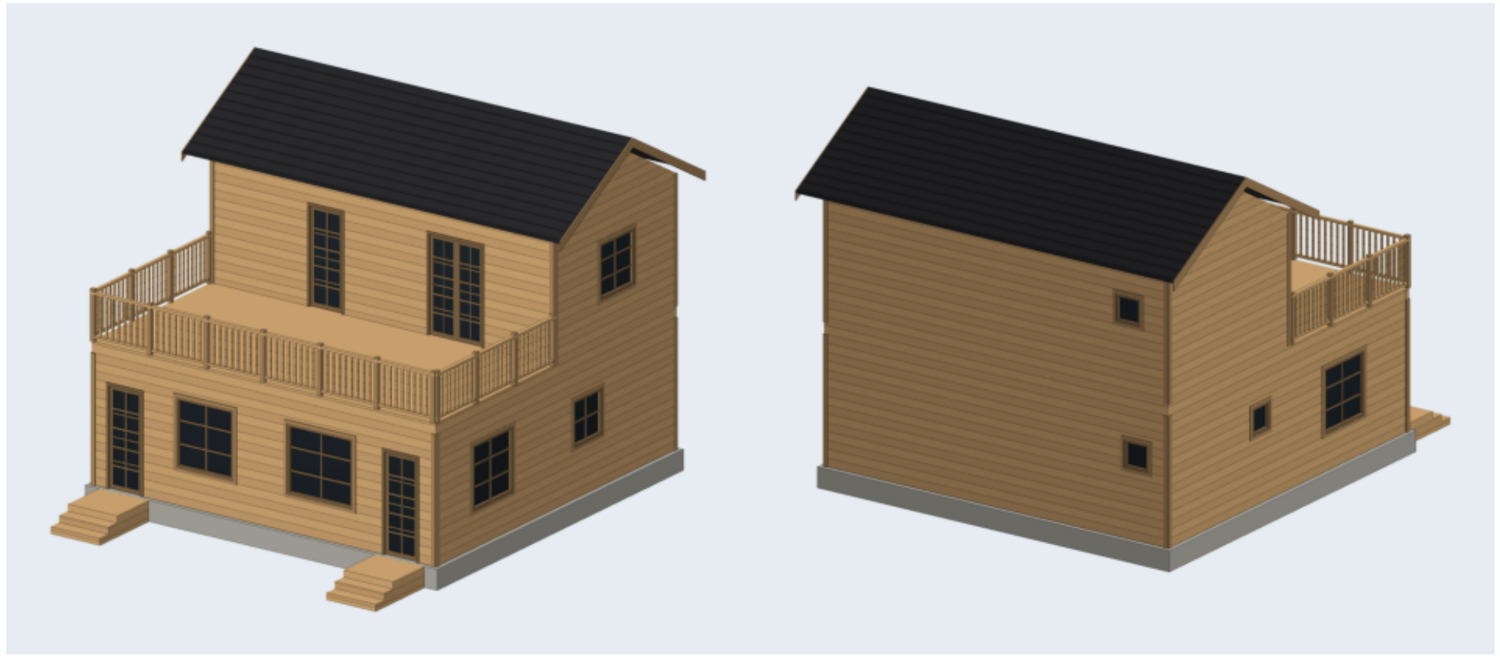

جدول المواد والألوان

الخشب / الصبغة

خشب طبيعي فاتح (بدون صبغة)

القرميد

قرميد رمادي غامق

الزجاج

زجاج عاكس غامق

إطارات الشبابيك والأبواب

إطار خشب بنفس الصبغة أغمق

الكنار والزوايا

نفس الصبغة أغمق درجة


الصبة

خرسانة 45 سم


الدربزين: ألواح أفقية متقاربة (عصري)

تقسيم الشبابيك: بدون | الباب الرئيسي: زجاج بتقسيمات (فرنسي)

أنواع الدربزين المعتمدة (من مشاريع المصنع)

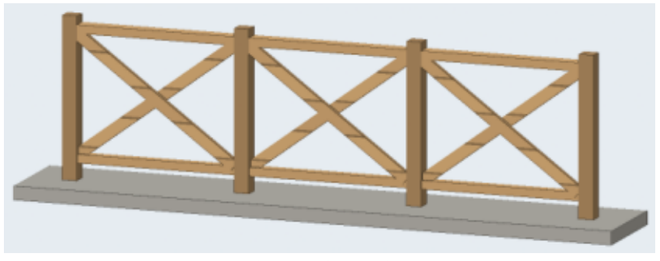

تقاطع X (صورة 5)

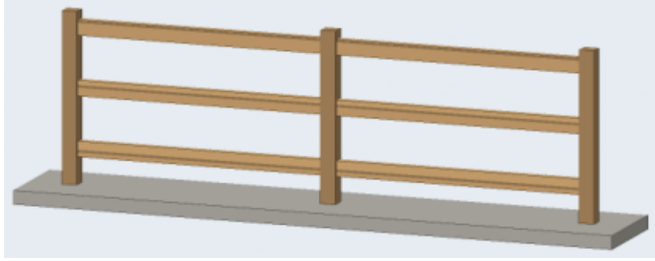

3 مرابيع أفقية (صورة 2)



قوائم رأسية متقاربة (صورة 1)

المشروع / العميل	عنوان اللوحة	المقياس	التاريخ	رقم اللوحة
مصنع وتد الأخشاب Watad Wood Factory **الخيار 3 — مجلس وصالة + غرفة — دورين بسطح علوي عميل — 3 خيارات**	**المنظور والمواد**	**—**	**2026-10-21**	**A-11 (11/11)**