

المنظور ثلاثي الأبعاد والمواد

النمط: جوزي غامق + إطارات سوداء — معاينة تقريبية، الإخراج النهائي من 3ds Max

جدول المواد والألوان

الخشب / الصبغة

صبغة جوزي غامق

القرميد

قرميد رمادي غامق

الزجاج

زجاج عاكس غامق

إطارات الشبابيك والأبواب

إطار ألومنيوم أسود

الكنار والزوايا

نفس الصبغة أعمق درجة

الصبة

خرسانة 45 سم

الدريزين: ألواح أفقية متقاربة (عصري)


تقسيم الشبابيك: بدون | الباب الرئيسي: سحب زجاج




أنواع الدريزين المعتمدة (من مشاريع المصنع)



قوائم رأسية متقاربة (صورة 1)

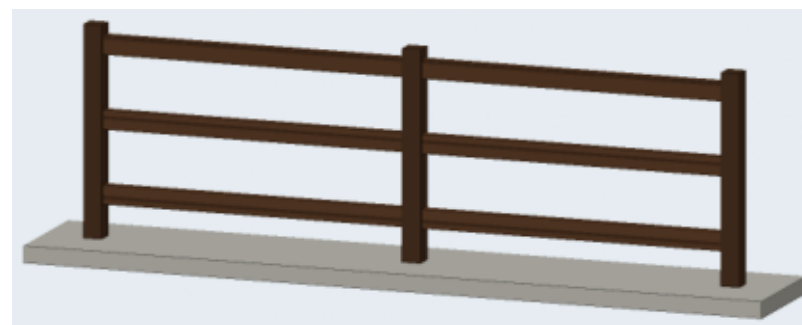

3 مربيع أفقية (صورة 2)

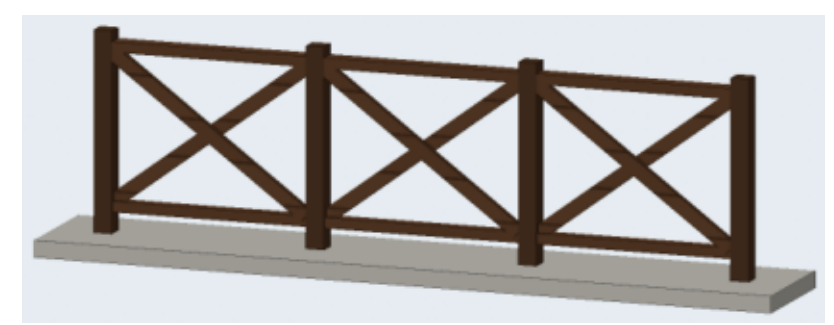

تقاطع X (صورة 5)

رقم اللوحة

W-01 (1/14)

التاريخ

2026-09-29

المقياس

1:50

عنوان اللوحة

المنظور والمواد

المشروع / العميل


كوخ غرفتين وتراس مسقوف 7.8×7.8
عميل — تصميم حسب الصورة

مصنع وتد الأخشاب
Watad Wood Factory




[illegible]

المشروع / العمل	عنوان اللوحة	المقياس	التاريخ	رقم اللوحة
كوخ غرفتين وتراس مسقوف 7.8×7.8 عمل – تصميم حسب الصورة	المسقط الأفقي	1:50	2026-09-29	W-02 (2/14)

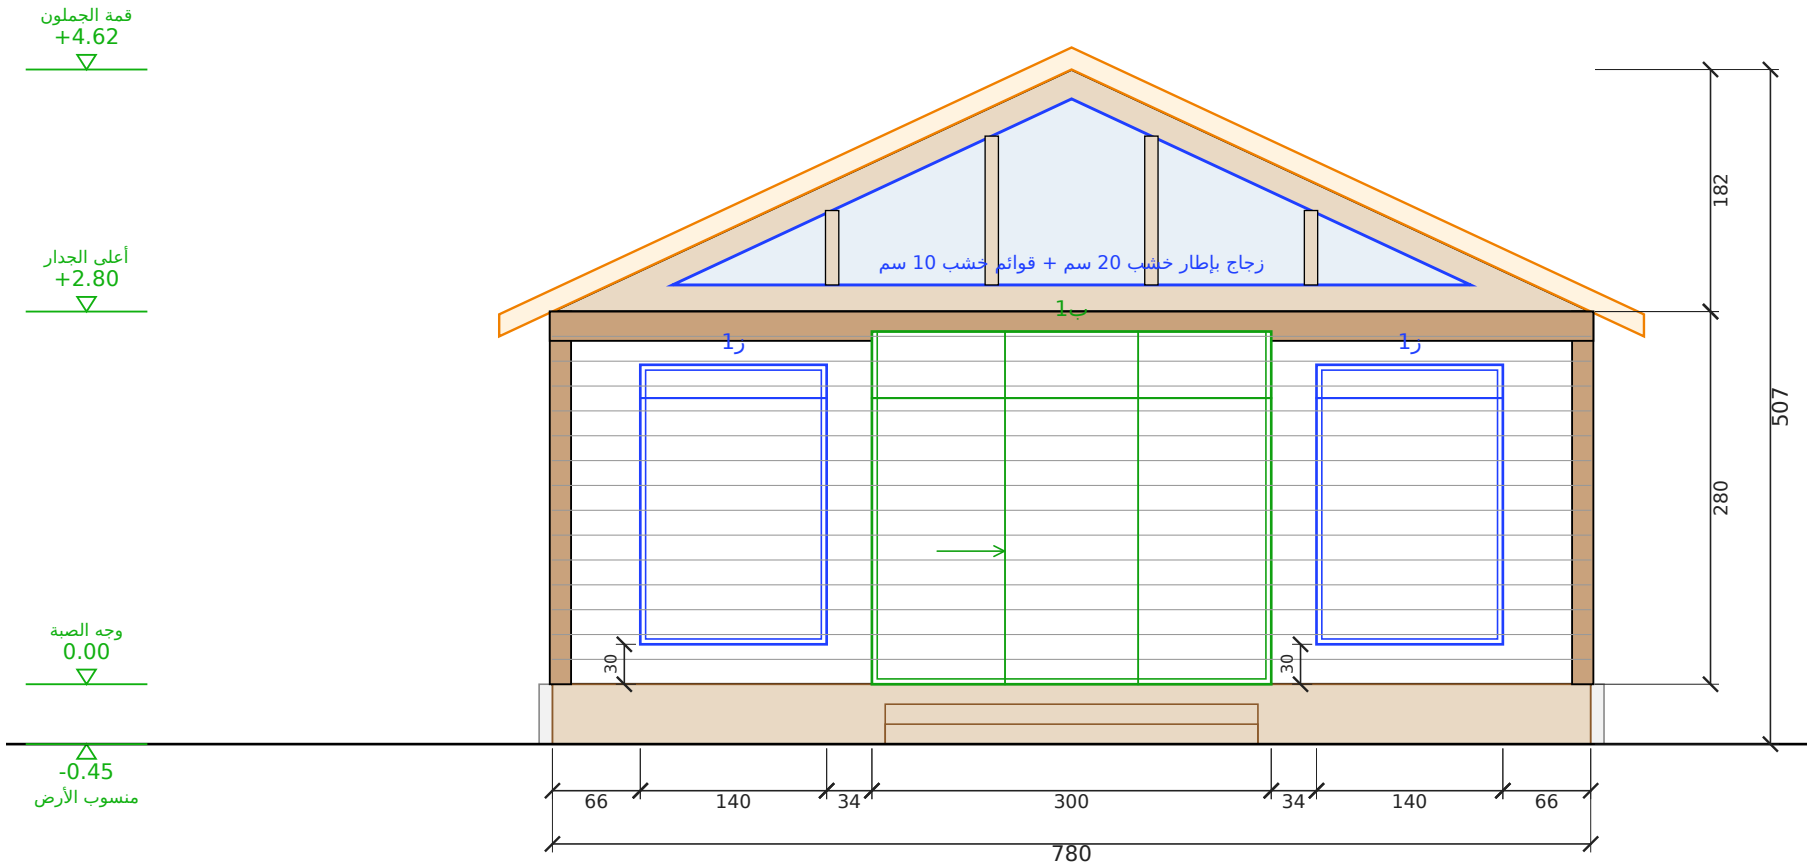

الواجهة الأمامية (التراس)


مقياس 1:50 | الوحدة: سم

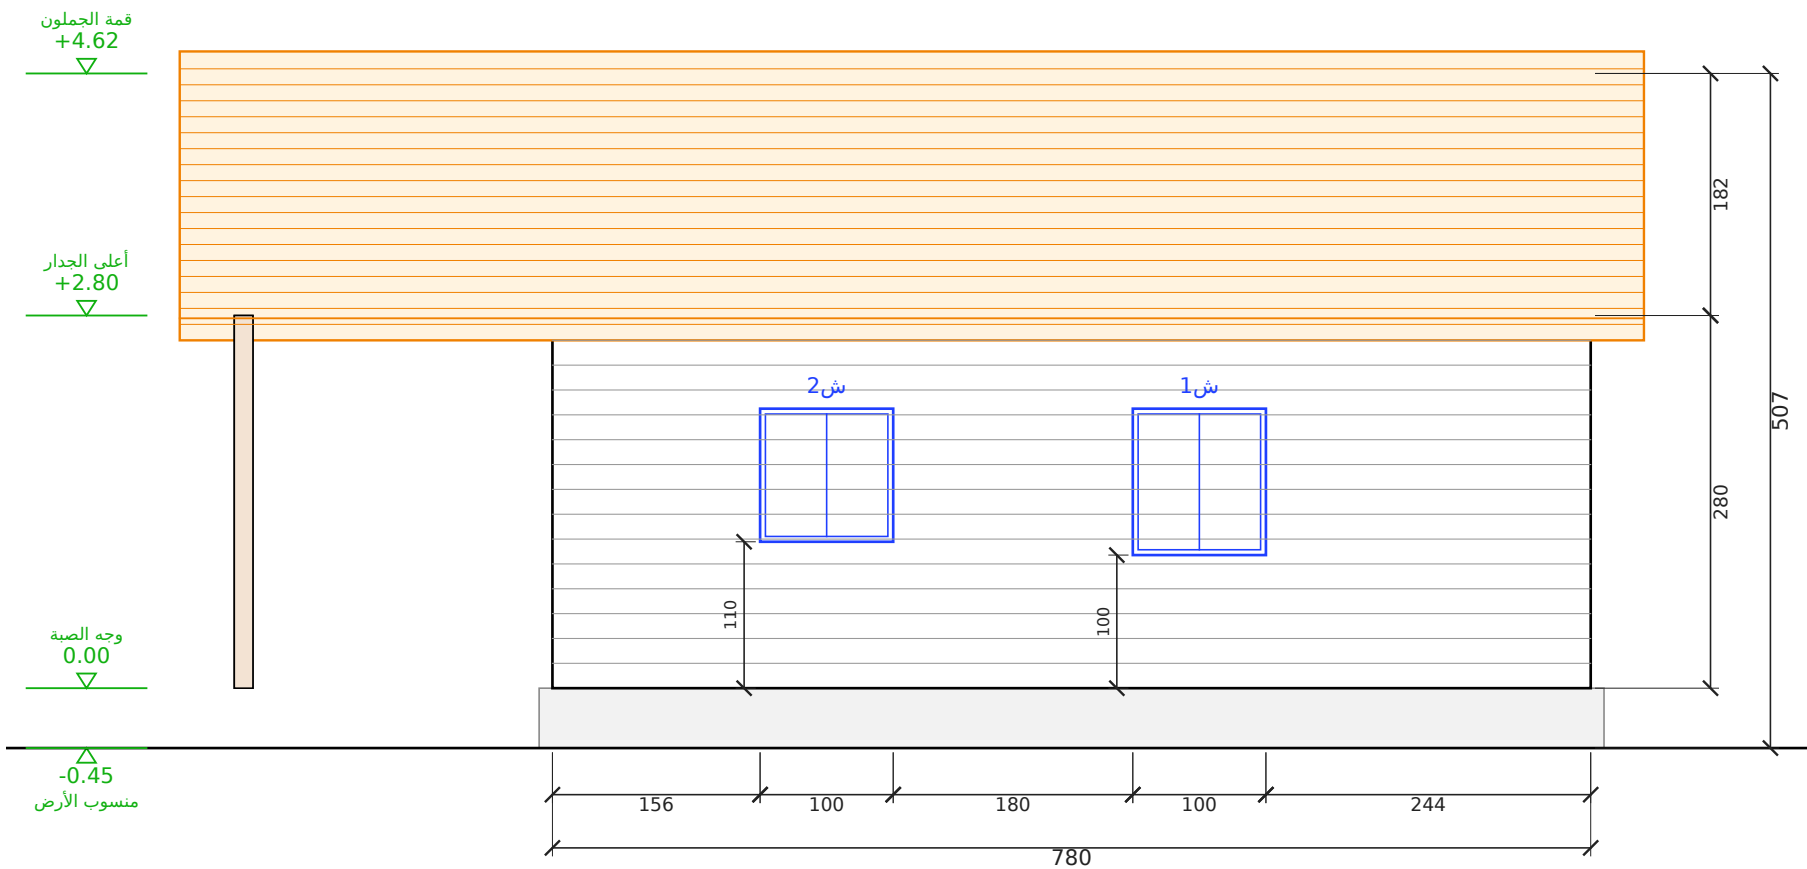

الواجهة الشرقية


مقياس 1:50 | الوحدة: سم

رقم اللوحة	التاريخ	المقياس	عنوان اللوحة	المشروع / العميل	مصنع وتد الأخشاب Watad Wood Factory
W-03 (3/14)	2026-09-29	1:50	الواجهة الأمامية (التراس) والواجهة الشرقية	كوخ غرفتين وتراس مسقوف 7.8x7.8 عميل - تصميم حسب الصورة	

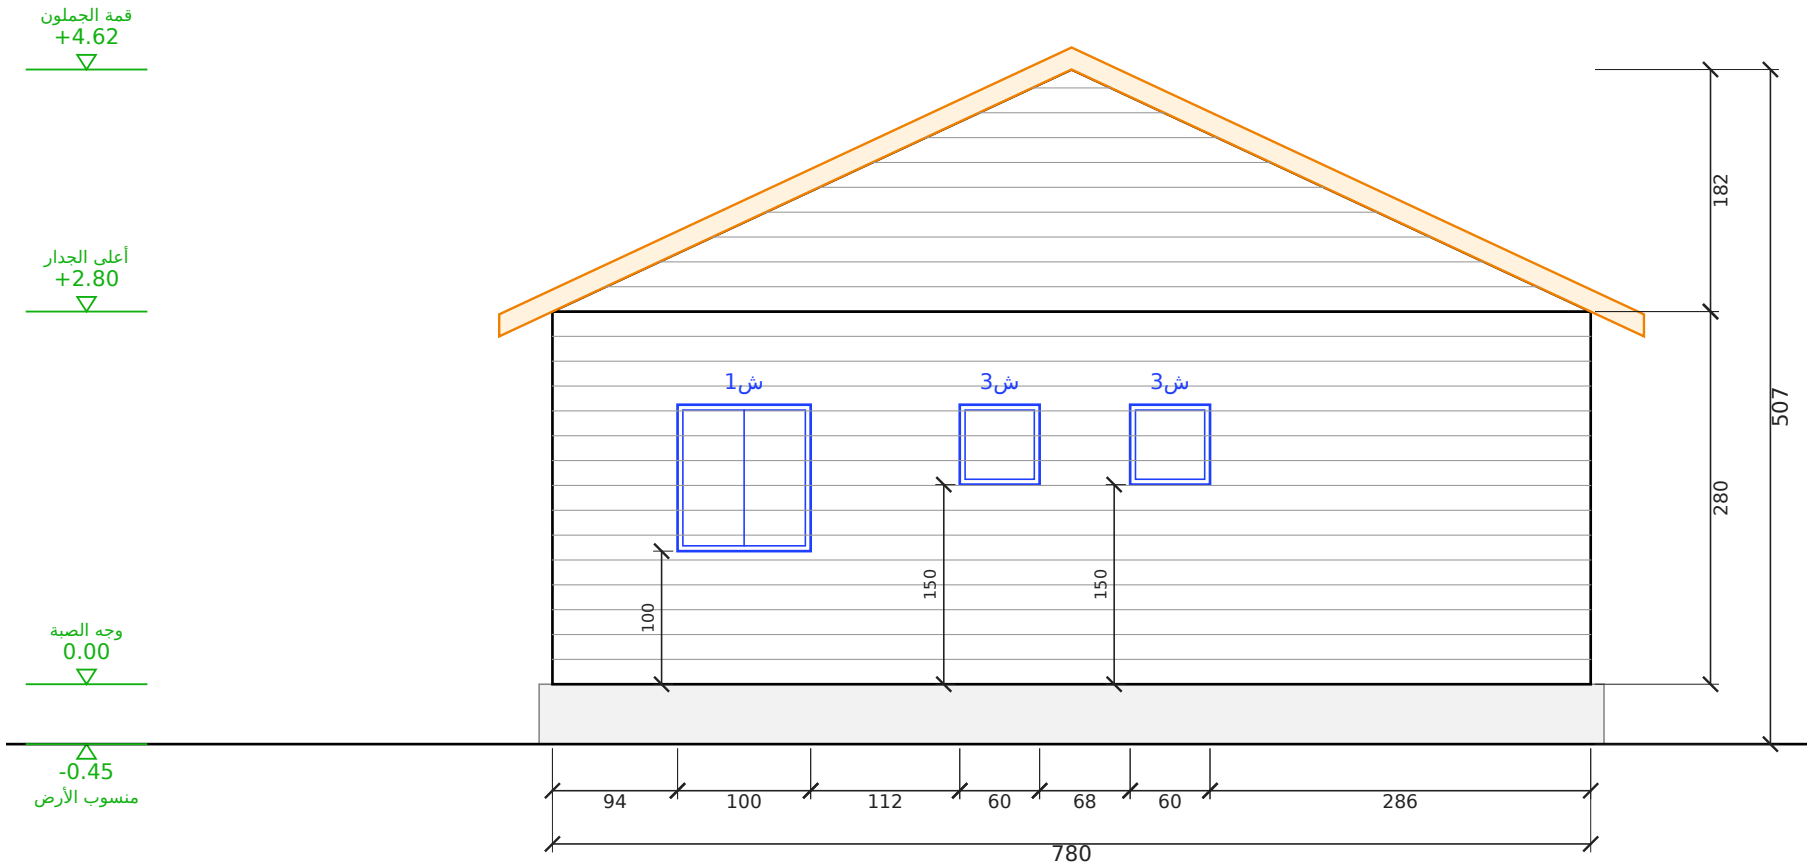

الواجهة الخلفية

مقياس 1:50 | الوحدة: سم

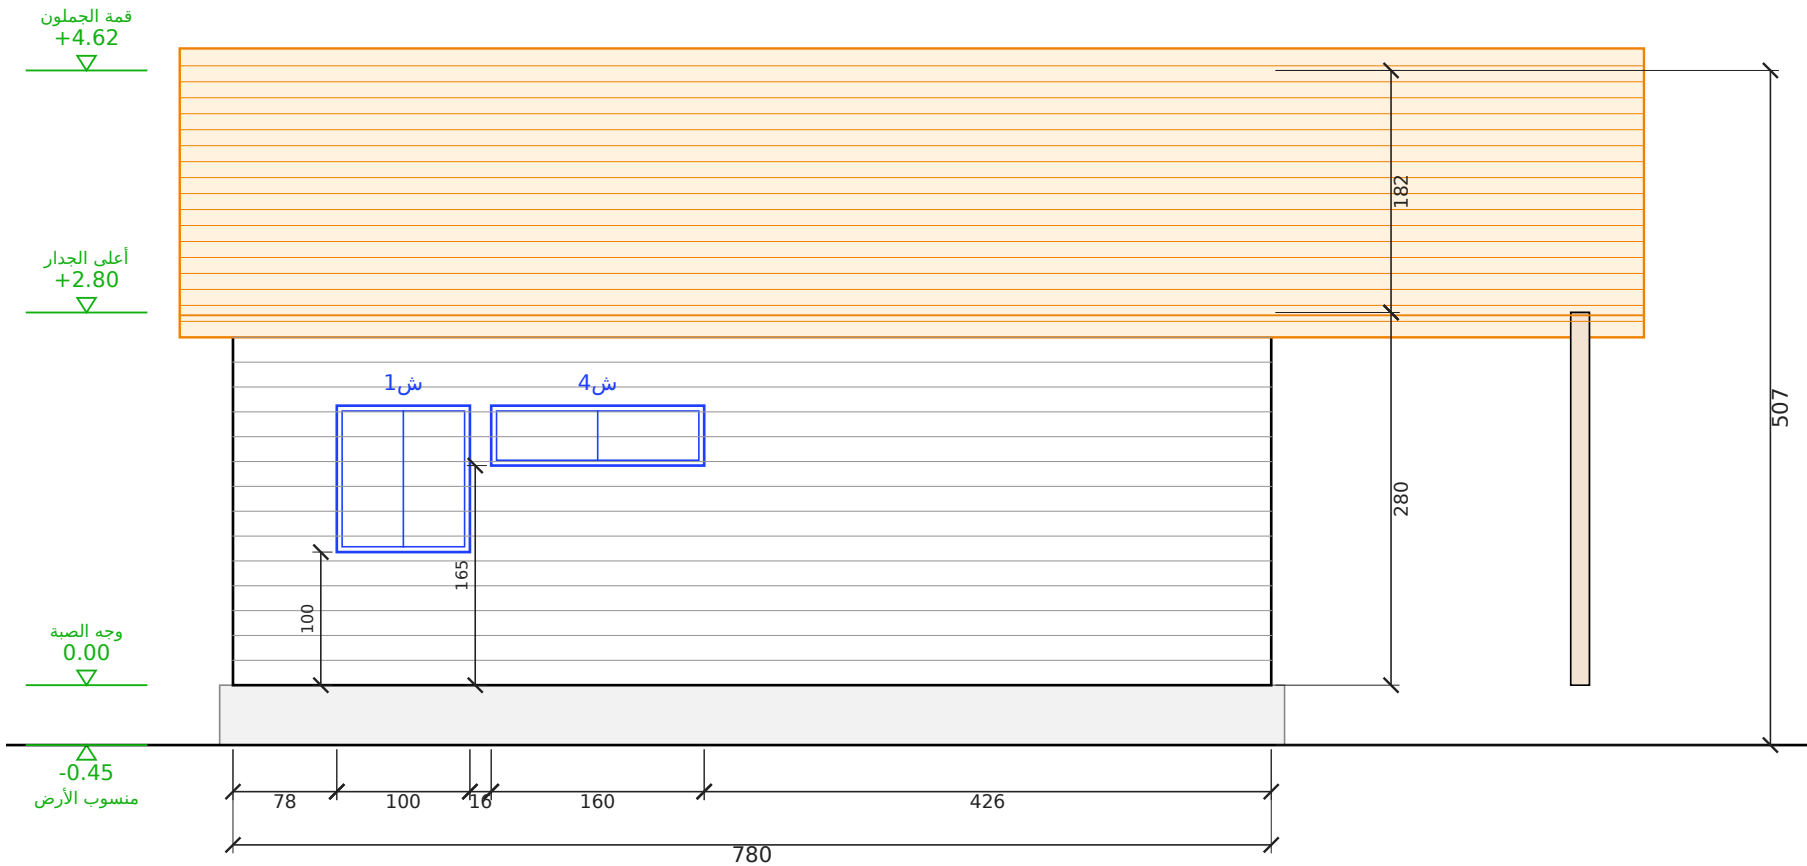


الواجهة الغربية


مقياس 1:50 | الوحدة: سم

رقم اللوحة	التاريخ	المقياس	عنوان اللوحة	المشروع / العميل	مصنع وتد الأخشاب Watad Wood Factory
W-04 (4/14)	2026-09-29	1:50	الواجهة الخلفية والواجهة الغربية	كوخ غرفتين وتراس مسقوف 7.8x7.8 عميل - تصميم حسب الصورة	


مسقط السقف (جملون)
رفرف 40 سم من كل جهة | مقياس 1:50

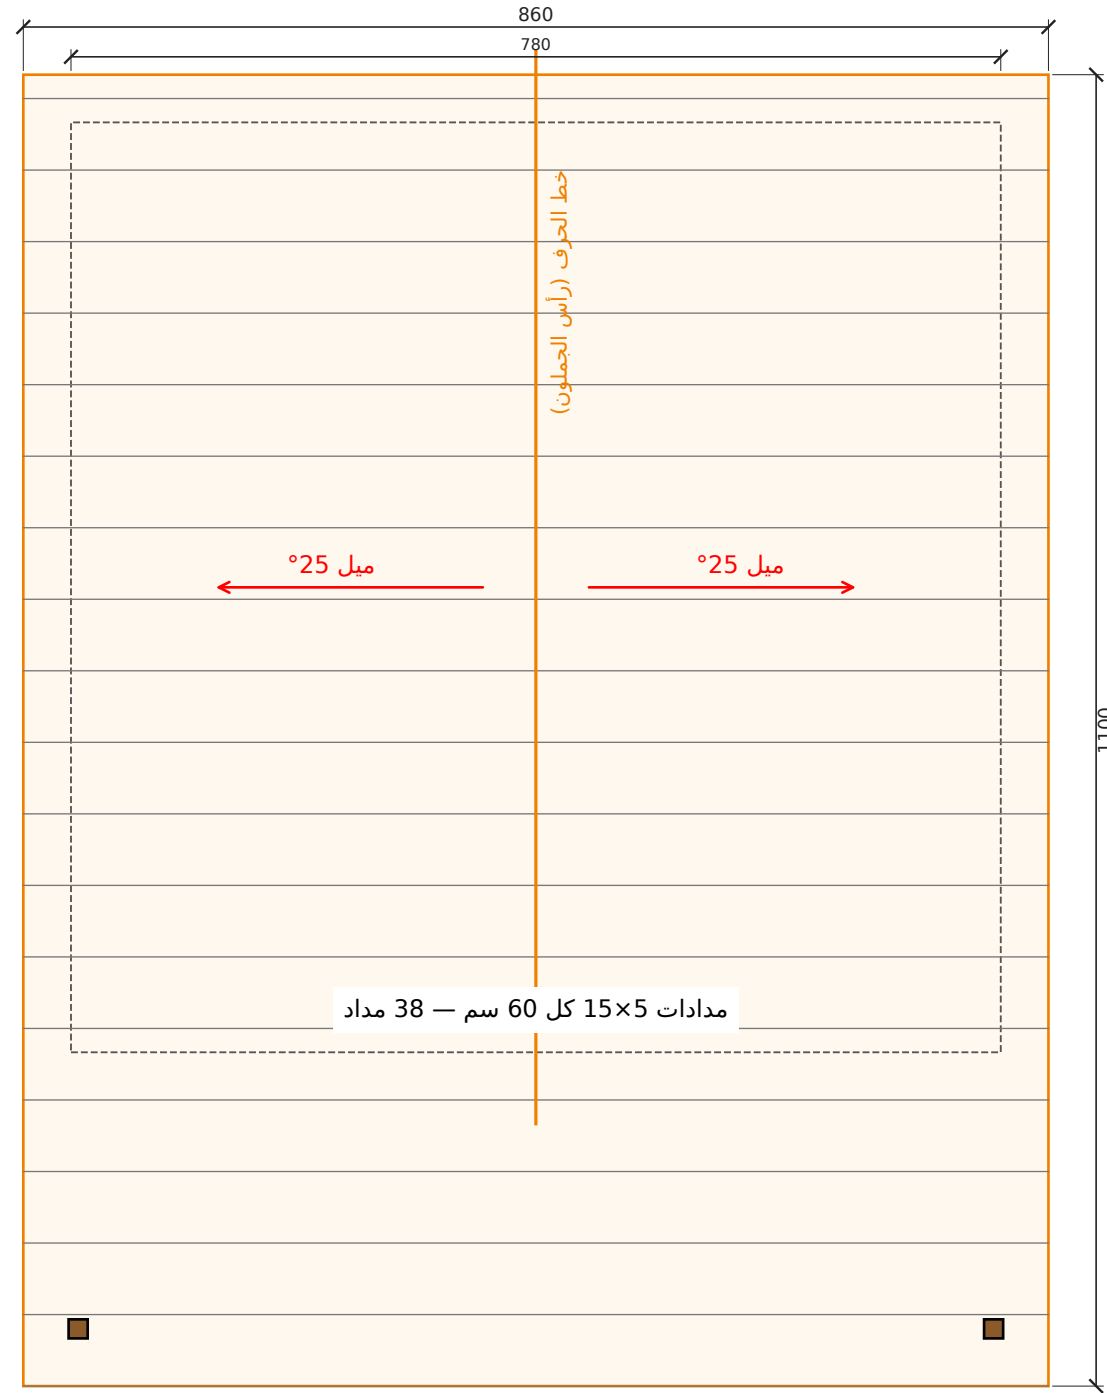

قطاع عرضي أ-أ
مقياس 1:50 | الوحدة: سم

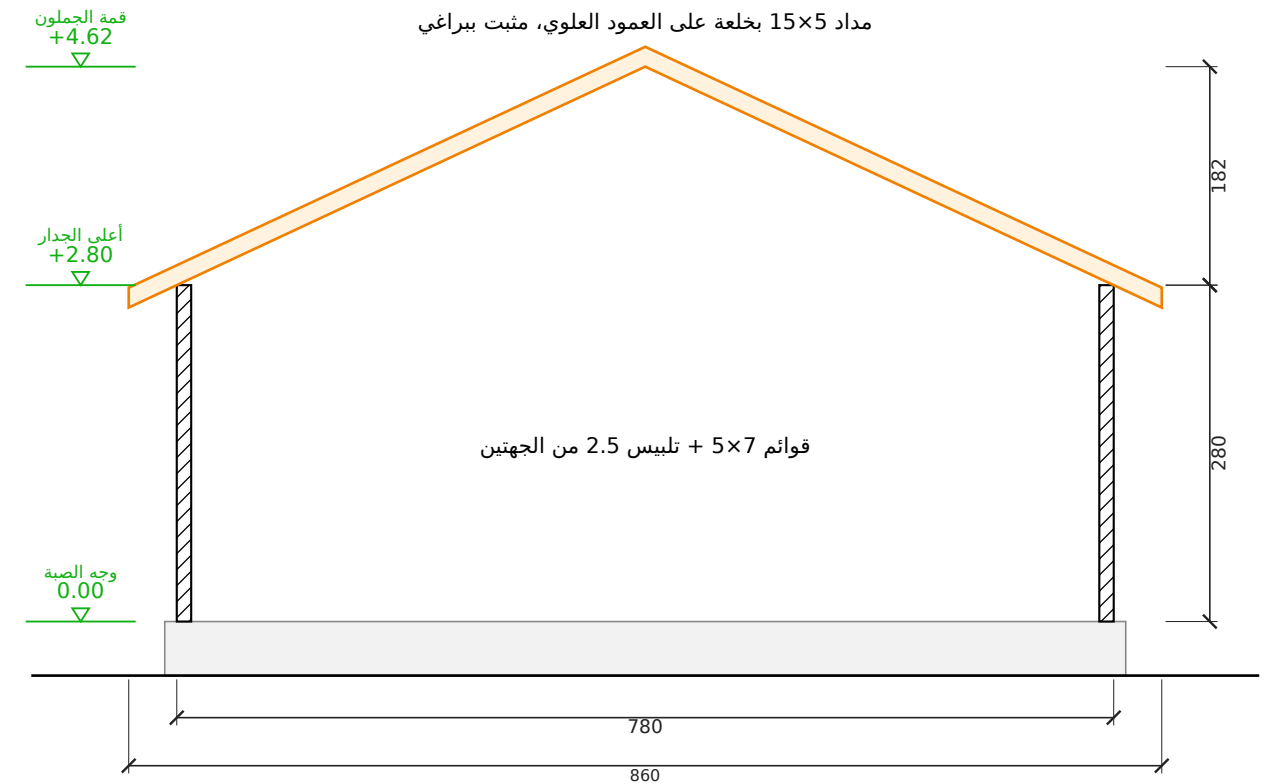

تفصيلة جلوس المداد على العلوي (1:5)

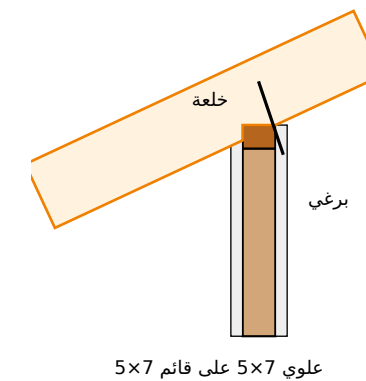

رقم اللوحة

W-05 (5/14)

التاريخ

2026-09-29

المقياس

1:50

عنوان اللوحة

مسقط السقف والقطاع

المشروع / العميل

كوخ غرفتين وتراس مسقوف 7.8×7.8
عميل — تصميم حسب الصورة

مصنع وتد الأخشاب
Watad Wood Factory



جدول مقاسات الأبواب والشبابيك
مقاس الفتحة الصافي في الجدار - الوحدة: سم

الرمز	النوع	العرض (سم)	الارتفاع (سم)	ارتفاع الجلسة (سم)	العدد	الموقع
ب1	باب	300	265	-	1	الأمامية (التراس)
ب2	باب	80	210	-	2	ماستر - غرفة 2
ب3	باب	70	210	-	2	حمام مشترك - حمام ماستر
ف1	باب	90	210	-	1	فتحة الممر
ز1	شباك	140	210	30	2	الأمامية (التراس) 2
ش1	شباك	100	110	100	3	الشرقية - الخلفية - الغربية
ش2	شباك	100	100	110	1	الشرقية
ش3	شباك	60	60	150	2	الخلفية 2
ش4	شباك	160	45	165	1	الغربية

الإجمالي: أبواب 6 - شبابيك 9

جدول المساحات وبيانات المشروع والتسعير

جدول المساحات

م	الفراغ	الأبعاد (م)	المساحة (م2)
1	الصالة ومطبخ الخدمة	7.56 × 3.30	24.95
2	غرفة الماستر	3.60 × 4.14	11.79
3	حمام الماستر	1.50 × 1.80	2.70
4	ممر	1.20 × 1.92	2.30
5	حمام مشترك	1.20 × 2.10	2.52
6	غرفة 2	2.52 × 4.14	10.43
	المساحة الصافية الداخلية		54.70
	التراس المسقوف	7.80 × 2.40	18.72
	المساحة الإجمالية المبنية	7.80 × 7.80	60.84

بيانات المشروع

البند	البيان
المشروع	كوخ غرفتين وتراس مسقوف 7.8×7.8
العميل	عميل — تصميم حسب الصورة
الموقع	—
الاستخدام	استراحة / استجمام
التاريخ	2026-09-29
نظام البناء	هيكل خشب 5×7 + تليس 2.5 سم من الجهتين
السقف	جملون 25° — قرميد معدني

التسعير


عرض اليوم الوطني

البند	القيمة
المساحة المبنية (م2)	60.84
سعر المتر المربع — عرض اليوم الوطني	1,096 ريال
الإجمالي	66,681 ريال


ملاحظات:

- السعر للمساحة المبنية حسب المخطط المعتمد.
- الصبة والتوريدات الخارجية على العميل ما لم يُذكر غير ذلك.

تأطير جدار جنوب — الطول 768 سم، الارتفاع 280 سم

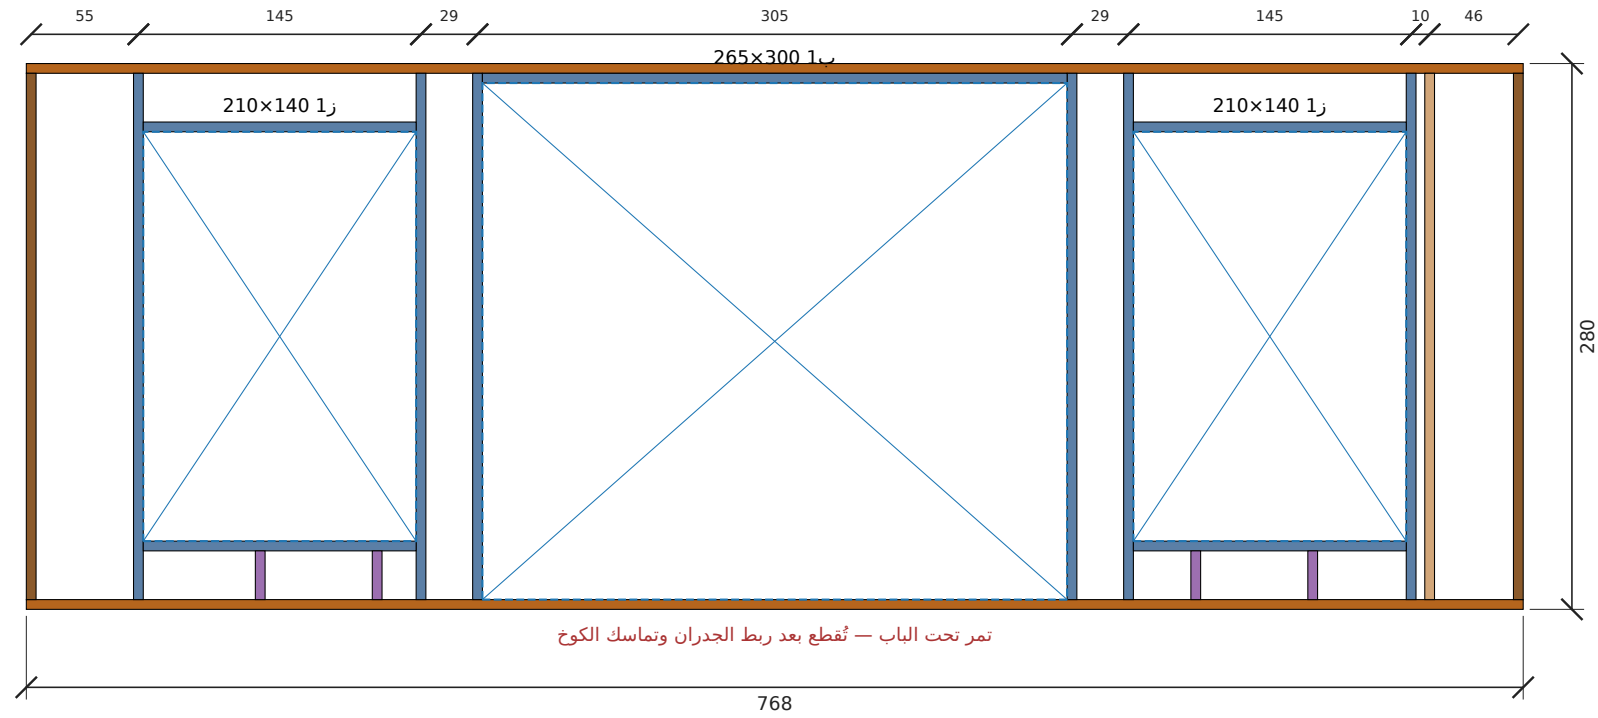

تأطير جدار شرق — الطول 768 سم، الارتفاع 280 سم

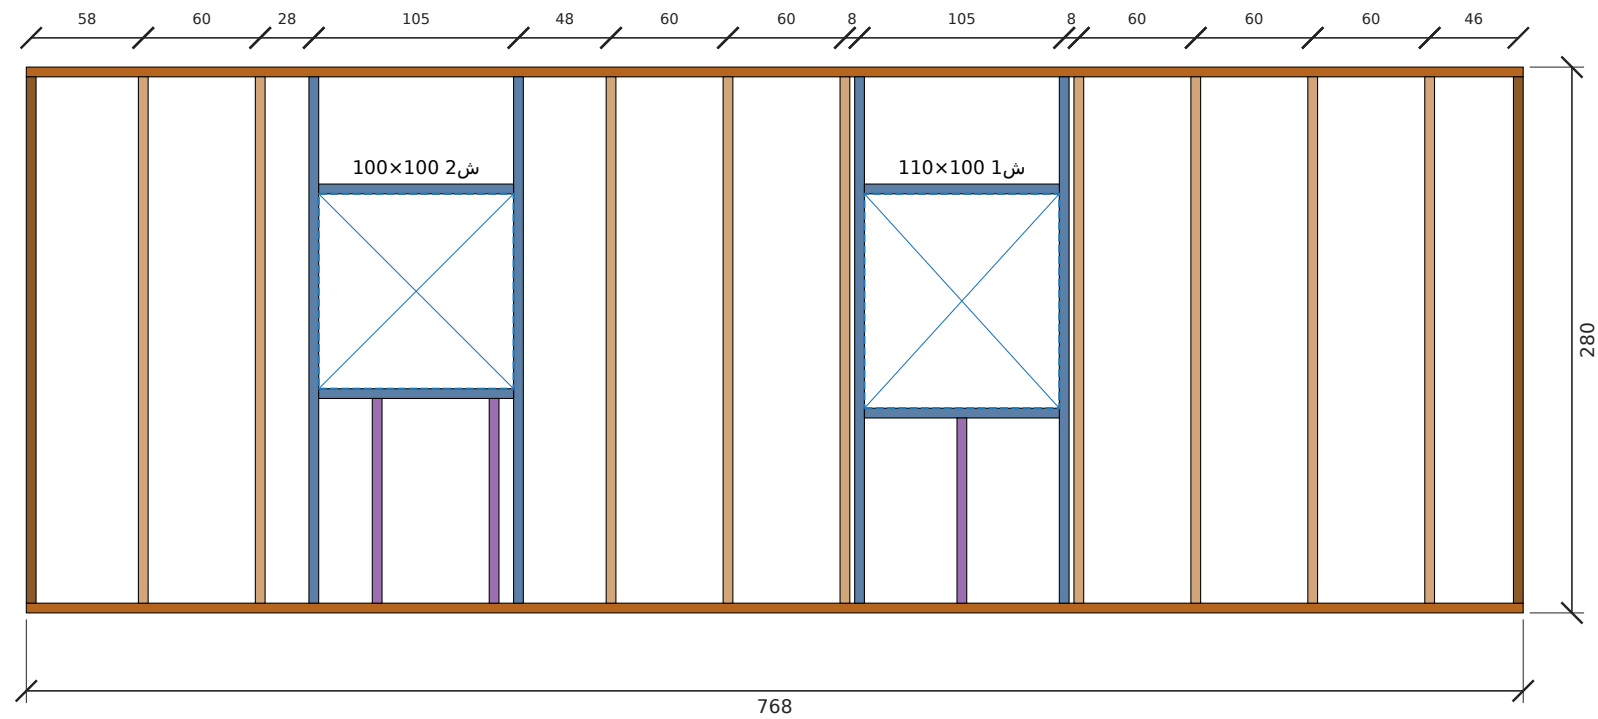

قاعدة سفلية علوي عمود عمود زاوية جنب فتحة رأس فتحة جلسة شباك عمود قصير

رقم اللوحة

W-08 (8/14)

التاريخ

2026-09-29

المقياس

—

عنوان اللوحة

لوحات التأطير (للورشة)


المشروع / العميل

كوخ غرفتين وتراس مسقوف 7.8x7.8
عميل — تصميم حسب الصورة


مصنع وتد الأخشاب
Watad Wood Factory



تأطير جدار شمال — الطول 768 سم، الارتفاع 280 سم

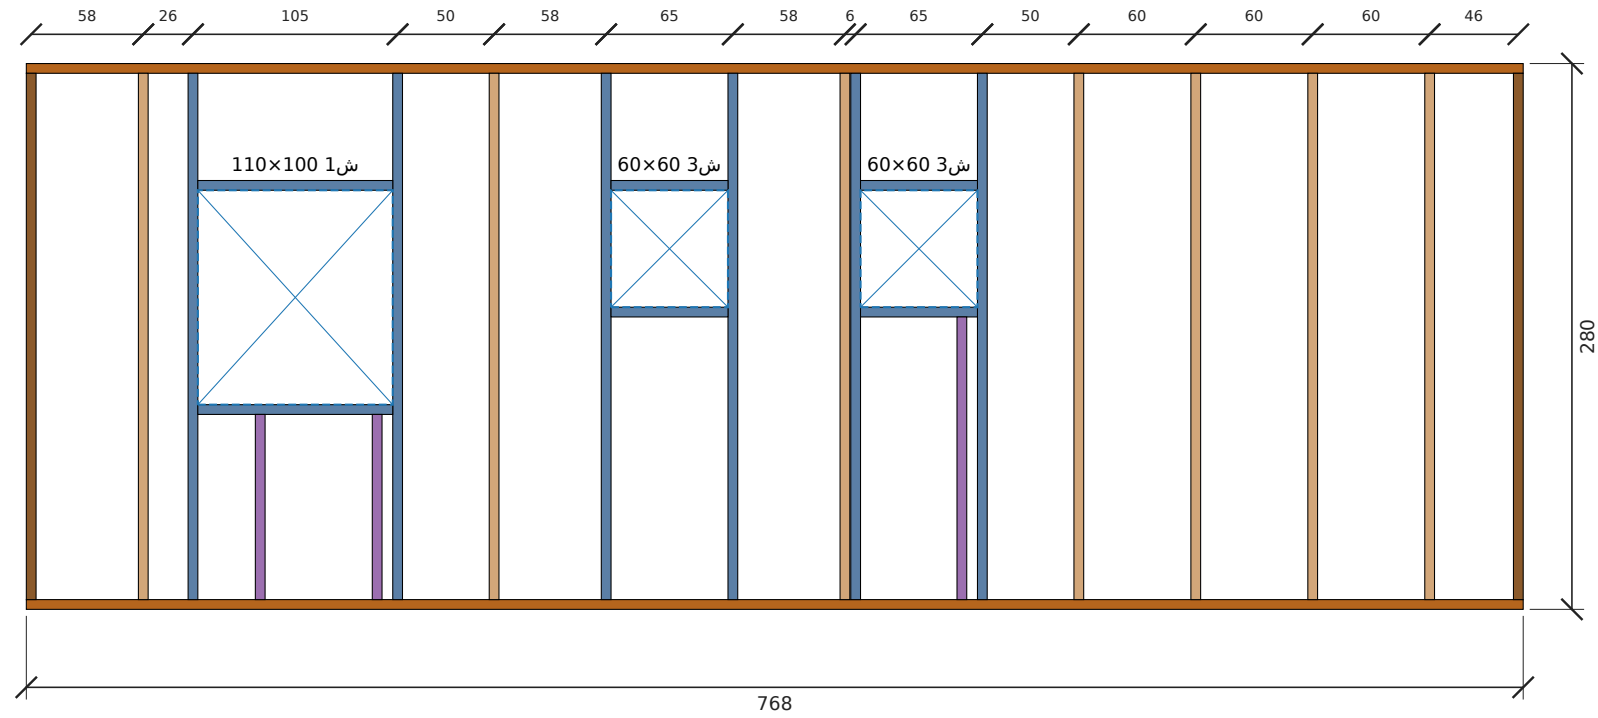

تأطير جدار غرب — الطول 768 سم، الارتفاع 280 سم

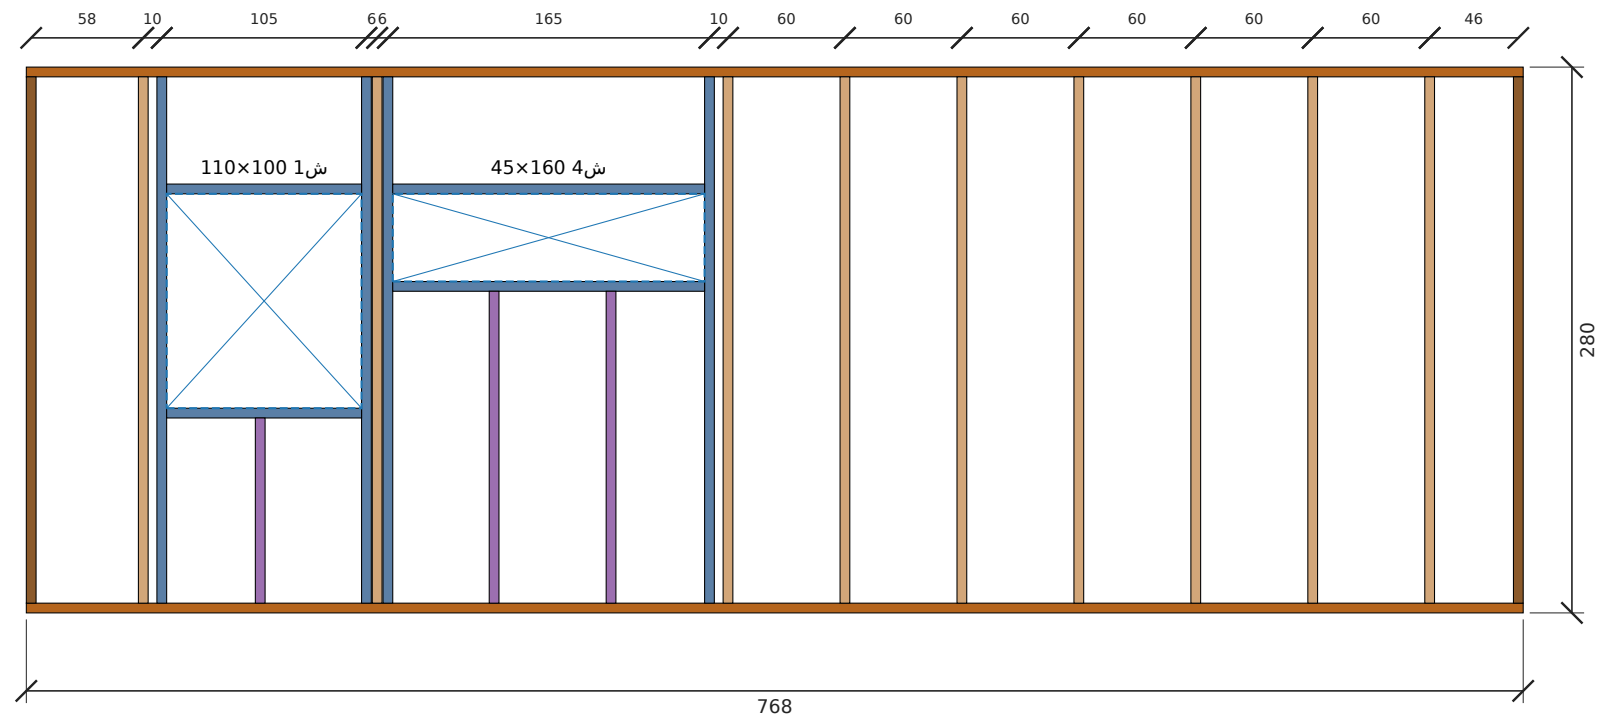

قاعدة سفلية علوي عمود عمود زاوية جنب فتحة رأس فتحة جلسة شباك عمود قصير

رقم اللوحة

W-09 (9/14)

التاريخ

2026-09-29

المقياس

—

عنوان اللوحة

لوحات التأطير (للورشة)


المشروع / العميل

كوخ غرفتين وتراس مسقوف 7.8x7.8
عميل — تصميم حسب الصورة


مصنع وتد الأخشاب
Watad Wood Factory



تأطير جدار د1-فاصل الصالة — الطول 768 سم، الارتفاع 280 سم (داخلي)

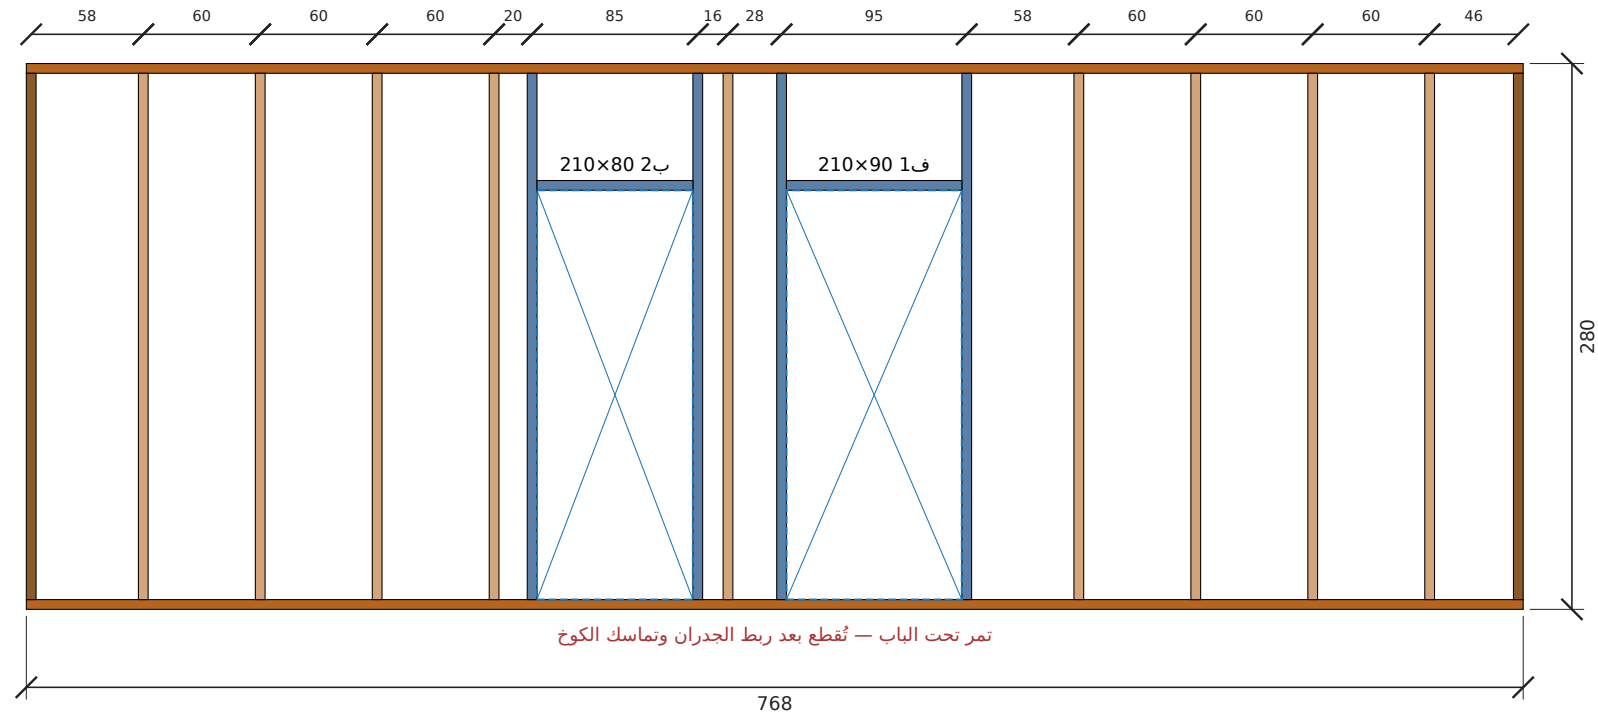

تأطير جدار د2-جدار النواة — الطول 426 سم، الارتفاع 280 سم (داخلي)

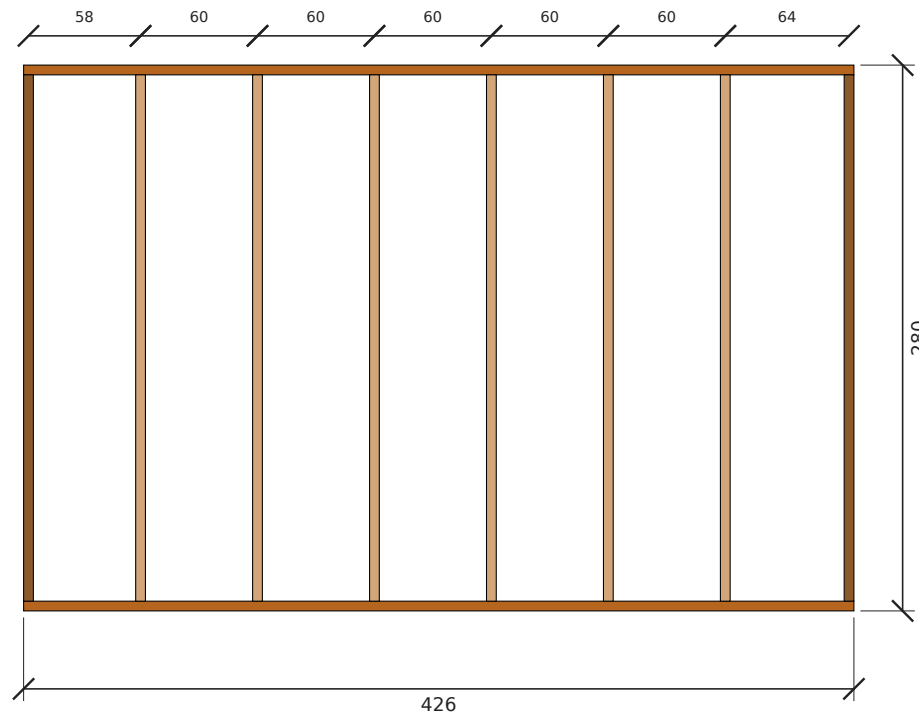

■ قاعدة سفلية
 ■ علوي
 ■ عمود
 ■ عمود زاوية
 ■ جنب فتحة
 ■ رأس فتحة
 ■ جلسة شباك
 ■ عمود قصير

رقم اللوحة

W-10 (10/14)

التاريخ

2026-09-29

المقياس

—

عنوان اللوحة

لوحات التأطير (للورشة)


المشروع / العميل

كوخ غرفتين وتراس مسقوف 7.8×7.8
عميل — تصميم حسب الصورة


مصنع وتد الأخشاب
Watad Wood Factory



تأطير جدار د3-غرفة 2 — الطول 426 سم، الارتفاع 280 سم (داخلي)

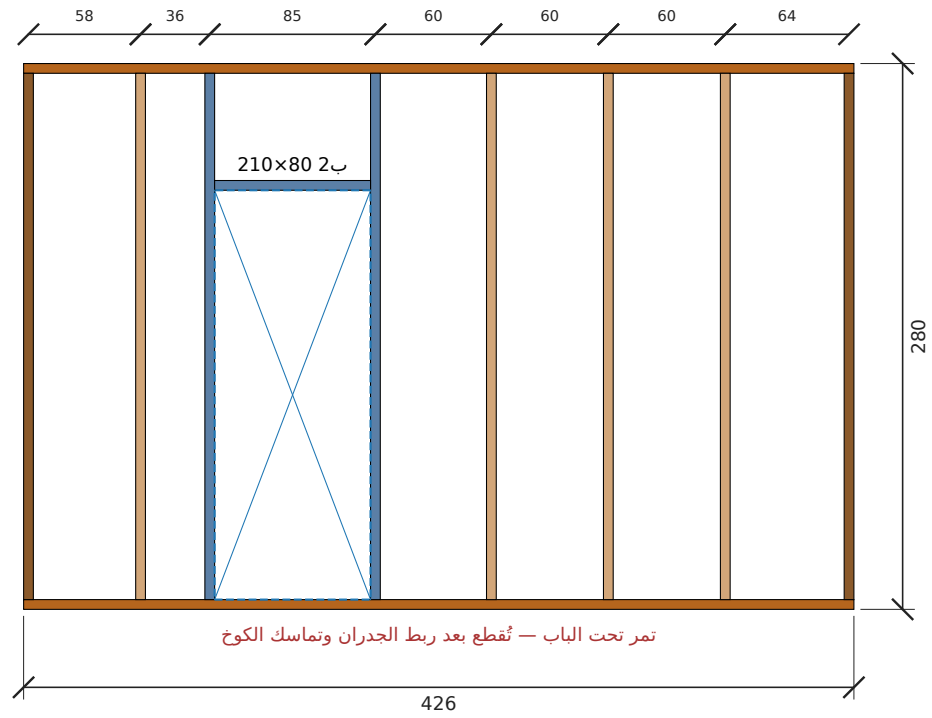

تأطير جدار د4-حمام مشترك — الطول 132 سم، الارتفاع 280 سم (داخلي)

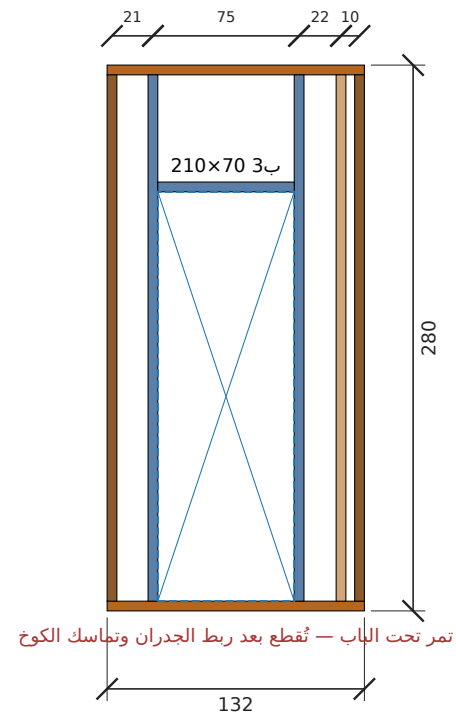

قاعدة سفلية علوي عمود عمود زاوية جنب فتحة رأس فتحة جلسة شباك عمود قصير

رقم اللوحة

W-11 (11/14)

التاريخ

2026-09-29

المقياس

—

عنوان اللوحة

لوحات التأطير (للورشة)


المشروع / العميل

كوخ غرفتين وتراس مسقوف 7.8x7.8
عميل — تصميم حسب الصورة


مصنع وتد الأخشاب
Watad Wood Factory



تأطير جدار د5-حمام ماستر جنوب — الطول 162 سم، الارتفاع 280 سم (داخلي)

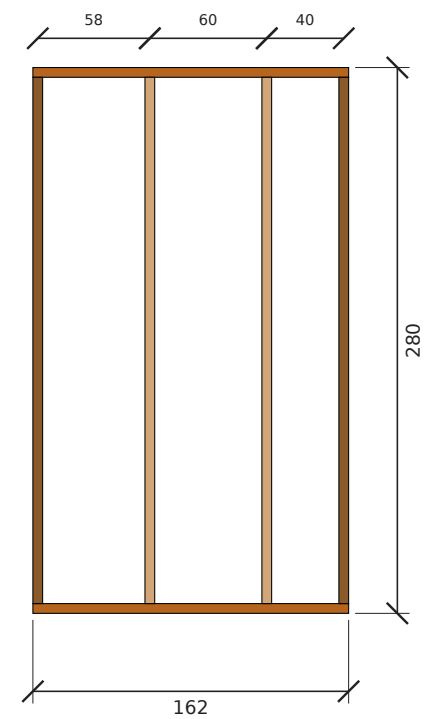

تأطير جدار د6-حمام ماستر غرب — الطول 192 سم، الارتفاع 280 سم (داخلي)

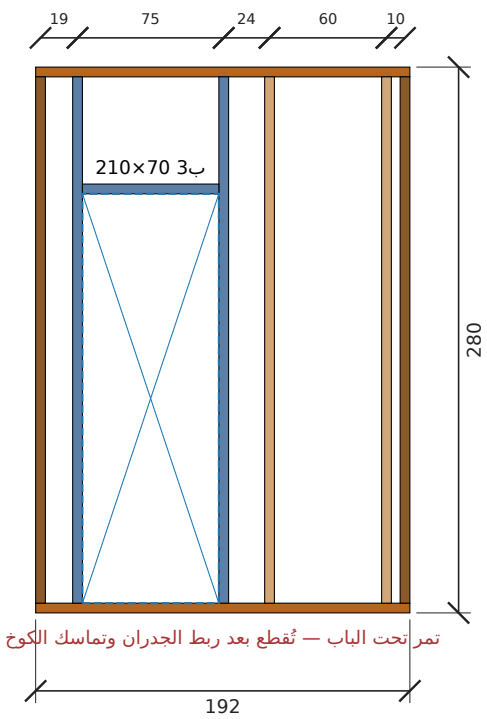

عمود قصير / عمود زاوية / عمود علوي / قاعدة سفلية / جنب فتحة / رأس فتحة / جلسة شباك / تمر تحت الباب — تُقطع بعد ربط الجدران وتماسك الكوخ

المشروع / العميل	عنوان اللوحة	المقياس	التاريخ	رقم اللوحة	مصنع وتد الأخشاب Watad Wood Factory
كوخ غرفتين وتراس مسقوف 7.8×7.8 عميل — تصميم حسب الصورة	لوحات التأطير (للورشة)	—	2026-09-29	W-12 (12/14)	

جدول الكميات وخطة تقطيع الطبلیات

البند	القيمة
الارتفاع المطلوب / المعتمد	280 / 280 سم
السقف	جملون 25° — قمة 462 سم من وجه الصبة
المدادات 15×5	38 مداد (19 لكل جهة) × 474 سم — من طبلية 480
طبلیات الطريقة الأولى (مداد + عمود)	38 طبلية × 480 سم
طبلیات الطريقة الثانية (3 أعمدة)	31 طبلية × 320 سم
إجمالي الطبلیات 22.5×5	69
إجمالي قطع 5×7	157
قائمة تقطيع 5×7	768سم×10 426سم×4 300سم×1 270سم×100 192سم×2 162سم×2 160سم×4 145سم×1 140سم×4
	132سم×2 105سم×2 100سم×8 95سم×4 90سم×1 80سم×2 70سم×2 60سم×4 25سم×4
ألواح تلييس 2.5 سم	280 لوح × 400 سم (مجموع الصفوف 1047.4 م، 20 وجه)
أسمنت بورد 12 مم (244×122)	28 لوح (داخل دورات المياه)
العزل	بدون (غير مطلوب)
الصبة	يجهزها العميل — 20 سم، مفرغة تحت دورات المياه

مراجعة التصميم مقابل قواعد المصنع

النوع	البند	التفاصيل	المقترح
ملاحظة	بحر المدادات	أطول بحر بدون جدار داخلي يحمل المداد: جهة أ: 390 سم، جهة ب: 390 سم. يحتاج رقم المصنع لأقصى بحر مسموح لتحديد المدادات اللي تُقوّى 5×20.	
ملاحظة	الصبة والدرج	ارتفاع الصبة 45 سم ← 3 درجة بقائمة 15.0 سم.	
ملاحظة	مناسيب رؤوس الفتحات	رؤوس الأبواب والشبابيك على مناسيب مختلفة: 210، 240، 265 سم.	
سؤال	يحتاج تأكيد	أقصى بحر للمداد بدون جدار داخلي قبل إضافة تقوية 5×7 (مداد 5×20)؟	
سؤال	يحتاج تأكيد	التغطية الصافية للوح التليس بعد التعشيق (مستنتجة مؤقتاً 18.67 سم من 280/15)؟	
سؤال	يحتاج تأكيد	هل يوضع أعمدة قصيرة فوق رأس الشباك/الباب إلى العلوي؟	
سؤال	يحتاج تأكيد	مكان الوصلة في القاعدة والعلوي إذا الجدار أطول من الطلبية؟	