



الأبعاد بالسنتيمتر - الجدران: قوائم 5×7 + تلبيس 2.5 من الجهتين (12 سم)

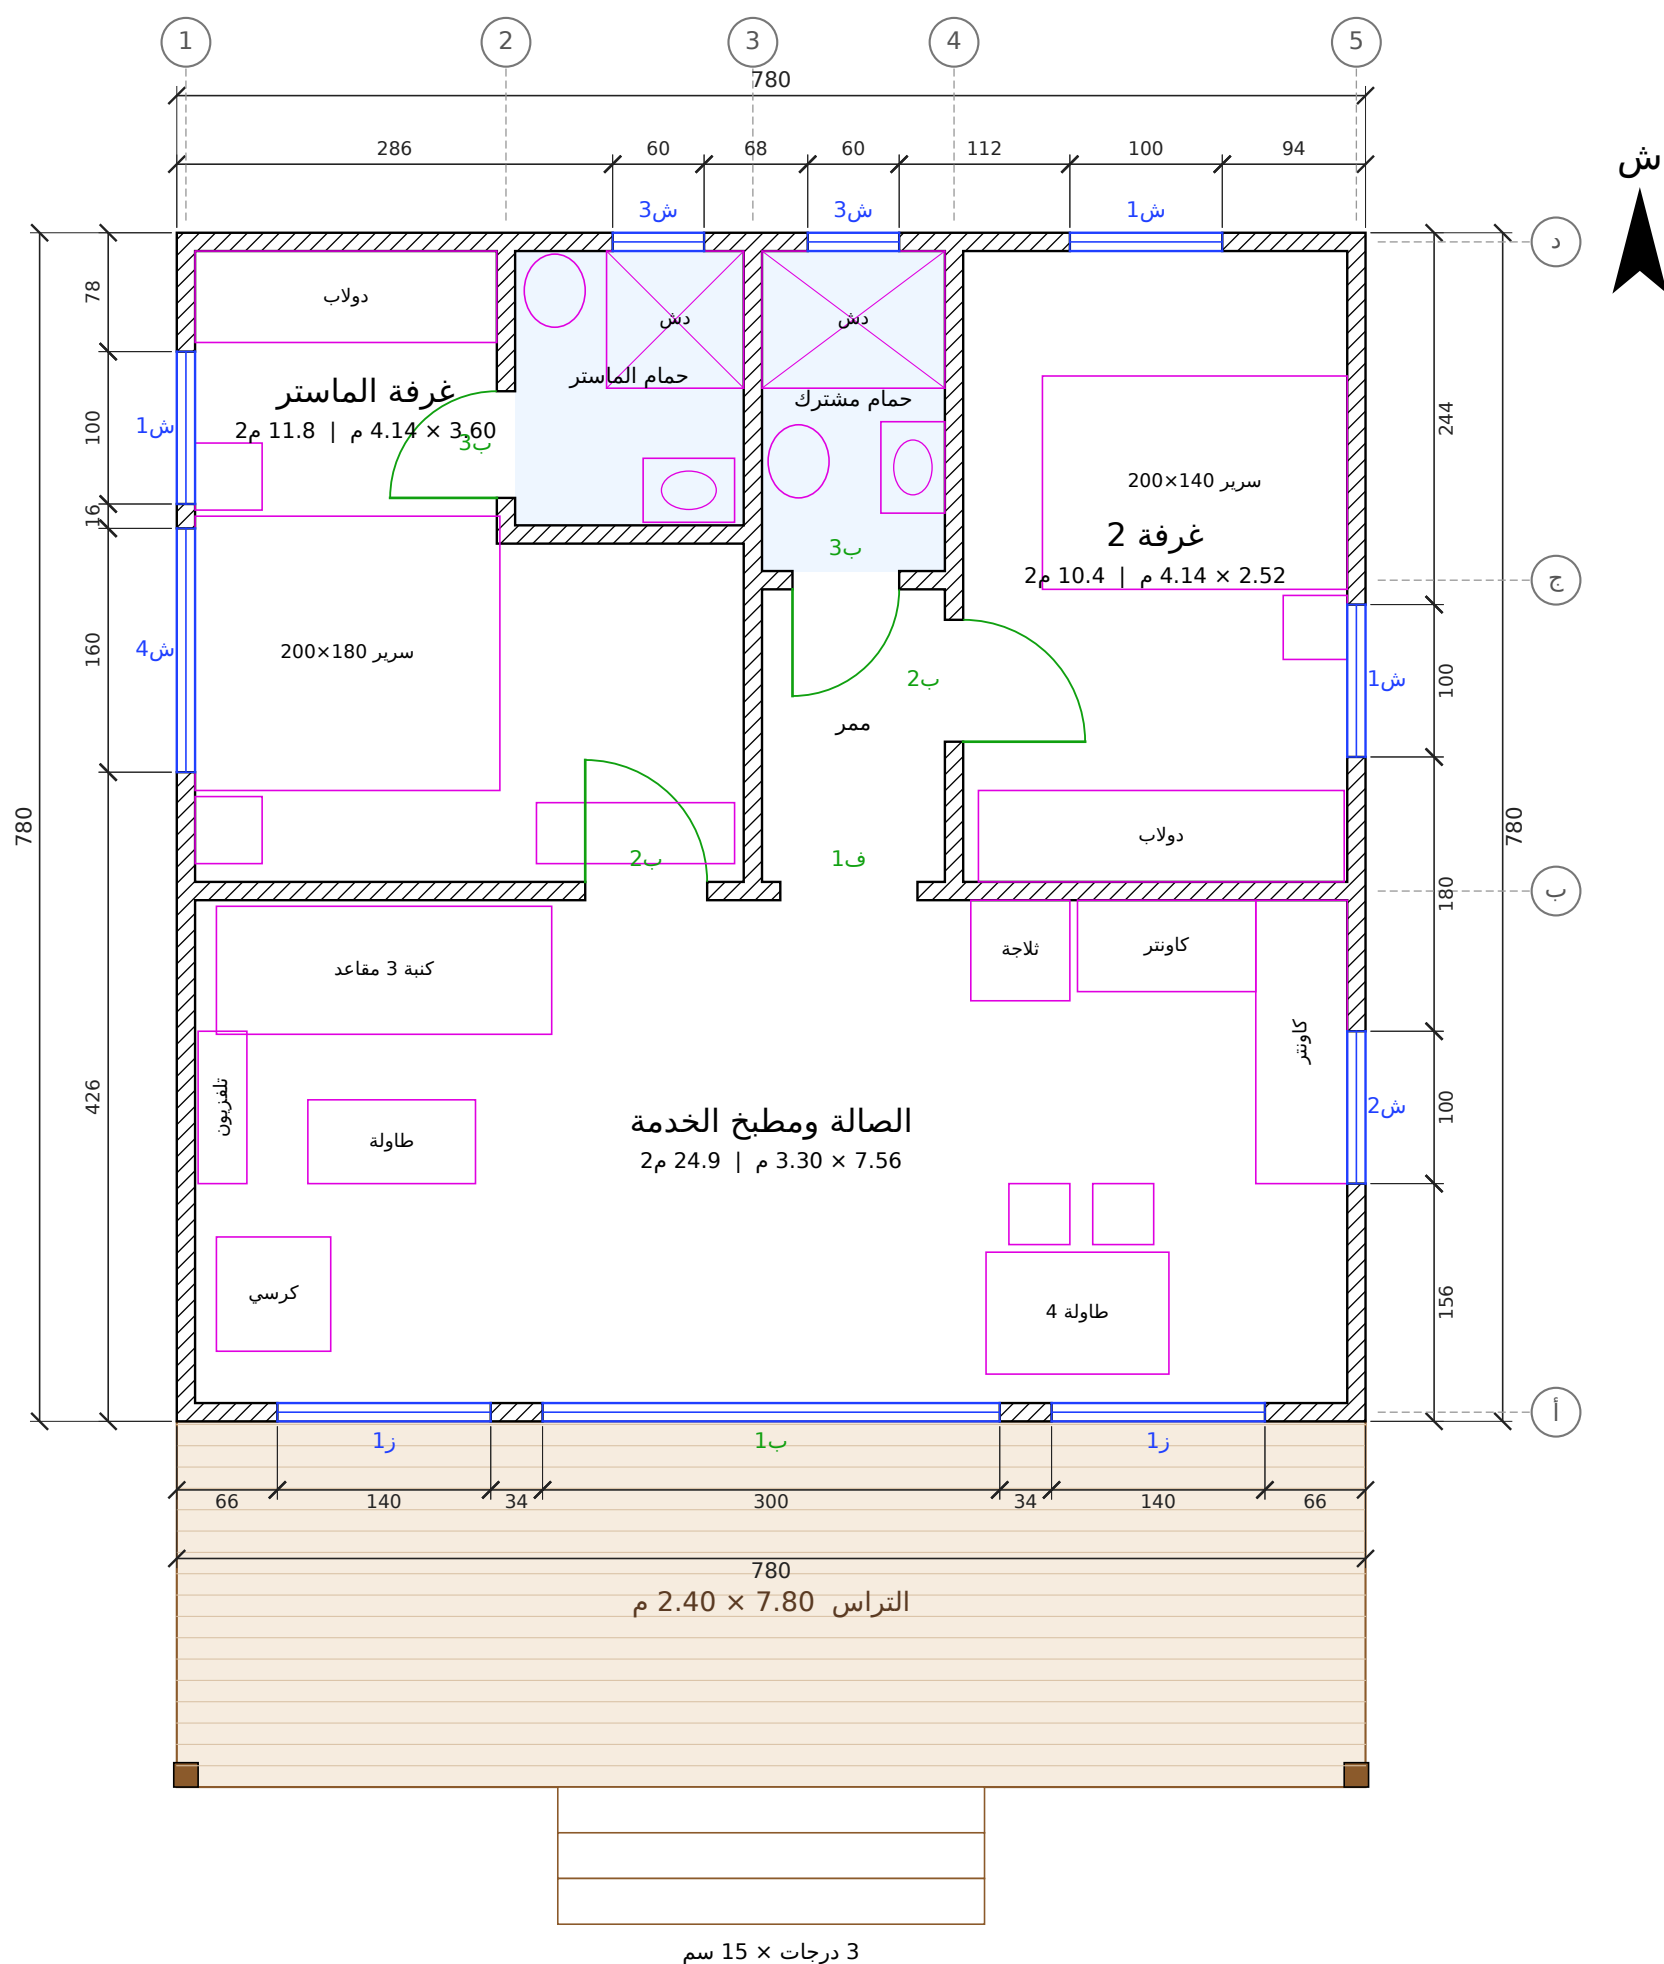


المشروع / العمل	عنوان اللوحة	المقياس	التاريخ	رقم اللوحة
كوخ غرفتين وتراس مسقوف 7.8×7.8 عمل – تصميم حسب الصورة	المسقط الأفقي	1:50	2026-09-29	A-01 (1/10)

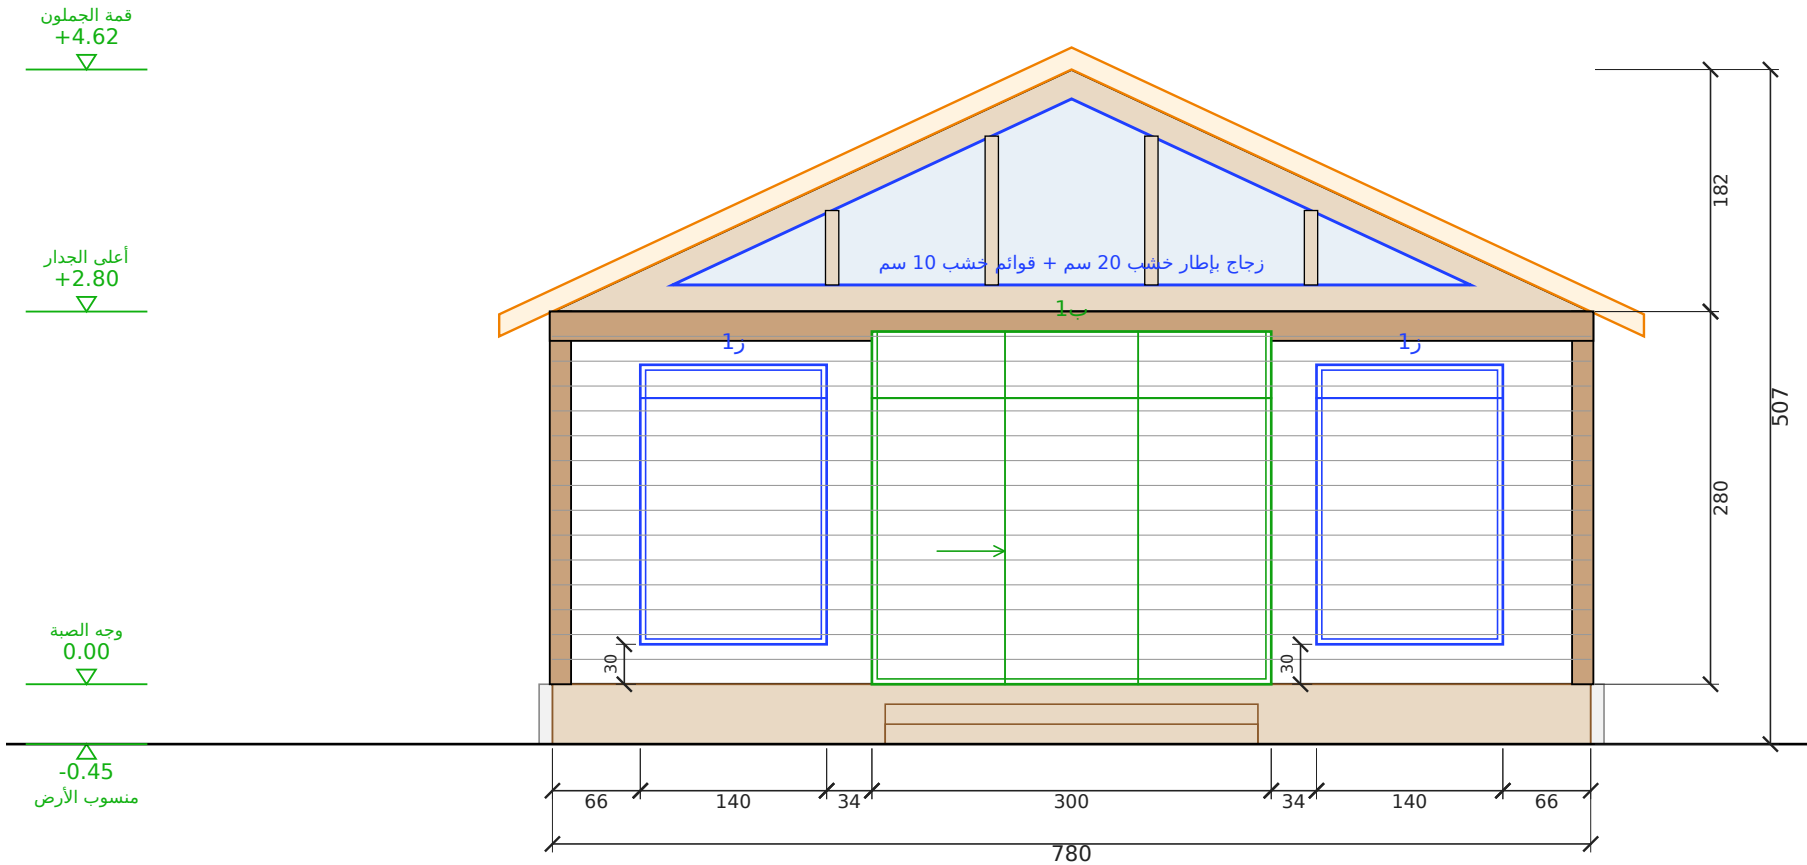

الواجهة الأمامية (التراس)


مقياس 1:50 | الوحدة: سم

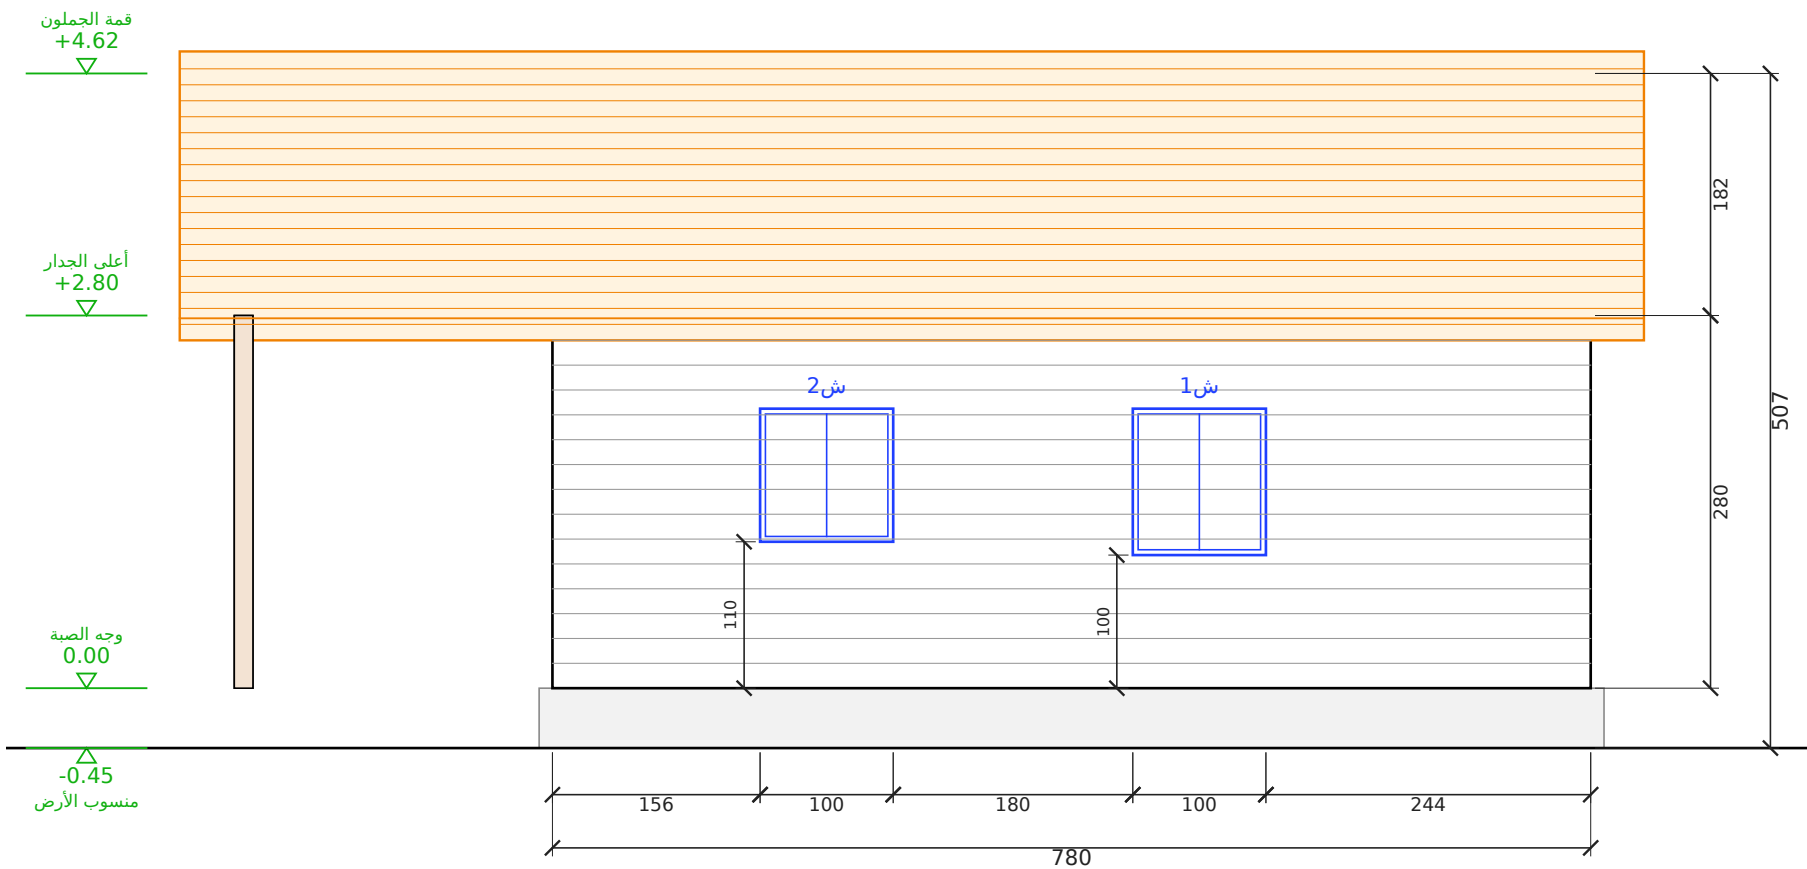

الواجهة الشرقية


مقياس 1:50 | الوحدة: سم

رقم اللوحة	التاريخ	المقياس	عنوان اللوحة	المشروع / العميل	مصنع وتد الأخشاب Watad Wood Factory
A-02 (2/10)	2026-09-29	1:50	الواجهة الأمامية (التراس) والواجهة الشرقية	كوخ غرفتين وتراس مسقوف 7.8x7.8 عميل - تصميم حسب الصورة	

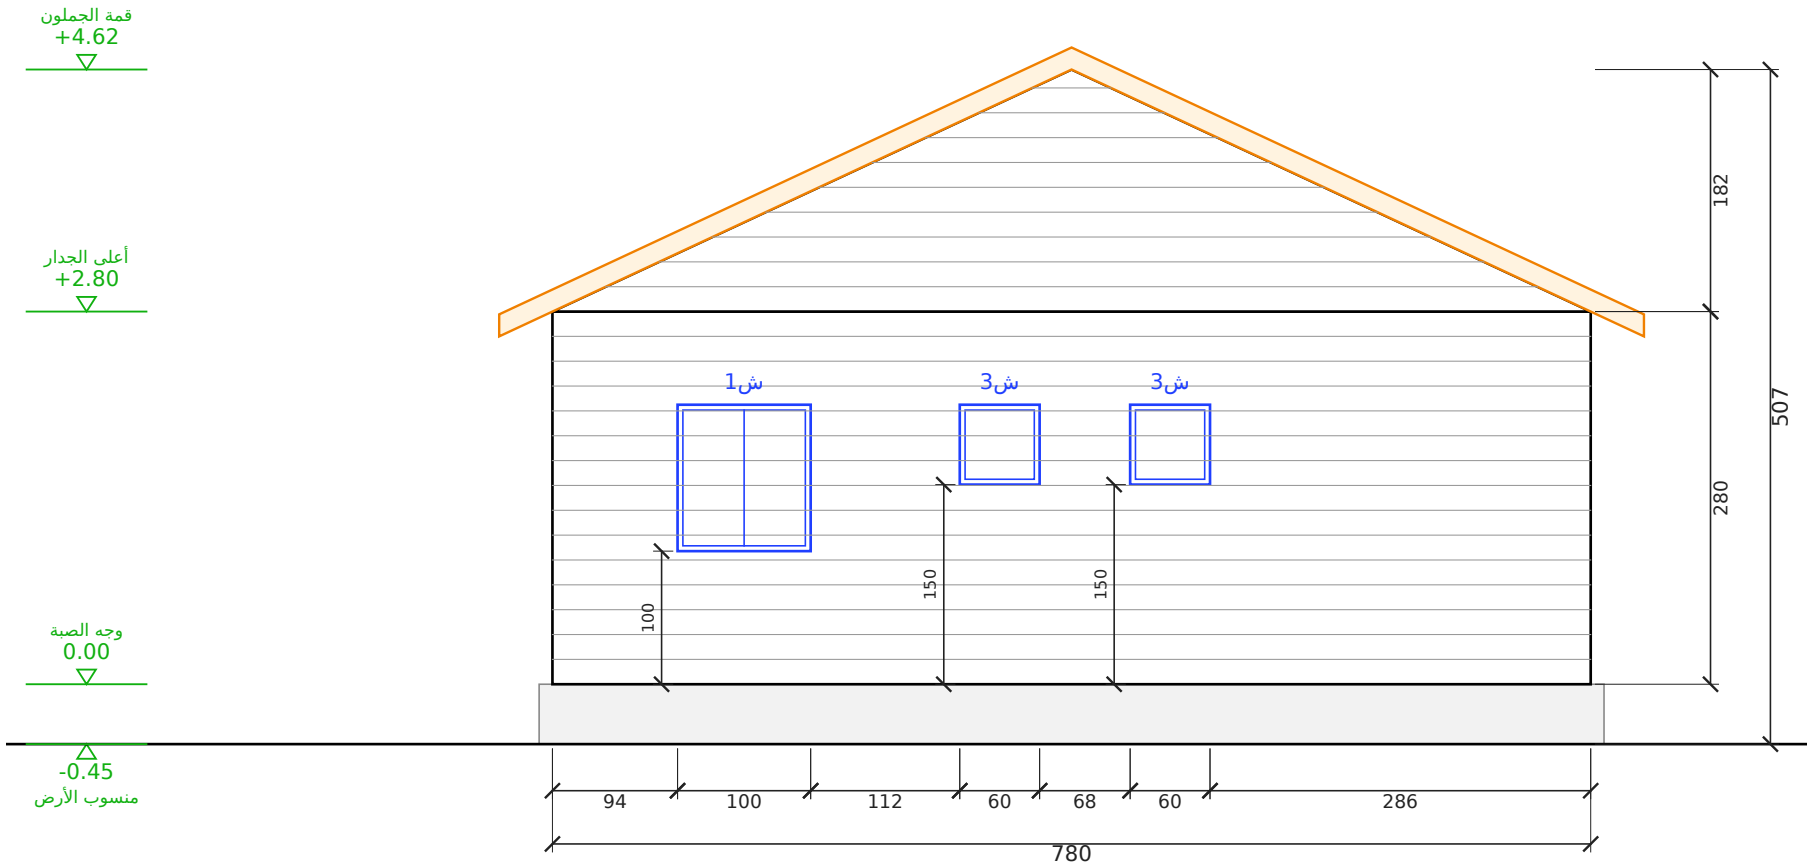

الواجهة الخلفية

مقياس 1:50 | الوحدة: سم

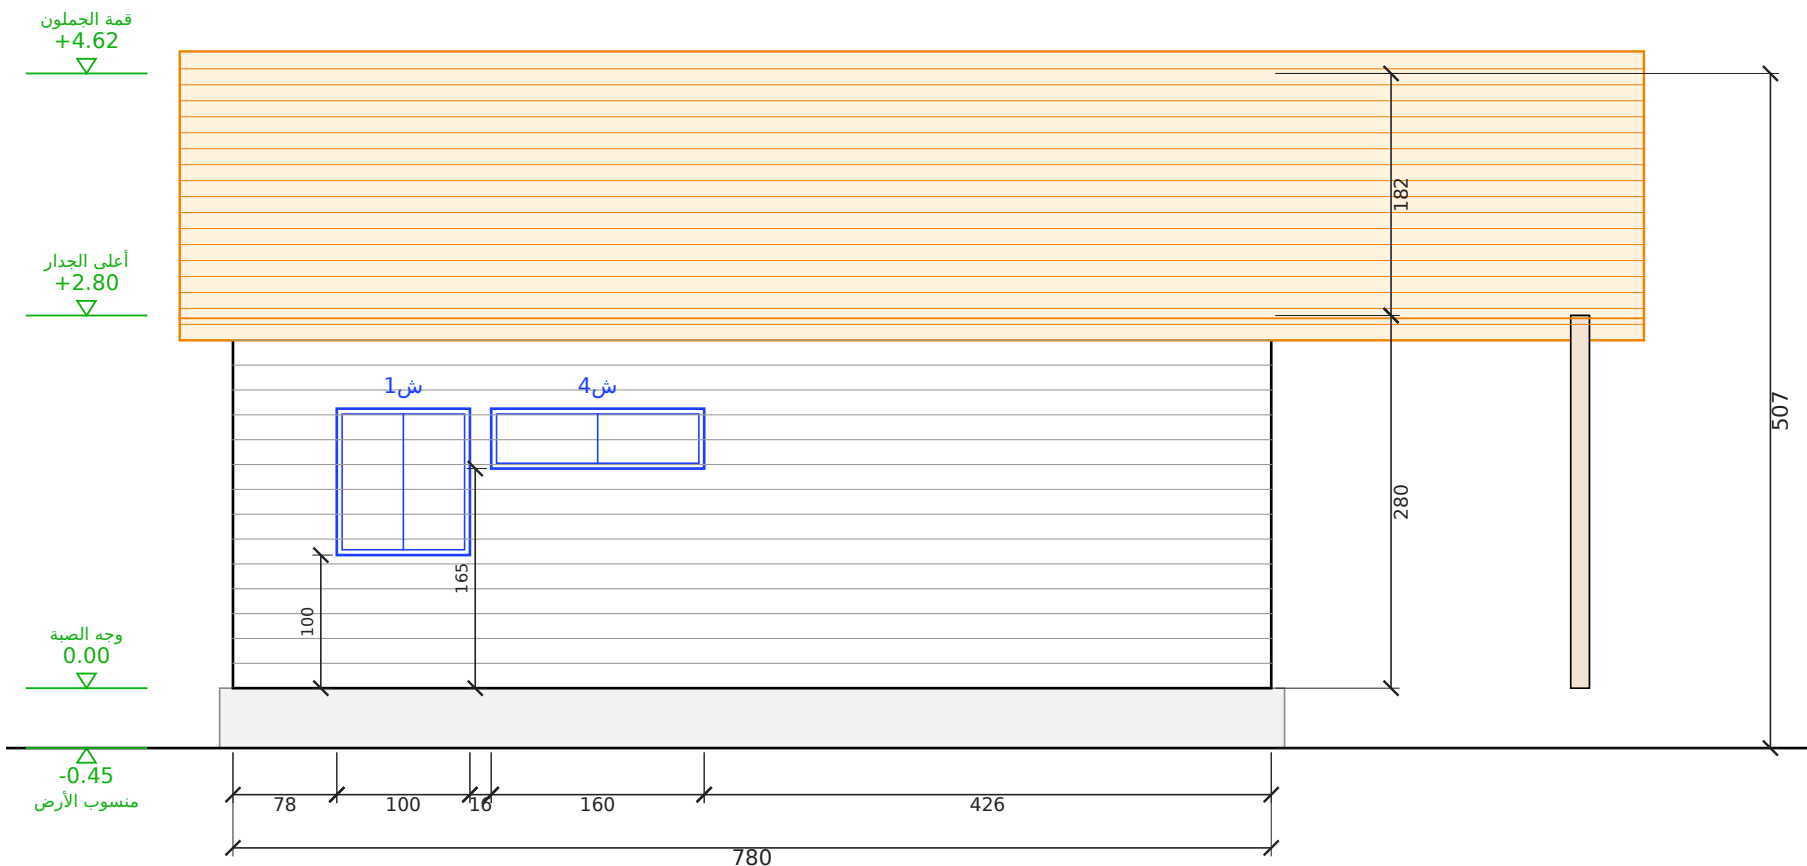


الواجهة الغربية

مقياس 1:50 | الوحدة: سم

رقم اللوحة	التاريخ	المقياس	عنوان اللوحة	المشروع / العميل	مصنع وتد الأخشاب Watad Wood Factory
A-03 (3/10)	2026-09-29	1:50	الواجهة الخلفية والواجهة الغربية	كوخ غرفتين وتراس مسقوف 7.8x7.8 عميل - تصميم حسب الصورة	

مسقط السقف (جملون)
رفر 40 سم من كل جهة | مقياس 1:50

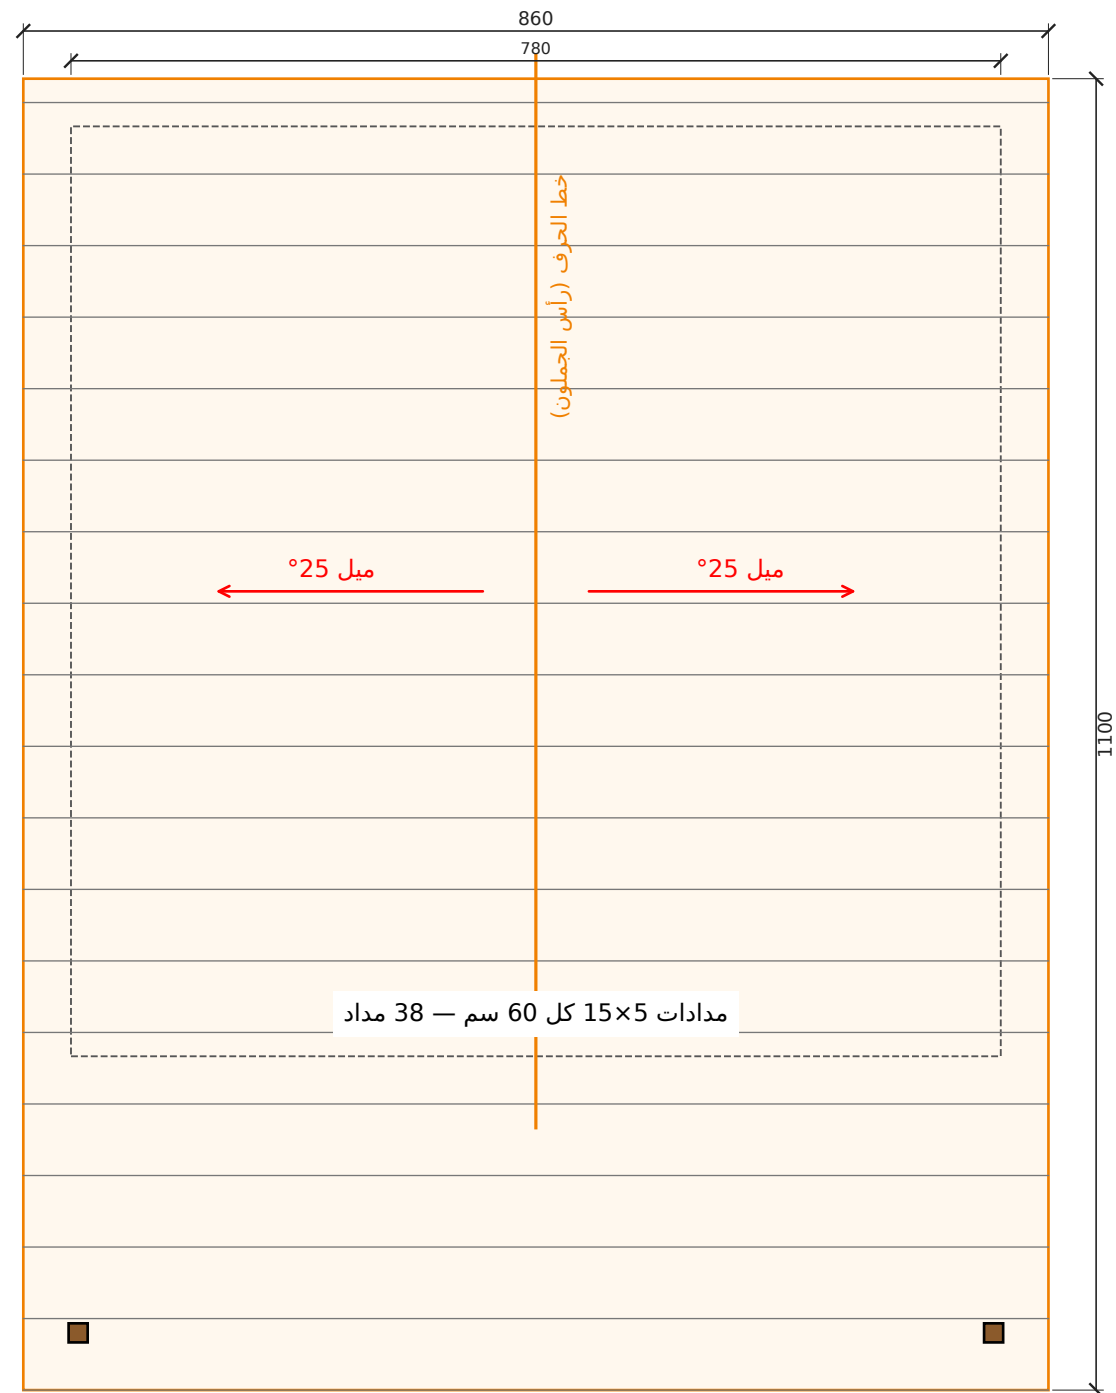


قطاع عرضي أ-أ'
مقياس 1:50 | الوحدة: سم

مداد 15×5 بخلة على العمود العلوي، مثبت ببراعي



تفصيلة جلوس المداد على العلوي (1:5)

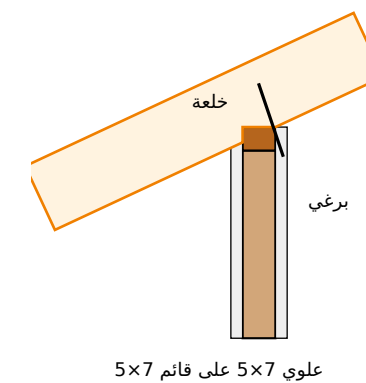

رقم اللوحة	التاريخ	المقياس	عنوان اللوحة	المشروع / العميل	مصنع وتد الأخشاب Watad Wood Factory	
A-04 (4/10)	2026-09-29	1:50	مسطط السقف والقطاع	كوخ غرفتين وتراس مسقوف 7.8×7.8 عميل – تصميم حسب الصورة		

جدول مقاسات الأبواب والشبابيك
مقاس الفتحة الصافي في الجدار - الوحدة: سم

الرمز	النوع	العرض (سم)	الارتفاع (سم)	ارتفاع الجلسة (سم)	العدد	الموقع
ب1	باب	300	265	-	1	الأمامية (التراس)
ب2	باب	80	210	-	2	ماستر - غرفة 2
ب3	باب	70	210	-	2	حمام مشترك - حمام ماستر
ف1	باب	90	210	-	1	فتحة الممر
ز1	شباك	140	210	30	2	الأمامية (التراس) 2
ش1	شباك	100	110	100	3	الشرقية - الخلفية - الغربية
ش2	شباك	100	100	110	1	الشرقية
ش3	شباك	60	60	150	2	الخلفية 2
ش4	شباك	160	45	165	1	الغربية

الإجمالي: أبواب 6 - شبابيك 9

جدول المساحات وبيانات المشروع والتسعير

جدول المساحات

م	الفراغ	الأبعاد (م)	المساحة (م2)
1	الصالة ومطبخ الخدمة	7.56 × 3.30	24.95
2	غرفة الماستر	3.60 × 4.14	11.79
3	حمام الماستر	1.50 × 1.80	2.70
4	ممر	1.20 × 1.92	2.30
5	حمام مشترك	1.20 × 2.10	2.52
6	غرفة 2	2.52 × 4.14	10.43
	المساحة الصافية الداخلية		54.70
	التراس المسقوف	7.80 × 2.40	18.72
	المساحة الإجمالية المبنية	7.80 × 7.80	60.84

بيانات المشروع

البند	البيان
المشروع	كوخ غرفتين وتراس مسقوف 7.8×7.8
العميل	عميل — تصميم حسب الصورة
الموقع	—
الاستخدام	استراحة / استجمام
التاريخ	2026-09-29
نظام البناء	هيكل خشب 5×7 + تليس 2.5 سم من الجهتين
السقف	جملون 25° — قرميد معدني

التسعير

عرض اليوم الوطني


البند	القيمة
المساحة المبنية (م2)	60.84
سعر المتر المربع — عرض اليوم الوطني	1,096 ريال
الإجمالي	66,681 ريال

ملاحظات:

- السعر للمساحة المبنية حسب المخطط المعتمد.
- الصبة والتوريدات الخارجية على العميل ما لم يُذكر غير ذلك.

الصور الواقعية


أمامي

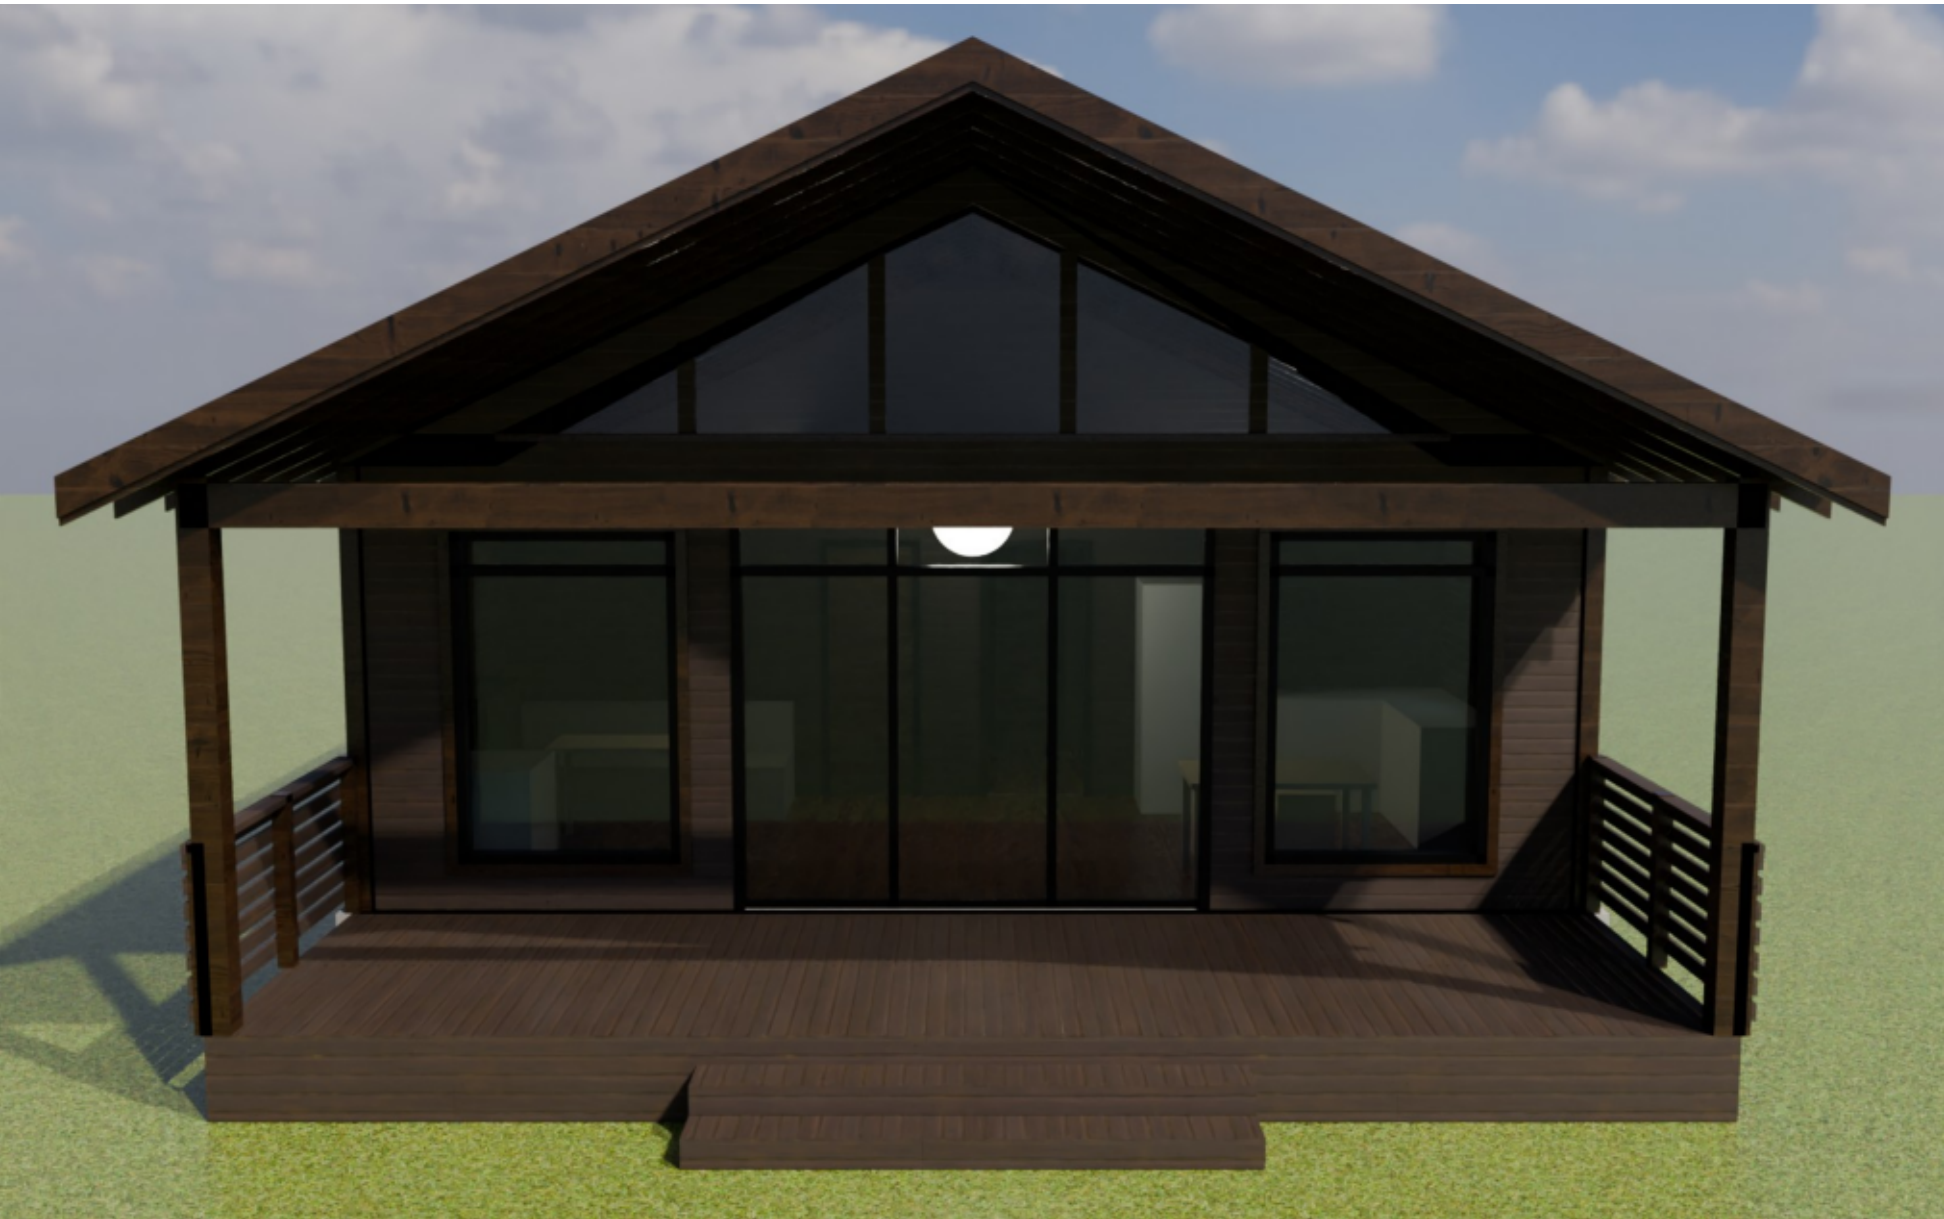

أمامي يسار



أمامي يمين

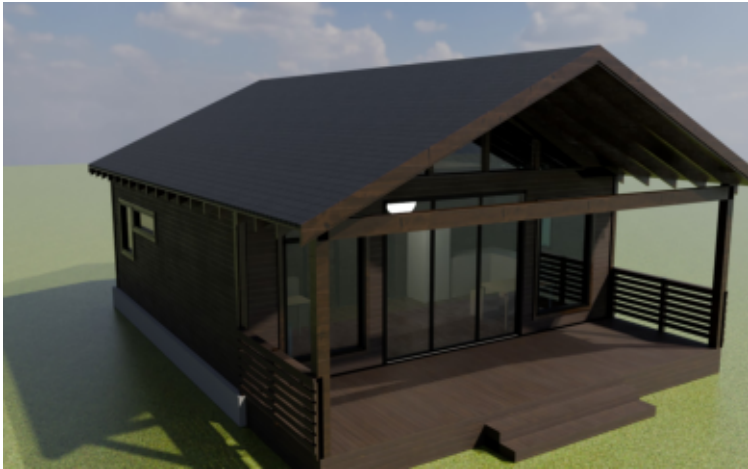

خلفي



رندر واقعي بخامات حقيقية وإضاءة طبيعية — الألوان النهائية حسب عينات المورد

المشروع / العميل	عنوان اللوحة	المقياس	التاريخ	رقم اللوحة	مصنع وتد الأخشاب Watad Wood Factory
كوخ غرفتين وتراس مسقوف 7.8×7.8 عميل — تصميم حسب الصورة	الصور الواقعية	—	2026-09-29	A-07 (7/10)	

لقطات المنظور الخارجي


المنظور الأمامي




منظور أمامي من اليسار




منظور أمامي من اليمين

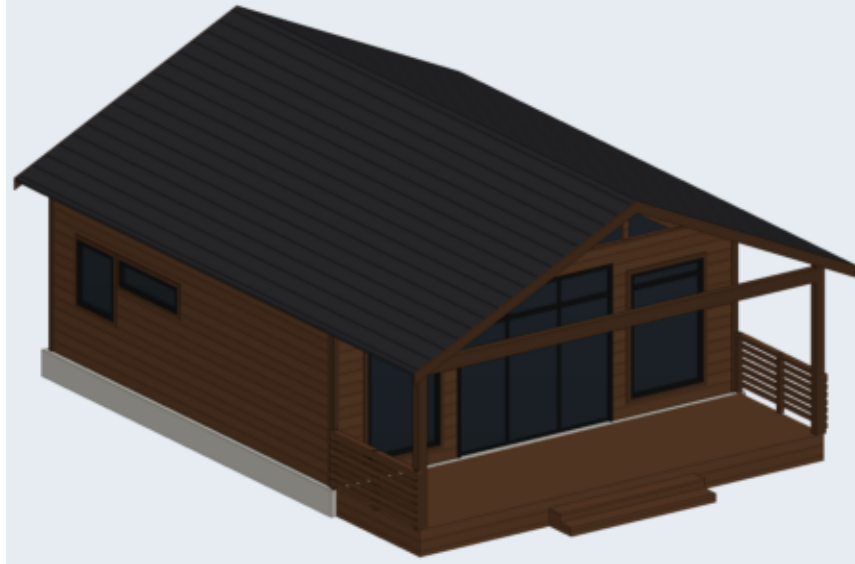


المنظور الخلفي

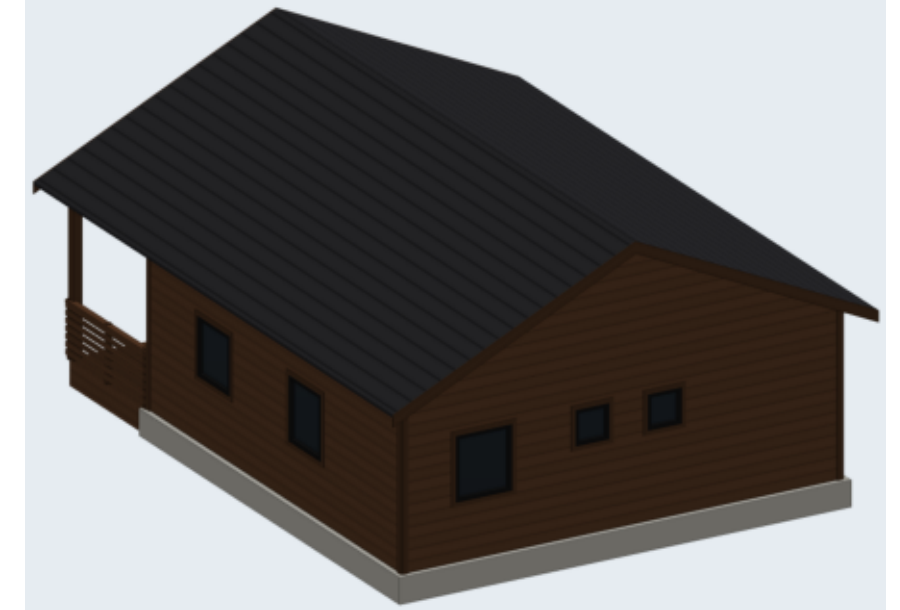

منظور خلفي من اليمين

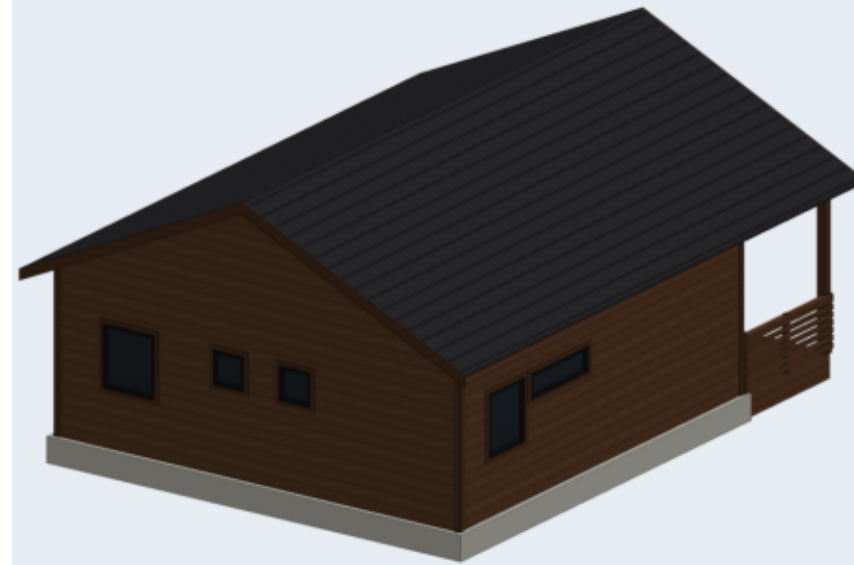

منظر علوي

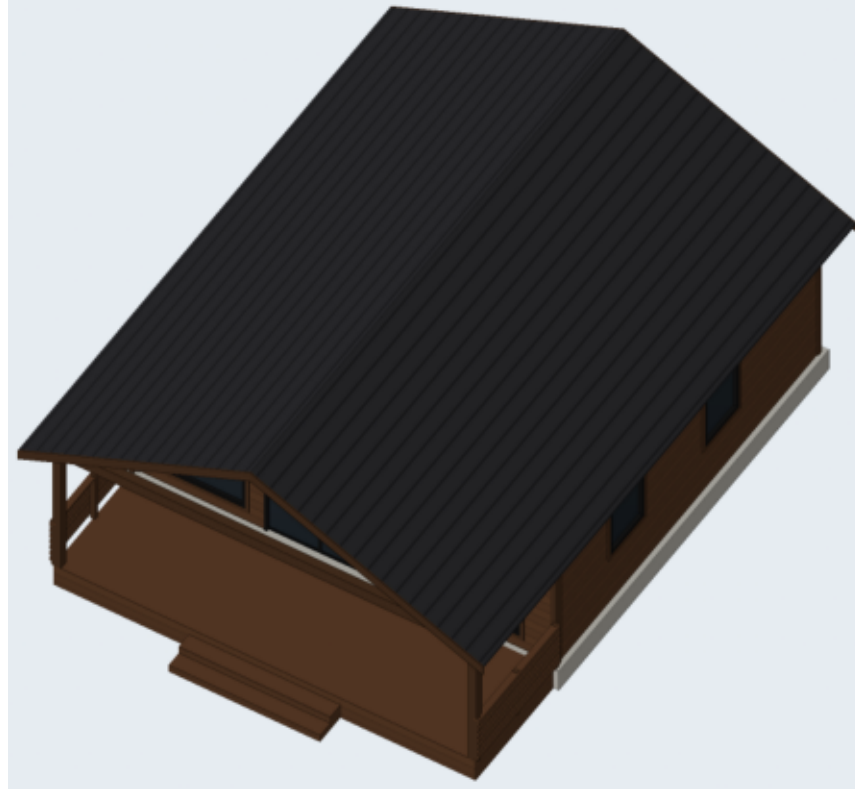

رقم اللوحة

A-08 (8/10)

التاريخ

2026-09-29

المقياس

—

عنوان اللوحة

لقطات المنظور

المشروع / العميل

كوخ غرفتين وتراس مسقوف 7.8×7.8
عميل — تصميم حسب الصورة

مصنع وتد الأخشاب
Watad Wood Factory



المقطع العلوي بالفرش

مقطع أفقي على ارتفاع 1.90 م — توزيع الفرش ومسار الحركة



رقم اللوحة

A-09 (9/10)

التاريخ

2026-09-29

المقياس

—

عنوان اللوحة

المقطع العلوي بالفرش

المشروع / العميل

كوخ غرفتين وتراس مسقوف 7.8×7.8
عميل — تصميم حسب الصورة

مصنع وتد الأخشاب
Watad Wood Factory



المنظور ثلاثي الأبعاد والمواد

النمط: جوزي غامق + إطارات سوداء — معاينة تقريبية، الإخراج النهائي من 3ds Max

جدول المواد والألوان

الخشب / الصبغة

صبغة جوزي غامق

القرميد

قرميد رمادي غامق

الزجاج

زجاج عاكس غامق

إطارات الشبابيك والأبواب

إطار ألومنيوم أسود

الكنار والزوايا

نفس الصبغة أعمق درجة

الصبة

خرسانة 45 سم

الدريزين: ألواح أفقية متقاربة (عصري)


تقسيم الشبابيك: بدون | الباب الرئيسي: سحب زجاج




أنواع الدريزين المعتمدة (من مشاريع المصنع)



قوائم رأسية متقاربة (صورة 1)

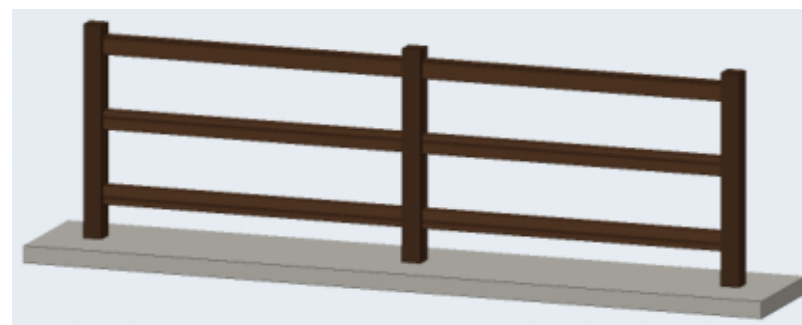

3 مربيع أفقية (صورة 2)

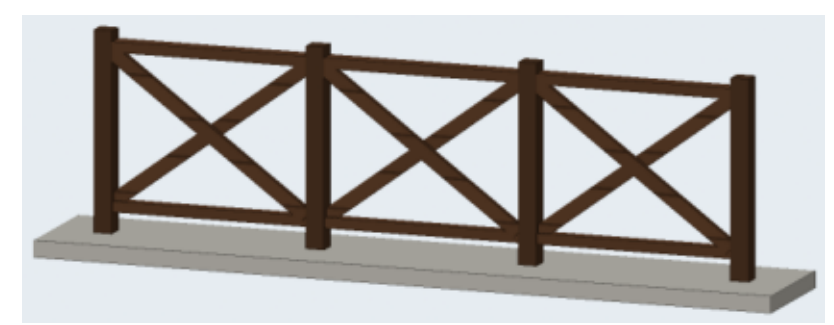

تقاطع X (صورة 5)

رقم اللوحة

A-10 (10/10)

التاريخ

2026-09-29

المقياس

—

عنوان اللوحة

المنظور والمواد

المشروع / العميل

كوخ غرفتين وتراس مسقوف 7.8×7.8
عميل — تصميم حسب الصورة

مصنع وتد الأخشاب
Watad Wood Factory

