

المسقط الأفقي مع الفرش

الأبعاد بالسنتيمتر - الجدران: قوائم 7×5 + تلبيس 2.5 من الجهتين (12 سم)

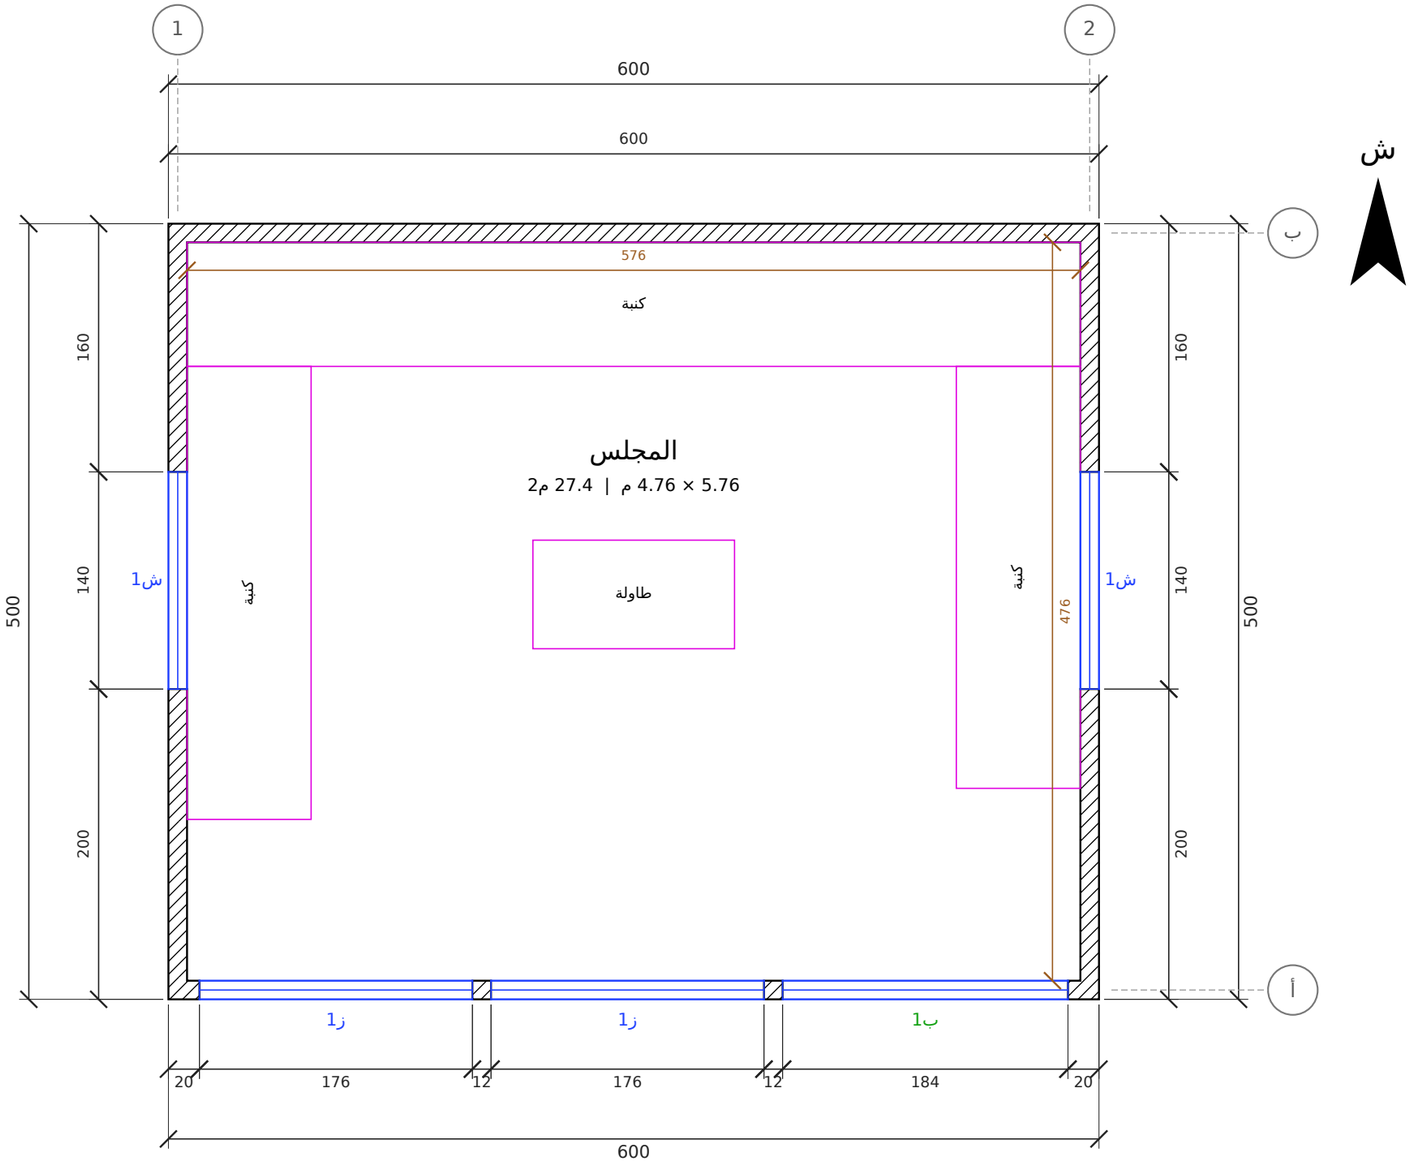


المشروع / العميل	عنوان اللوحة	المقياس	التاريخ	رقم اللوحة
مجلس حديث بواجهة زجاج كاملة — 6.00 × 5.00 = 30 م² **عميل — مجلس حديث 5×6**	**المسقط الأفقي**	**1:50**	**2026-10-23**	**A-01 (1/9)**

مصنع وتد الأخشاب
Watad Wood Factory

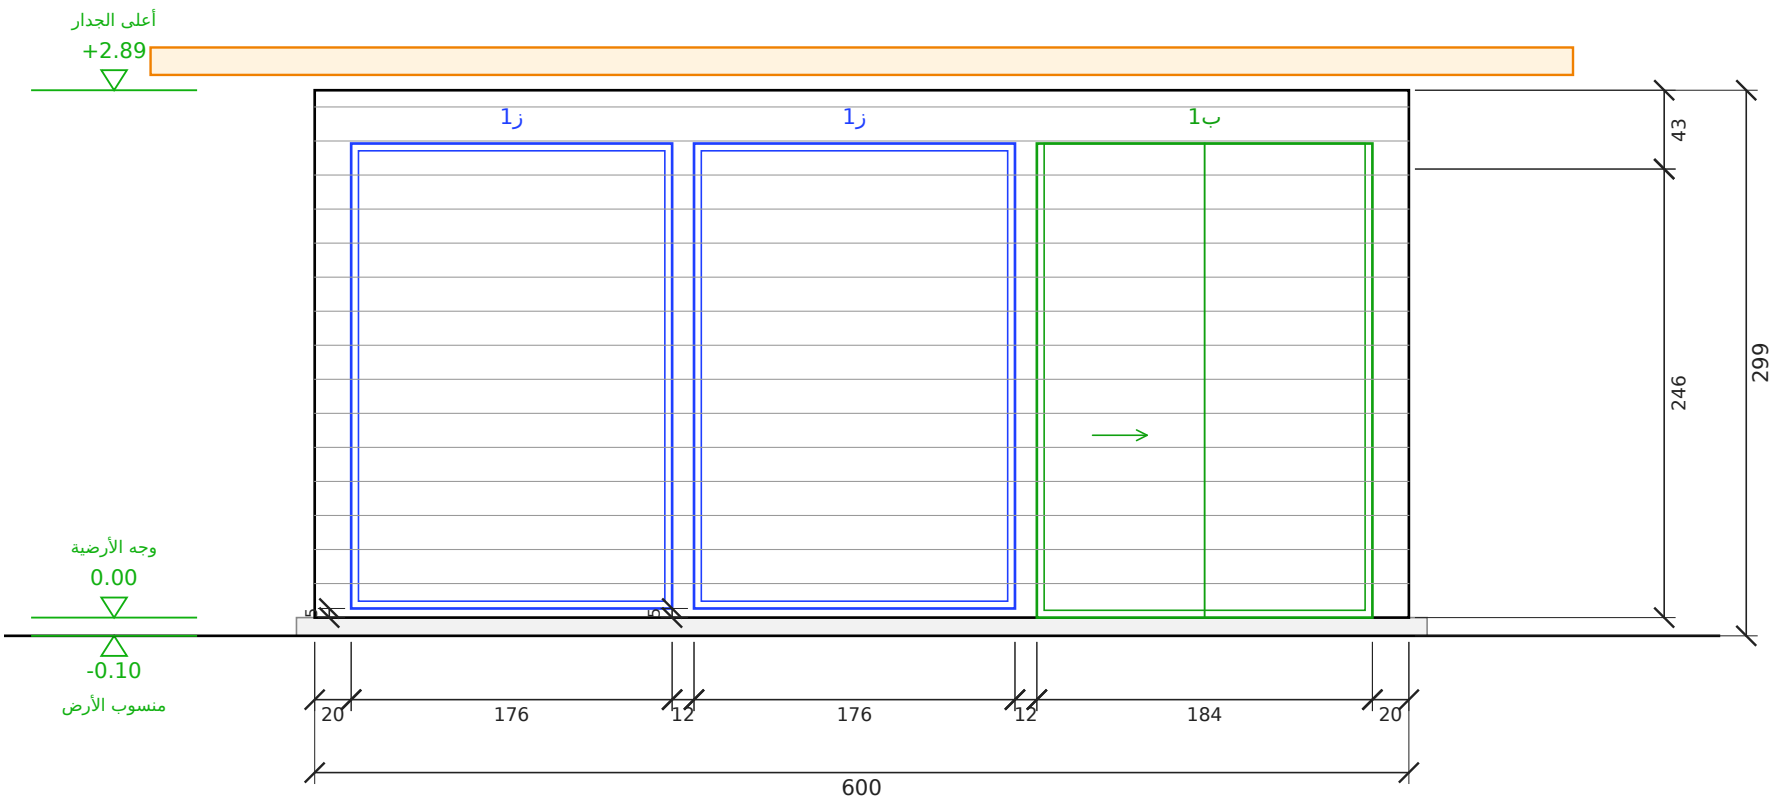

الواجهة الأمامية (زجاج كامل)

مقياس 1:50 | الوحدة: سم

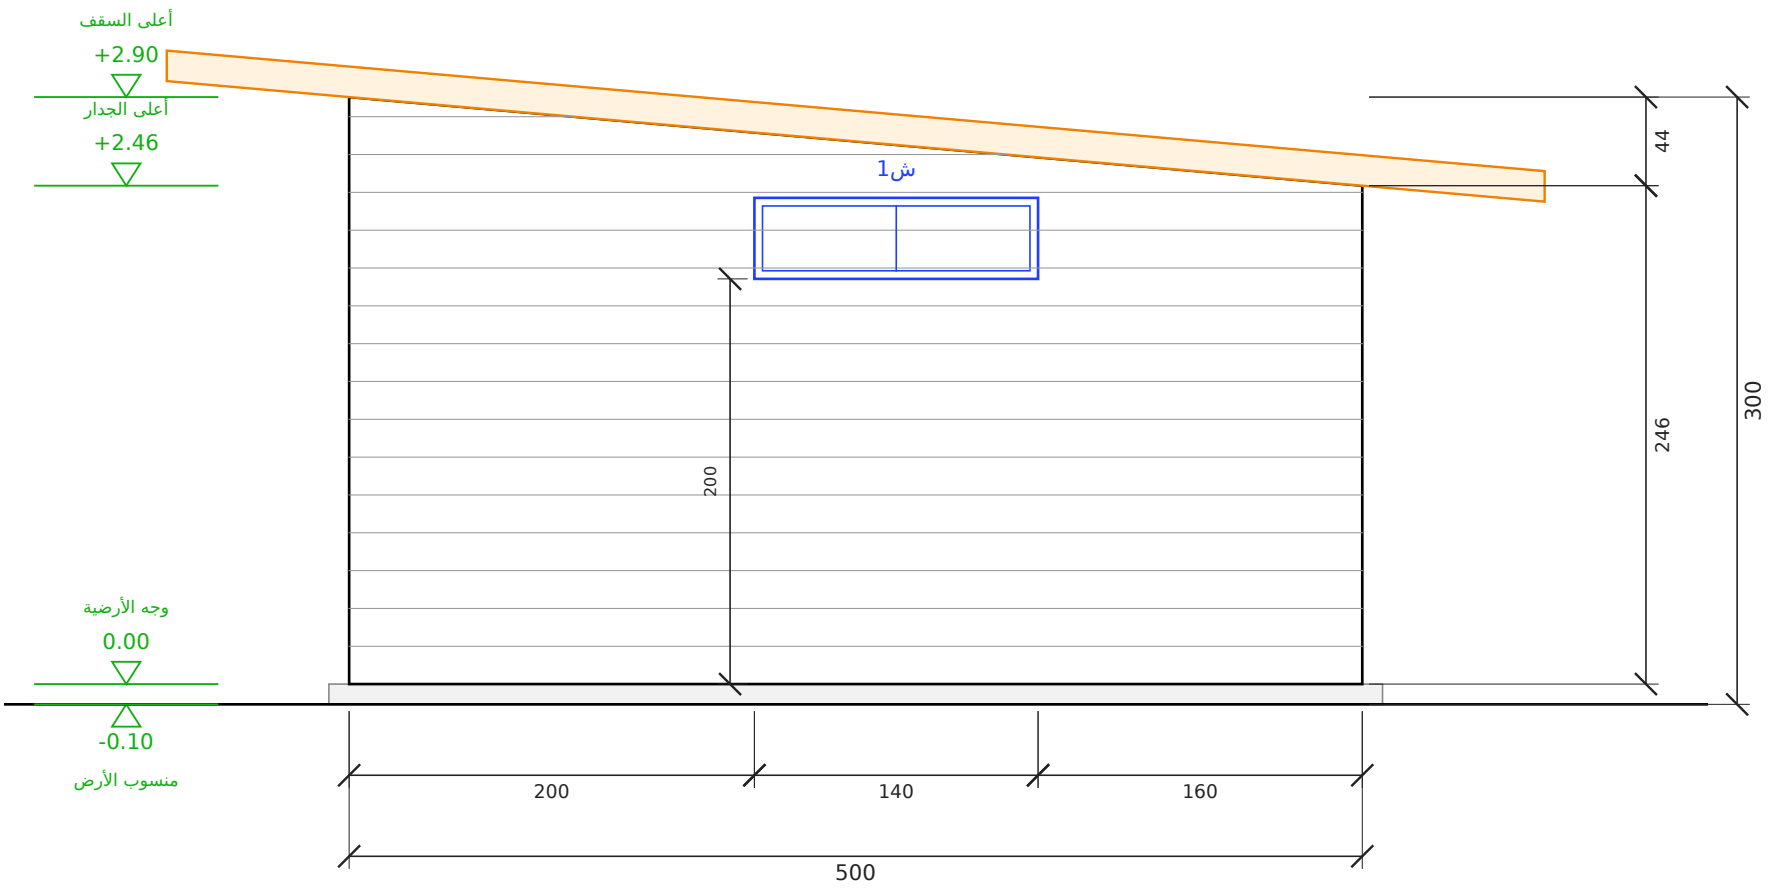


الواجهة الشرقية

مقياس 1:50 | الوحدة: سم


المشروع / العميل	عنوان اللوحة	المقياس	التاريخ	رقم اللوحة
مجلس حديث بواجهة زجاج كاملة — 6.00 × 5.00 = 30 م² **عميل — مجلس حديث 5×6**	**الواجهة الأمامية (زجاج كامل) والواجهة الشرقية**	**1:50**	**2026-10-23**	**A-02 (2/9)**

مصنع وتد الأخشاب
Watad Wood Factory

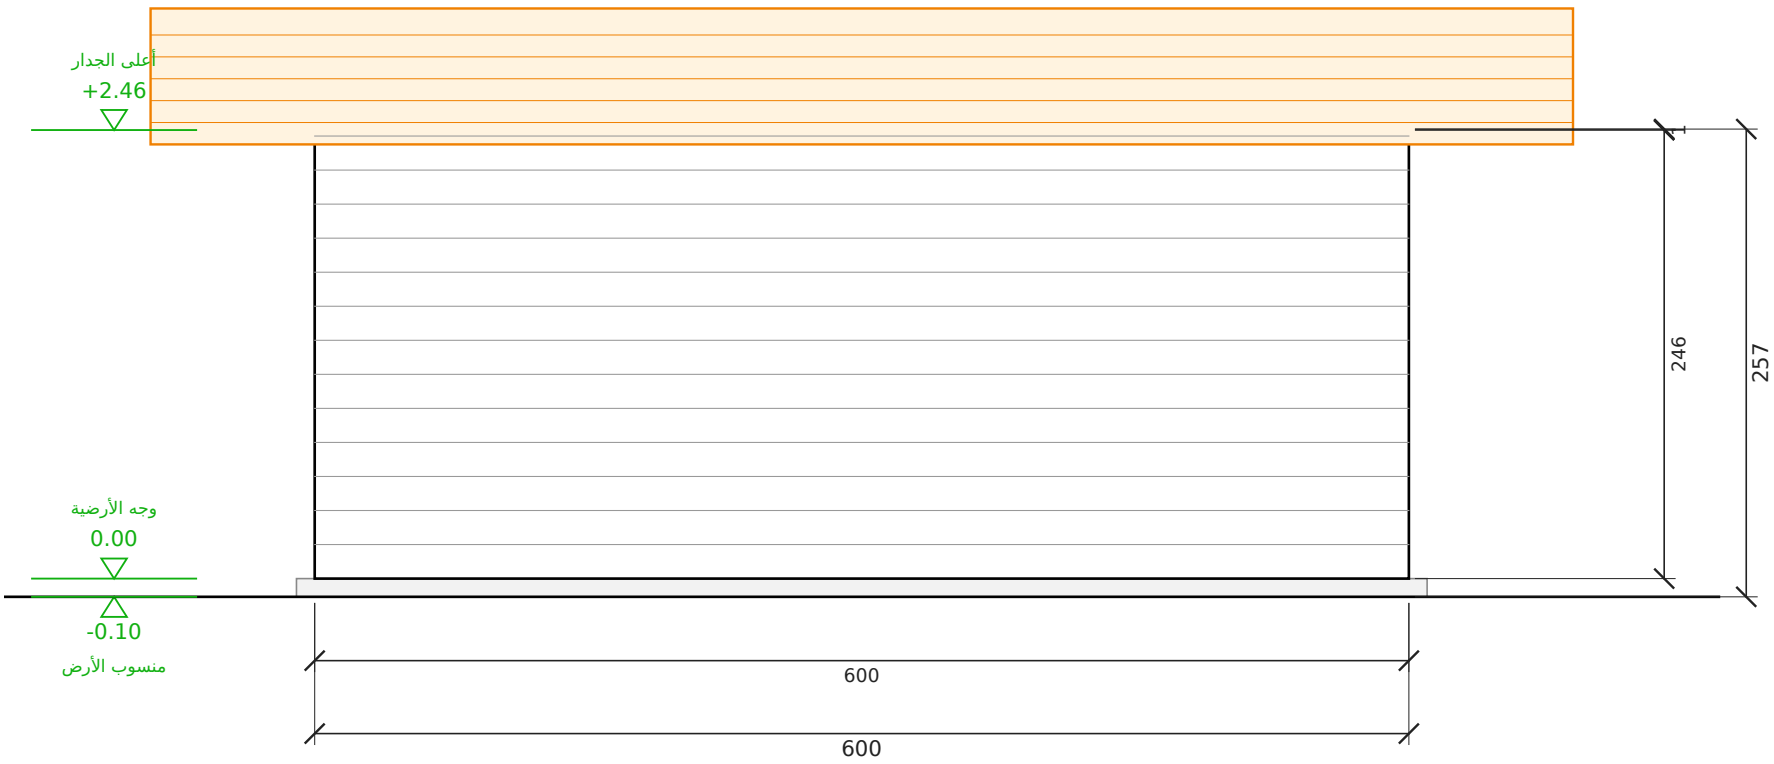

الواجهة الخلفية

مقياس 1:50 | الوحدة: سم

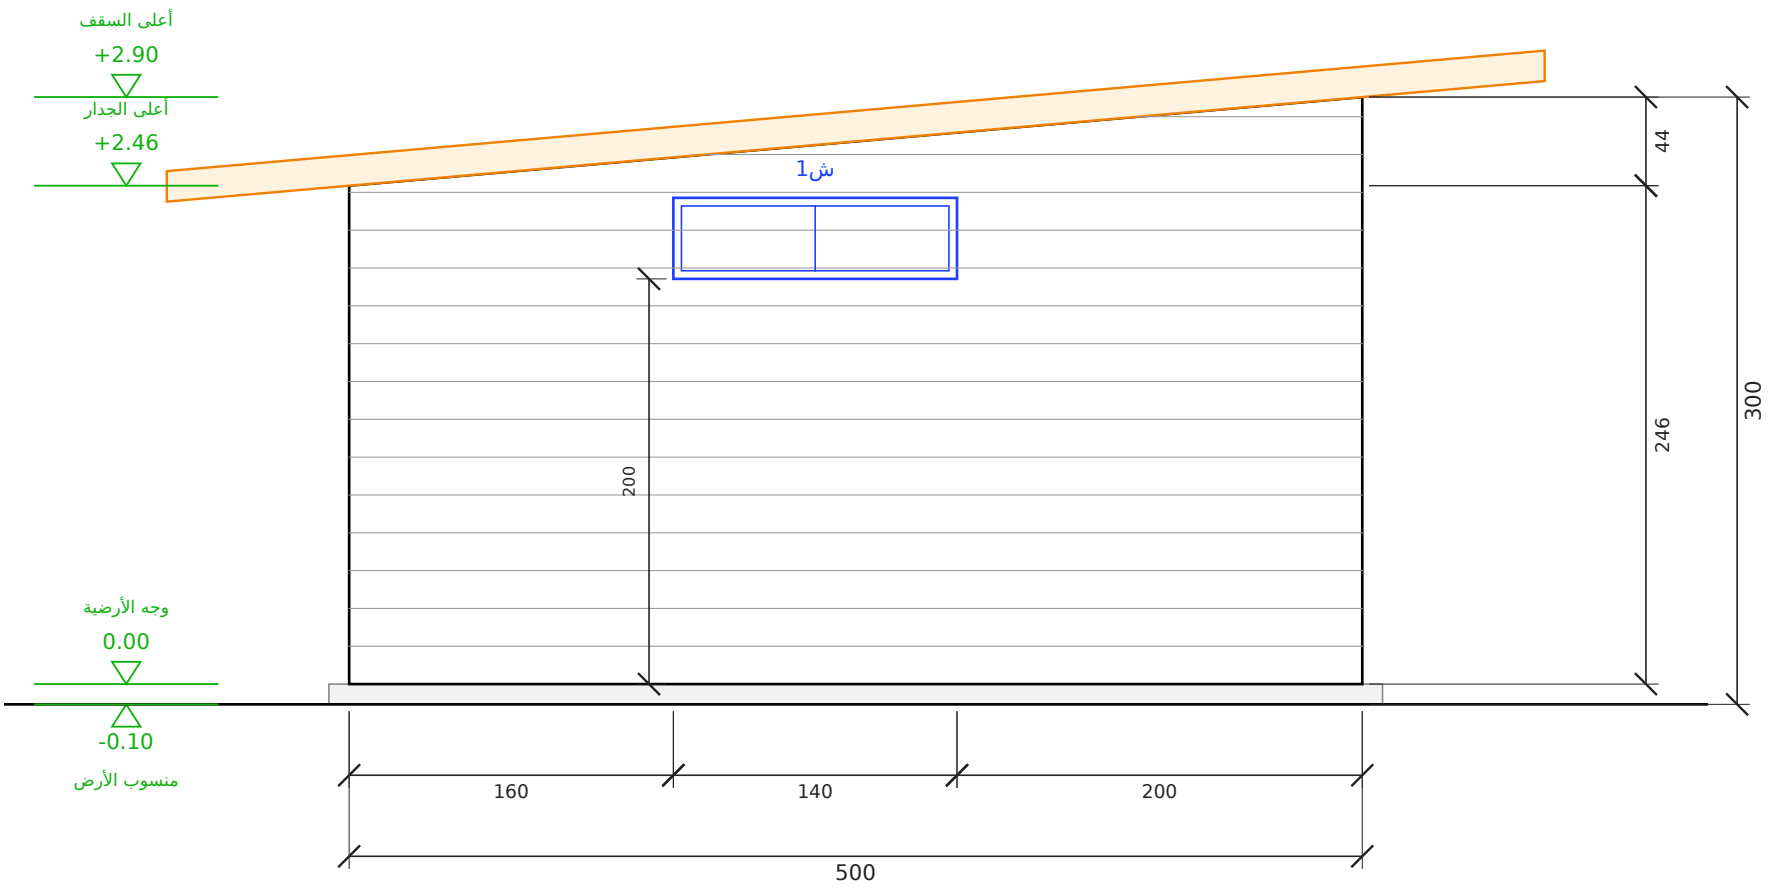


الواجهة الغربية

مقياس 1:50 | الوحدة: سم


المشروع / العميل	عنوان اللوحة	المقياس	التاريخ	رقم اللوحة
مجلس حديث بواجهة زجاج كاملة — 6.00 × 5.00 = 30 م² عميل — مجلس حديث 5×6	الواجهة الخلفية والواجهة الغربية	1:50	2026-10-23	A-03 (3/9)

مصنع وتد الأخشاب
Watad Wood Factory


مسقط السقف (مائل باتجاه واحد)
رفرف 90 سم من كل جهة | مقياس 1:50

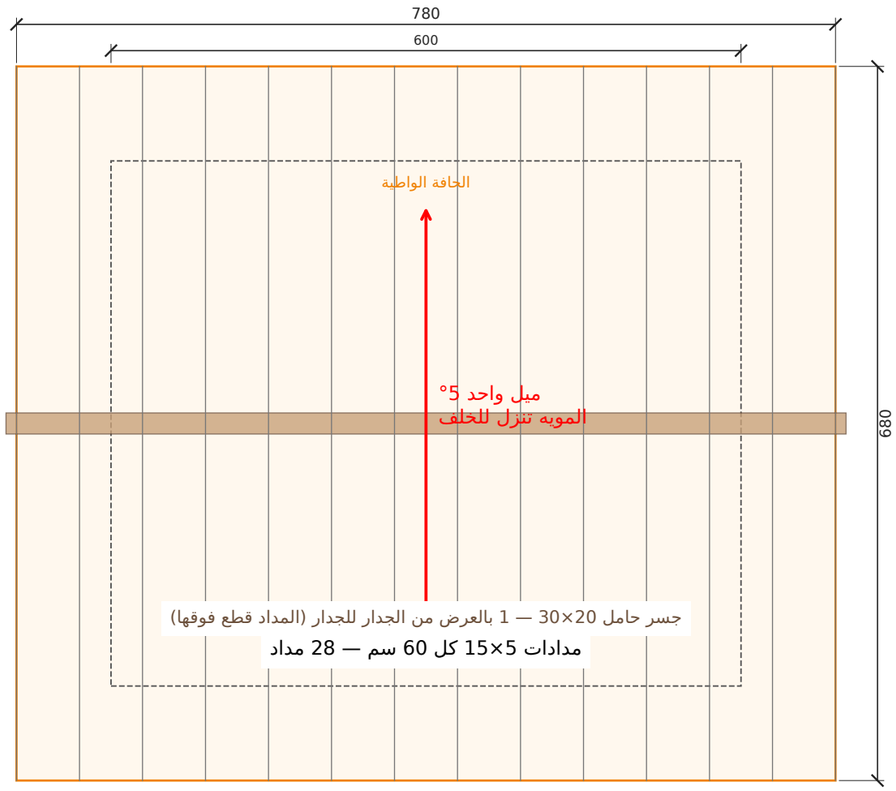

قطاع عرضي أ-أ
مقياس 1:50 | الوحدة: سم

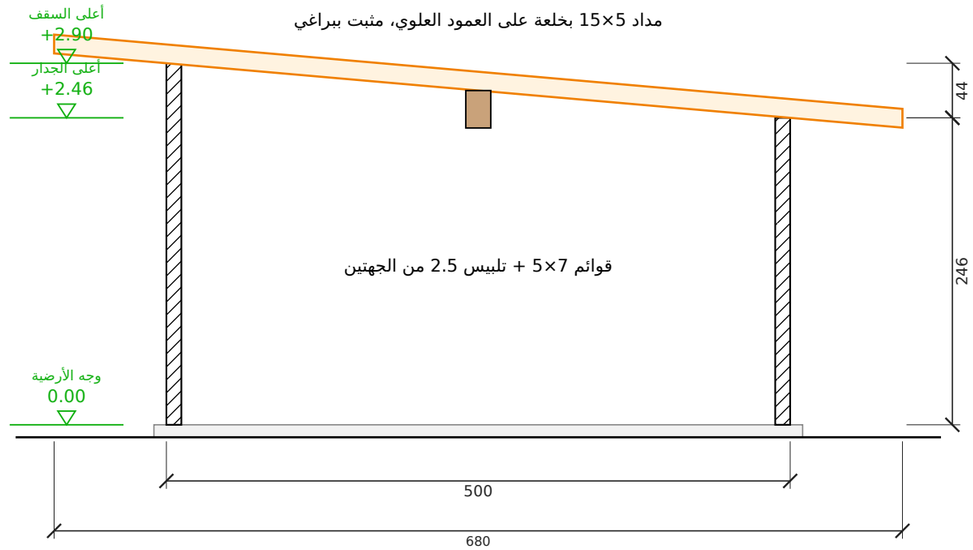

تفصيلة جلوس المداد على العلوي (1:5)

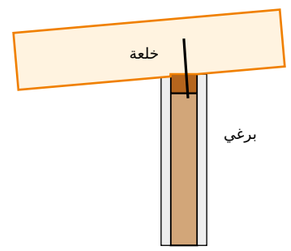

المشروع / العميل	عنوان اللوحة	المقياس	التاريخ	رقم اللوحة
مجلس حديث بواجهة زجاج كاملة — 6.00 × 5.00 = 30 م² **عميل — مجلس حديث 5×6**	**مسقط السقف والقطاع**	**1:50**	**2026-10-23**	**A-04 (4/9)**

مصنع وتد الأخشاب
Watad Wood Factory

جدول مقاسات الأبواب والشبابيك
مقاس الفتحة الصافي في الجدار - الوحدة: سم

الرمز	النوع	العرض (سم)	الارتفاع (سم)	ارتفاع الجلسة (سم)	العدد	الموقع
ب1	باب مزدوج	184	260	-	1	الأمامية (زجاج كامل)
ز1	شباك	176	255	5	2	الأمامية (زجاج كامل) 2
ش1	شباك	140	40	200	2	الشرقية - الغربية

الإجمالي: أبواب 1 - شبابيك 4

جدول المساحات وبيانات المشروع

بيانات المشروع


البند	البيان
المشروع	مجلس حديث بواجهة زجاج كاملة — 6.00 × 5.00 = 30 م²
العميل	عميل — مجلس حديث 5×6
الموقع	—
الاستخدام	مجلس
التاريخ	2026-10-23
نظام البناء	هيكل خشب 5×7 + تلبيس 2.5 سم من الجهتين
السقف	مائل باتجاه واحد 5° — صاج معدني + عزل مائي

جدول المساحات


م	الفراغ	الأبعاد (م)	المساحة (م2)
1	المجلس	5.76 × 4.76	27.42
	المساحة الصافية الداخلية		**27.42**
	المساحة الإجمالية المبنية	**6.00 × 5.00**	**30.00**

لقطات المنظور الخارجي


المنظور الأمامي

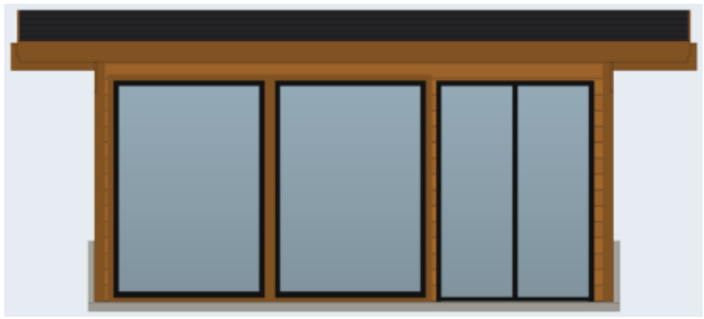


منظور أمامي من اليسار

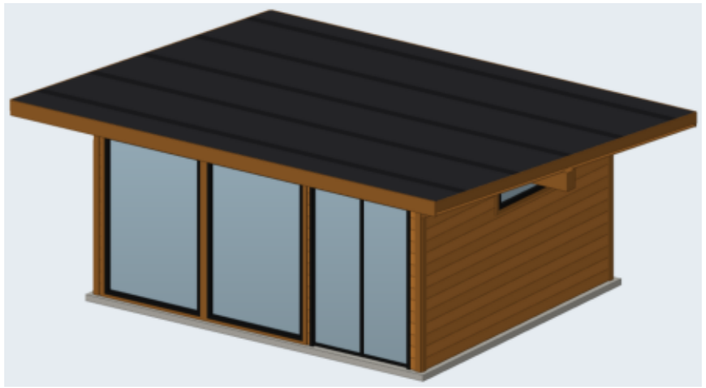


منظور أمامي من اليمين

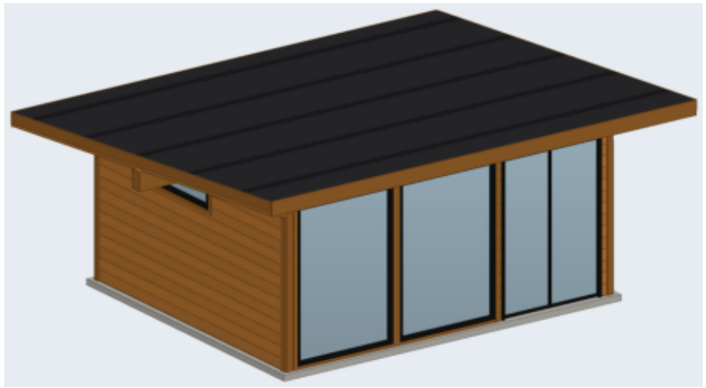

المنظور الخلفي

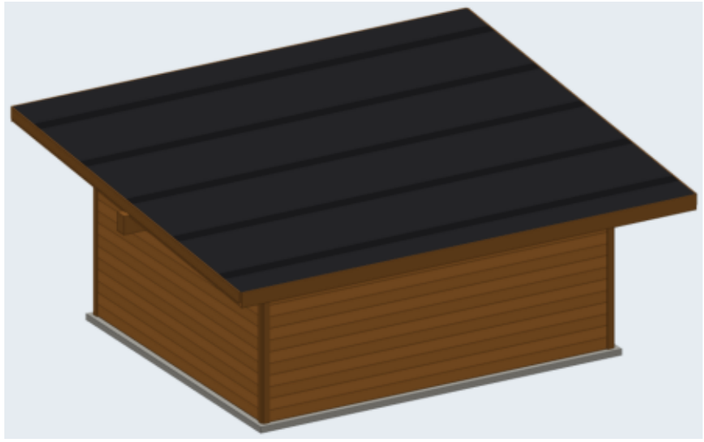

منظور خلفي من اليمين

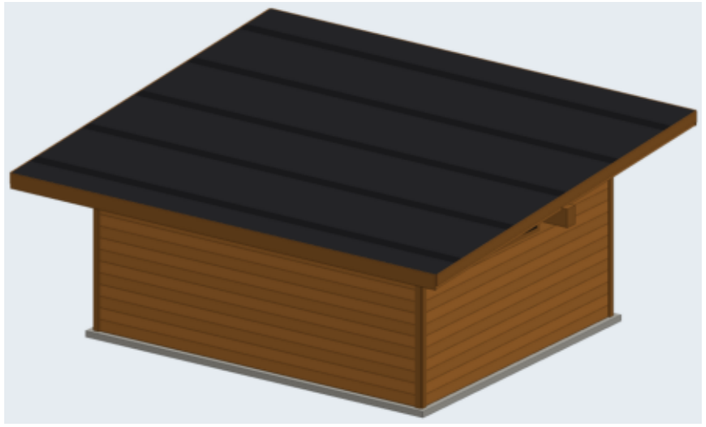

منظر علوي




المشروع / العميل	عنوان اللوحة	المقياس	التاريخ	رقم اللوحة
مجلس حديث بواجهة زجاج كاملة — 6.00 × 5.00 = 30 م² **عميل — مجلس حديث 5×6**	**لقطات المنظور**	**—**	**2026-10-23**	**A-07 (7/9)**

مصنع وتد الأخشاب
Watad Wood Factory

المقطع العلوي بالفرش

مقطع أفقي على ارتفاع 1.90 م — توزيع الفرش ومسار الحركة

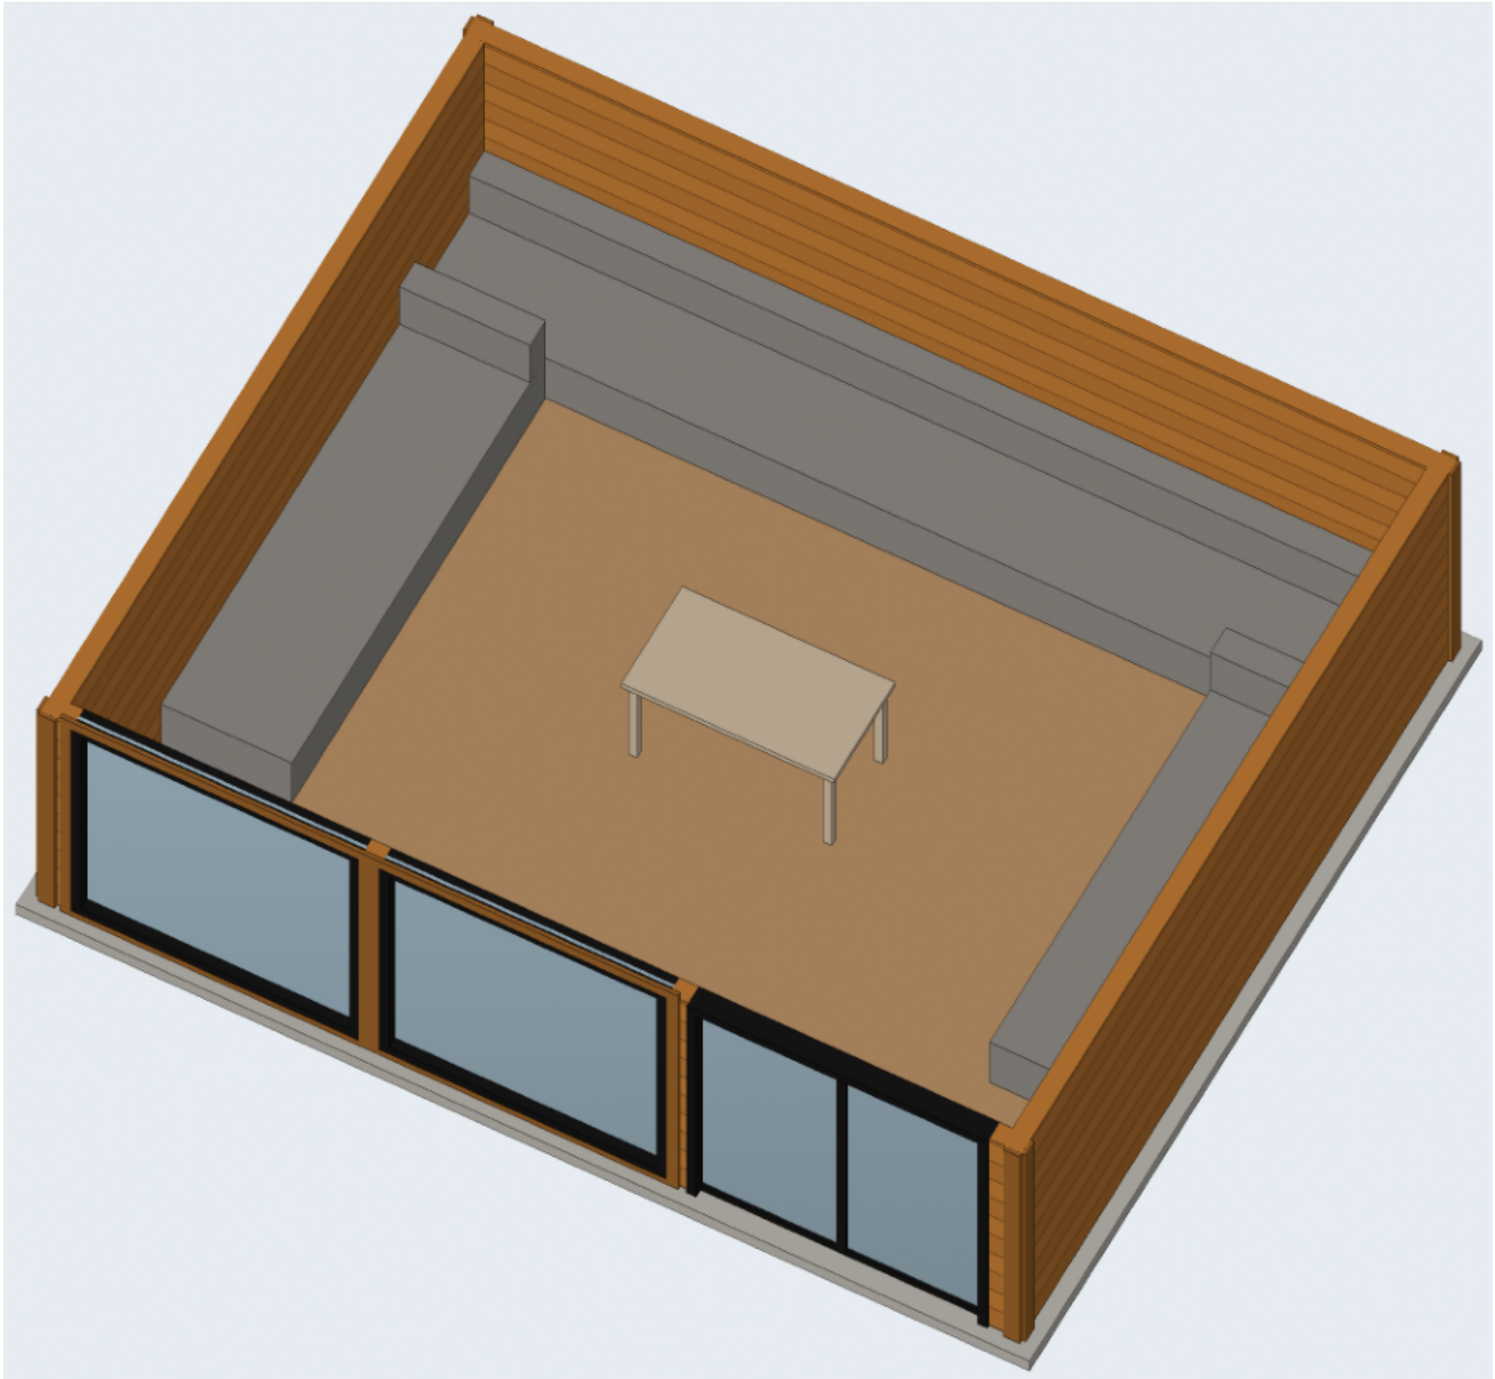


المشروع / العميل	عنوان اللوحة	المقياس	التاريخ	رقم اللوحة
مجلس حديث بواجهة زجاج كاملة — 6.00 × 5.00 = 30 م² **عميل — مجلس حديث 5×6**	**المقطع العلوي بالفرش**	**—**	**2026-10-23**	**A-08 (8/9)**

مصنع وتد الأخشاب
Watad Wood Factory

المنظور ثلاثي الأبعاد والمواد

النمط: جوزي غامق + إطارات سوداء — رندر واقعي بخامات حقيقية

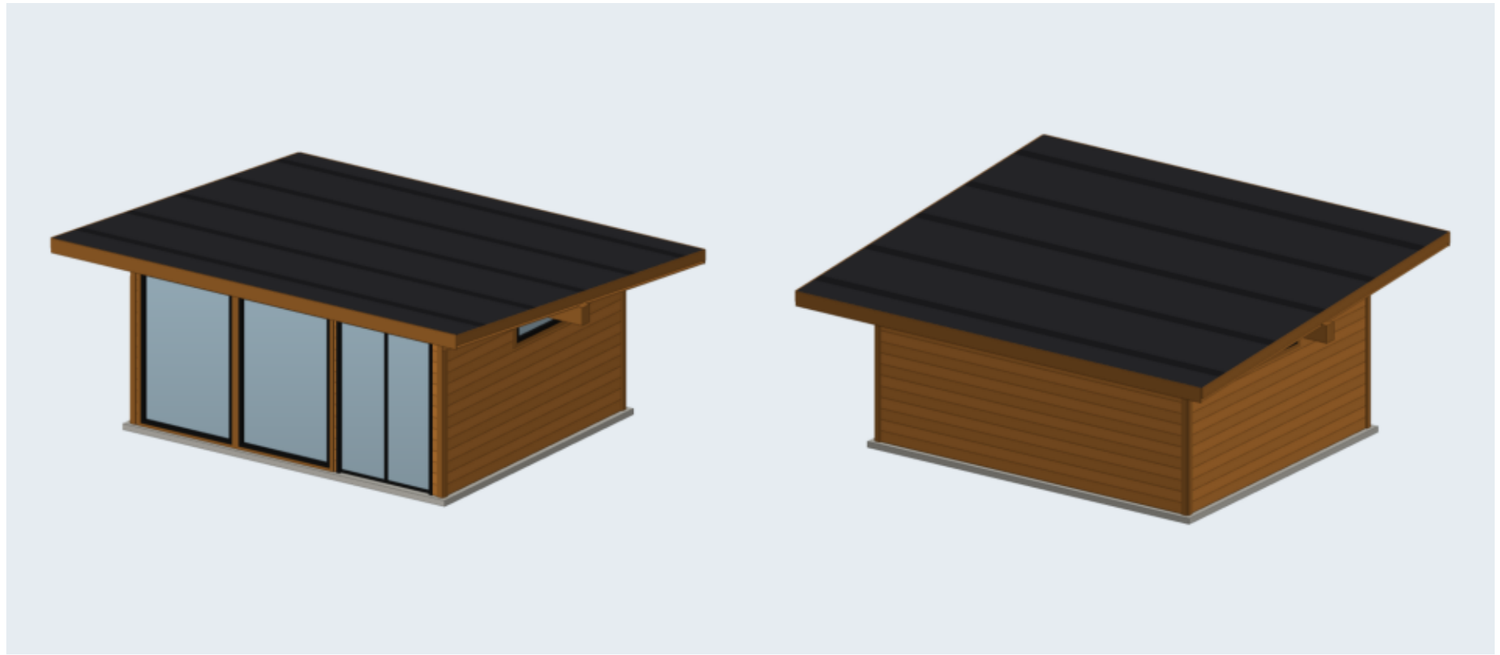

جدول المواد والألوان

الخشب / الصبغة

صبغة عسلي / سيدر

السقف (صاج معدني)

صاج رمادي غامق

الزجاج

زجاج شفاف

إطارات الشبابيك والأبواب

إطار ألمنيوم أسود

الكنار والزوايا

نفس الصبغة أغمق درجة


القاعدة

قواعد حديد 10 سم (متنقل — بدون صبة)


الدربزين: قوائم رأسية متقاربة (صورة 1)

تقسيم الشبابيك: بدون | الباب الرئيسي: سحاب زجاج

أنواع الدربزين المعتمدة (من مشاريع المصنع)

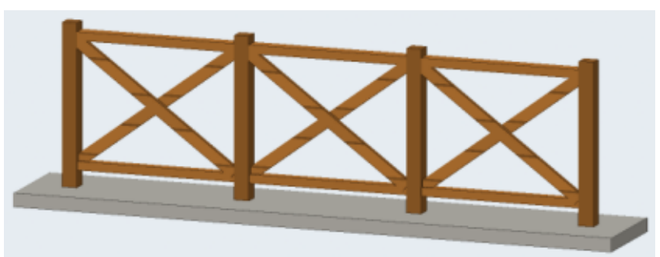

تقاطع X (صورة 5)

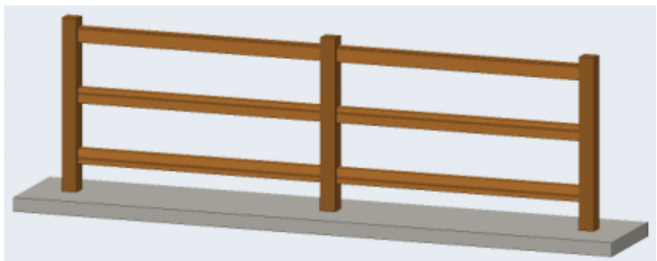

3 مرابيع أفقية (صورة 2)



قوائم رأسية متقاربة (صورة 1)

المشروع / العميل	عنوان اللوحة	المقياس	التاريخ	رقم اللوحة
مجلس حديث بواجهة زجاج كاملة — 6.00 × 5.00 = 30 م² **عميل — مجلس حديث 5×6**	**المنظور والمواد**	**—**	**2026-10-23**	**A-09 (9/9)**

مصنع وتد الأخشاب
Watad Wood Factory

الرندر الواقعي — الخارج نهاراً · الواجهة الزجاج — منظور أمامي



(مصنع وتد الأخشاب — الواقع الافتراضي في آخر صفحة (أو اضغط هنا

الرندر الواقعي — الخارج نهاراً · الواجهة من الجنب



(مصنع وتد الأخشاب — الواقع الافتراضي في آخر صفحة (أو اضغط هنا

الرندر الواقعي — الخارج نهاراً · الخلف والسقف



(مصنع وتد الأخشاب — الواقع الافتراضي في آخر صفحة (أو اضغط هنا

الرندر الواقعي — الداخل · المجلس — الجلسة من المدخل




(مصنع وتد الأخشاب — الواقع الافتراضي في آخر صفحة (أو اضغط هنا

الرندر الواقعي — الداخل · المجلس — الإطلالة على الزجاج



(مصنع وتد الأخشاب — الواقع الافتراضي في آخر صفحة (أو اضغط هنا

(صور 360° — تنعرض متحركة في الجولة الافتراضية (اضغط هنا

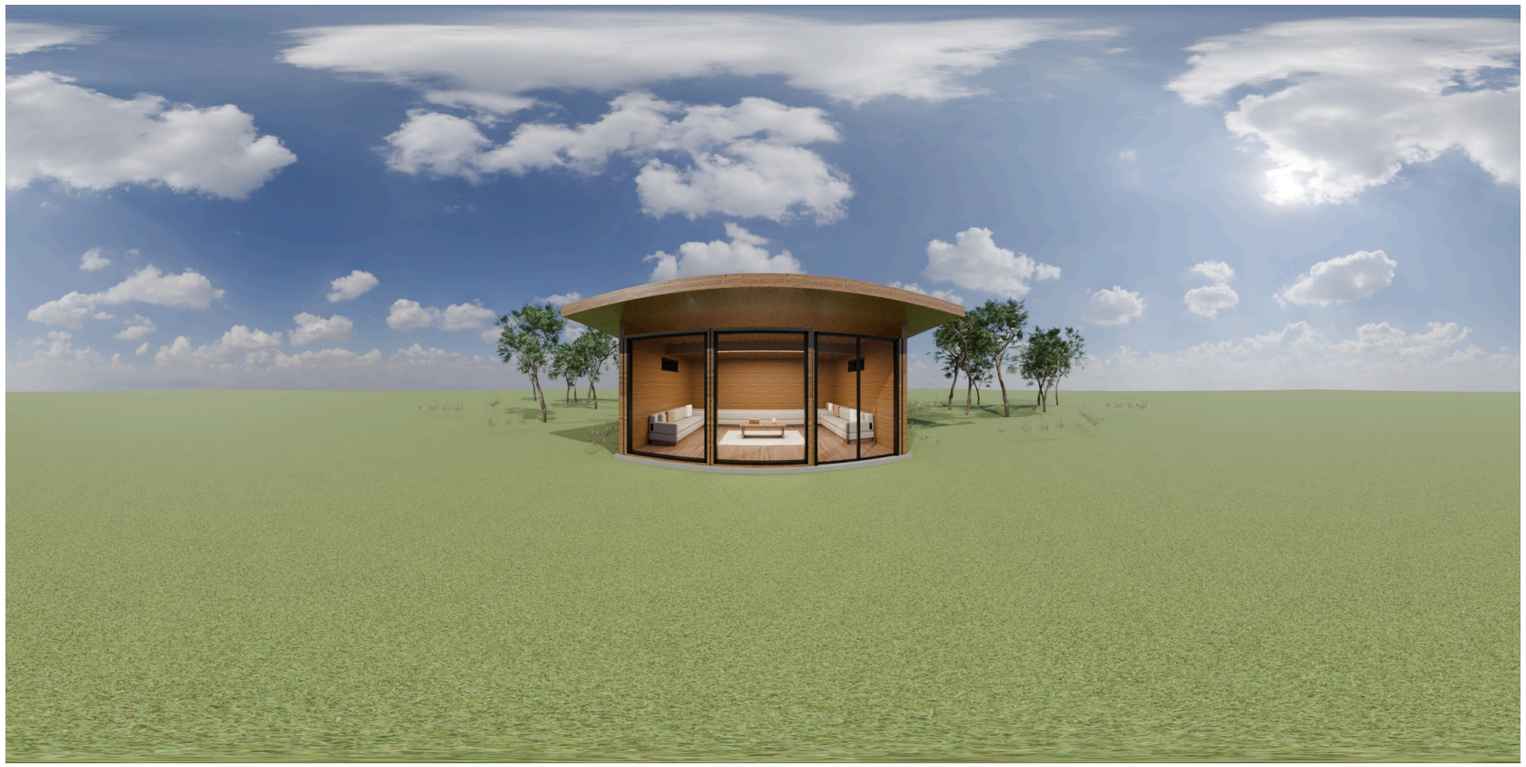



مصنع وتد الأخشاب

جرّب الواقع الافتراضي

.المجلس الحديث بواجهة زجاج — امشِ داخل التصميم: الحوش والجلسات والدورين، ولف 360° بكل غرفة. امسح الرمز بكاميرا الجوال أو اضغط على الزر



افتح الجولة بالنهار

افتح الجولة بالليل والإنارة شغالة

الرابط: https://watad-wood.com/majlis-modern/